

4 3 2 1

F


E

D

C

B


A

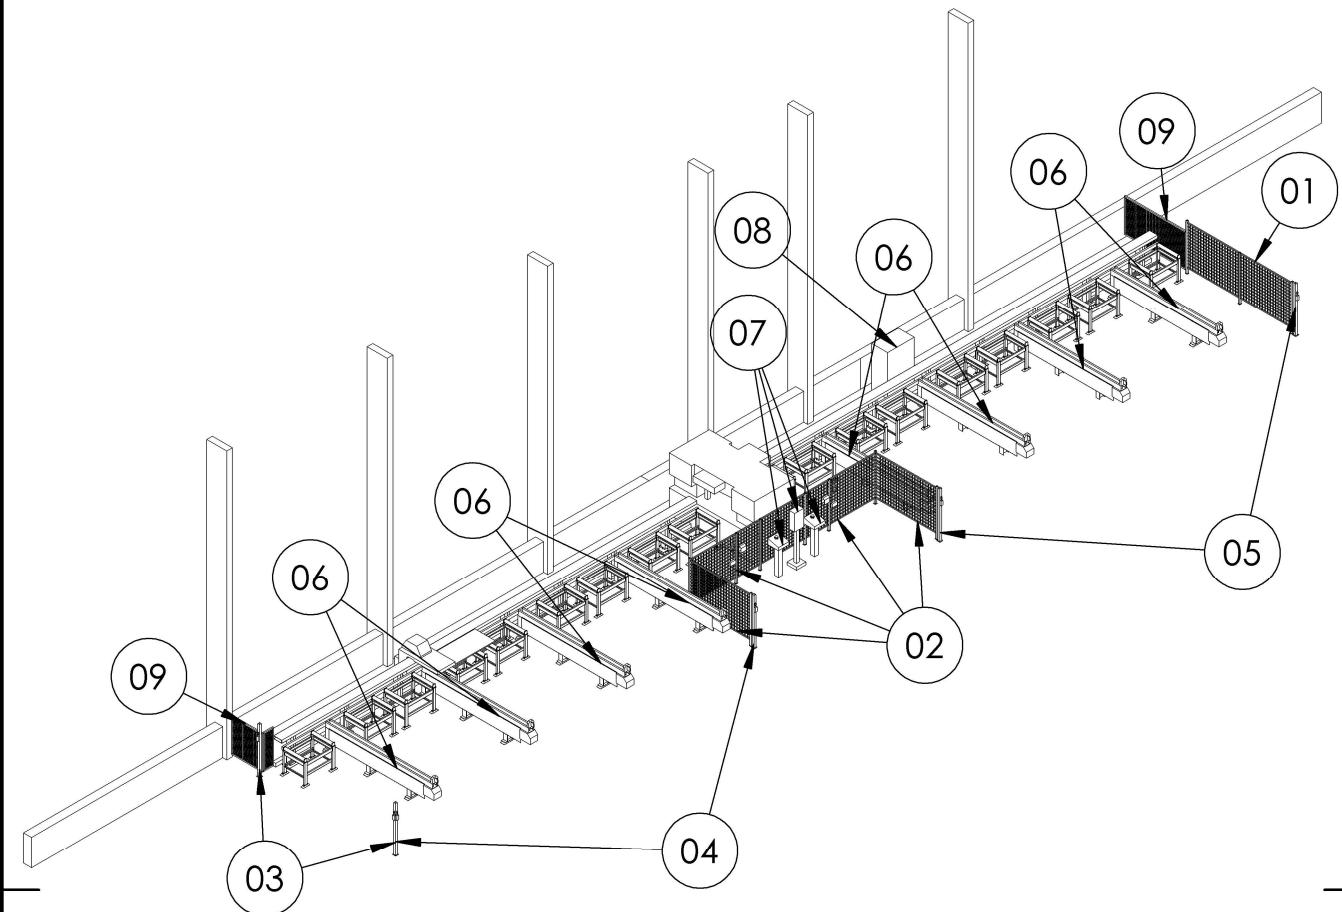

| ITENS | NOMES |
|-------|--|
| 01 | PROTEÇÃO FIXA 01 |
| 02 | PROTEÇÃO FIXA C/ PORTAS DE INTERTRAVAMENTO |
| 03 | SENSORES CORTINA DE LUZ 01 |
| 04 | SENSORES CORTINA DE LUZ 02 |
| 05 | SENSORES CORTINA DE LYZ 03 |
| 06 | PROTEÇÃO FIXA LATERAL AO EQUIPAMENTO |
| 07 | PAINEL DE COMANDO 01 |
| 08 | PAINEL DE COMANDO 02 |
| 09 | PROTEÇÃO FIXA ESISTENTE |

EMPRESA:**GRUPO NORMATEC****CLIENTE:**ISOESTE METALICA INDUSTRIA E COMERCIO LTDA.
CNPJ: 37.249.299/0001-22**DESCRIÇÃO:****CORTE LAMINADORA KATANA****FABRICANTE:** FICEP**APROVAÇÃO:** MATEUS FIALHO**DATA:** FEVEREIRO/2024**TAG:** COR - 1300**ANO:** N/C**NÚMERO:** 33730**ESCALA:** 1 : 200**MATERIAL:**

4 3 2 1

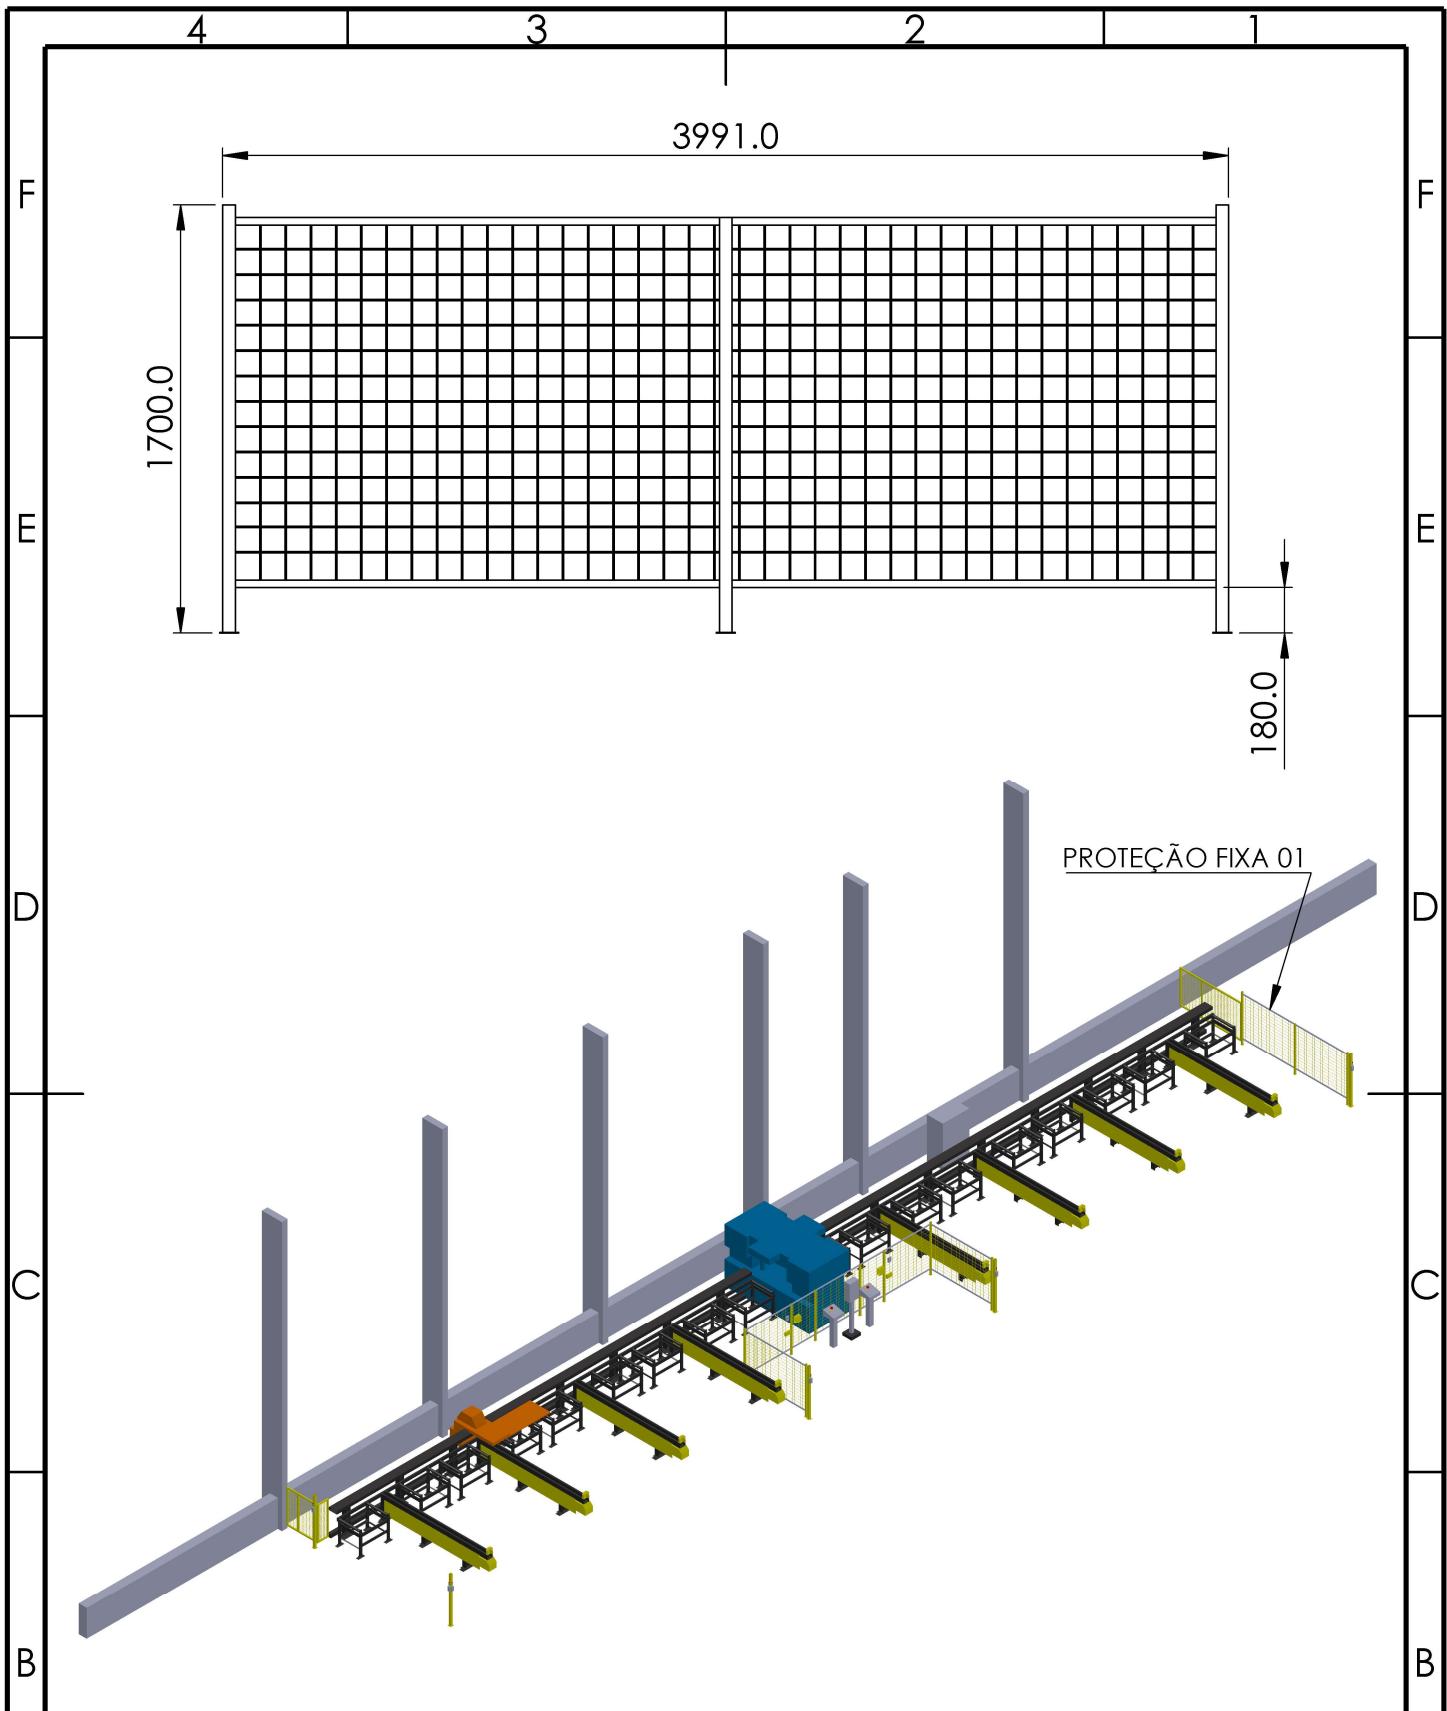

EMPRESA:

GRUPO NORMATEC

CLIENTE:

ISOESTE METALICA INDUSTRIA E COMERCIO LTDA.
CNPJ: 37.249.299/0001-22

DESCRIÇÃO:

CORTE LAMINADORA KATANA

FABRICANTE: FICEP

APROVAÇÃO: MATEUS FIALHO

DATA: FEVEREIRO/2024


TAG: COR - 1300

ANO: N/C

NÚMERO: 33730

ESCALA: S/E

MATERIAL:

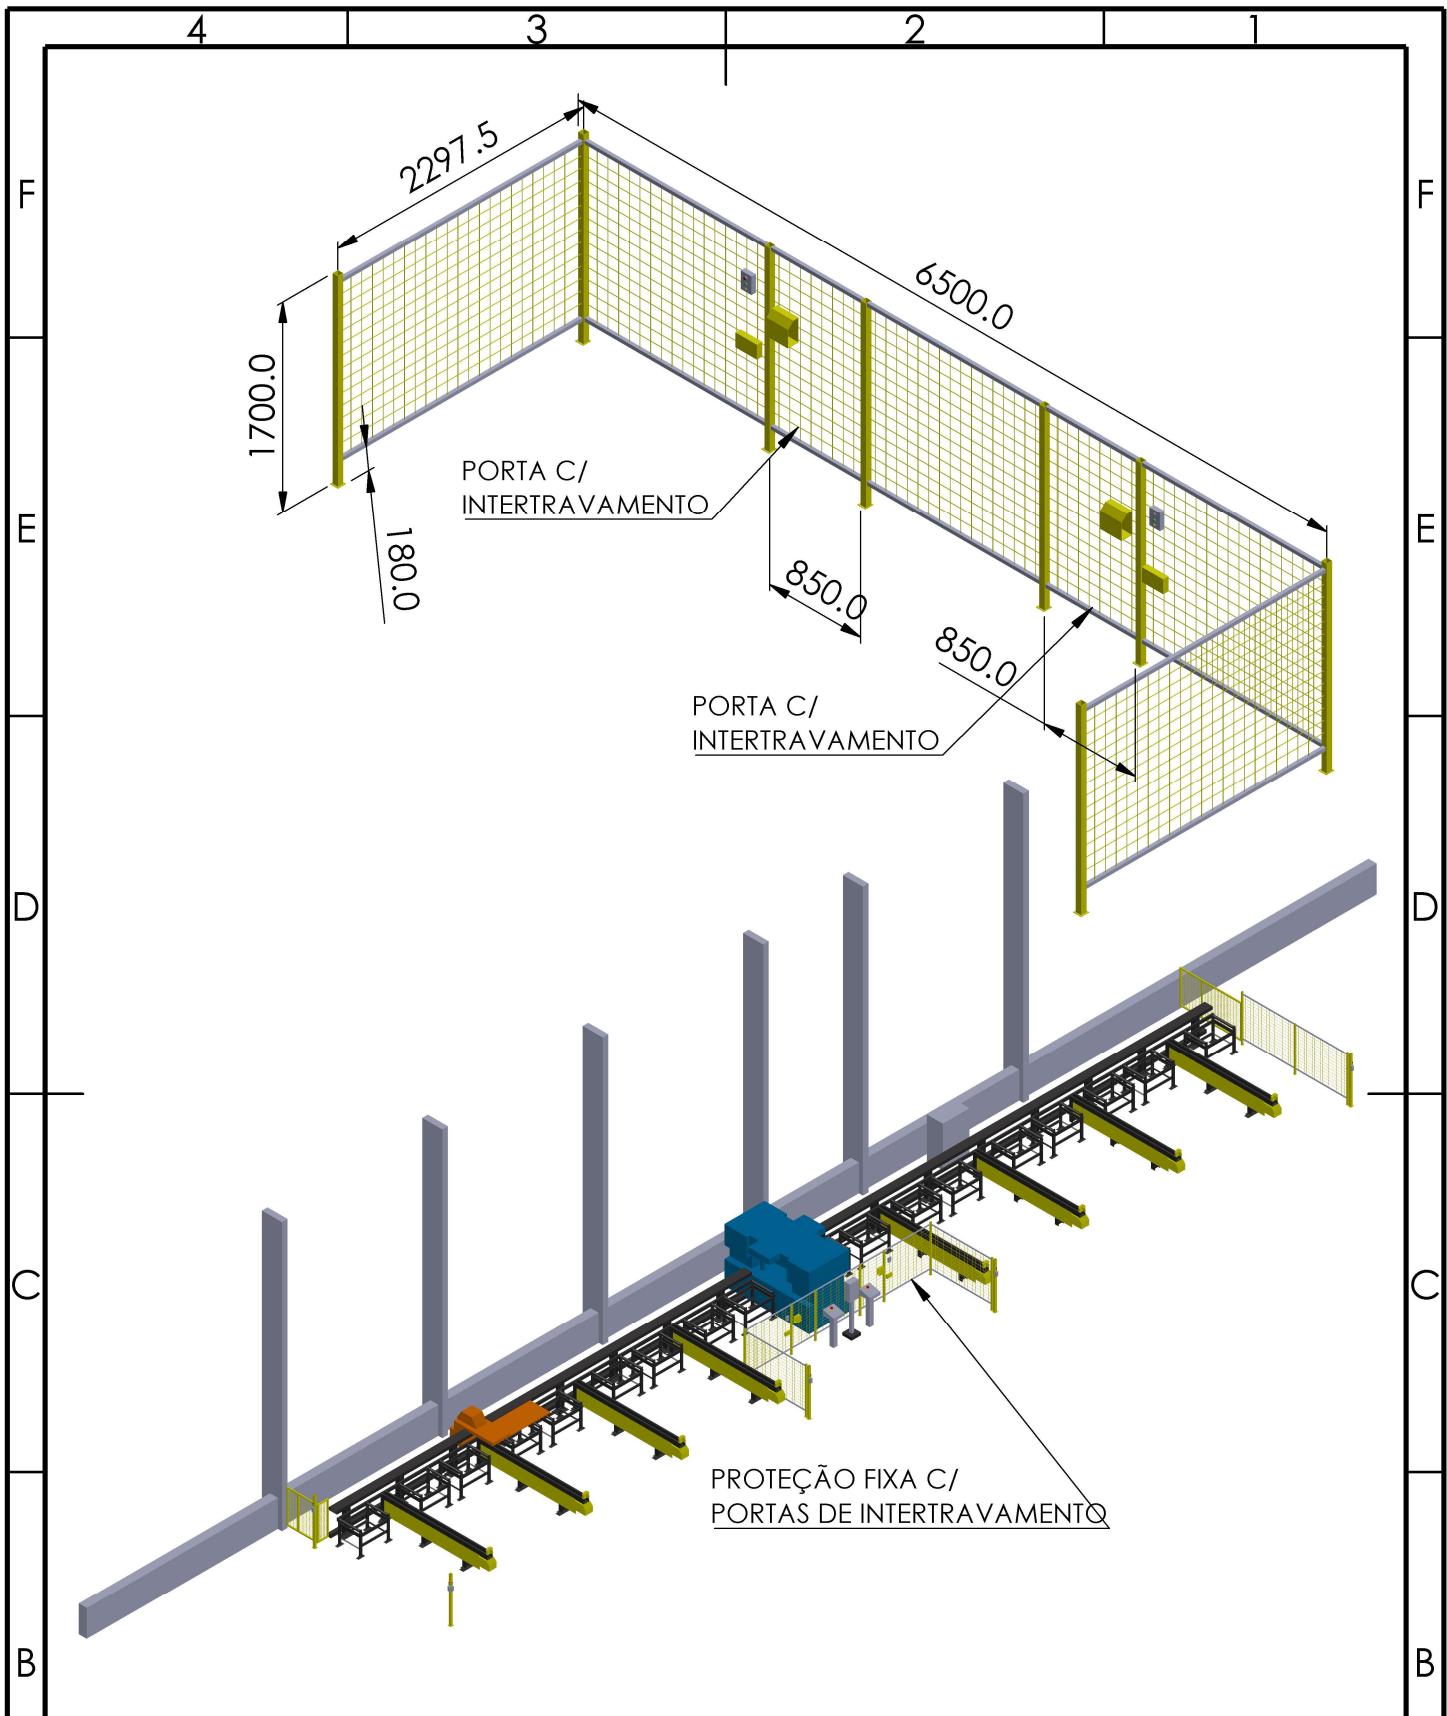

EMPRESA:

GRUPO NORMATEC

CLIENTE:

ISOESTE METALICA INDUSTRIA E COMERCIO LTDA.
CNPJ: 37.249.299/0001-22

DESCRIÇÃO:

CORTE LAMINADORA KATANA

FABRICANTE: FICEP

APROVAÇÃO: MATEUS FIALHO

DATA: FEVEREIRO/2024

TAG: COR - 1300

ANO: N/C

NÚMERO: 33730

ESCALA: S/E

MATERIAL:

4

3

2

1

QUANTIDADE: 16X

F

F

E

E

D

D

C

C

B

B



EMPRESA:**GRUPO NORMATEC****CLIENTE:**ISOESTE METALICA INDUSTRIA E COMERCIO LTDA.
CNPJ: 37.249.299/0001-22**DESCRIÇÃO:****CORTE LAMINADORA KATANA****FABRICANTE:** FICEP**APROVAÇÃO:** MATEUS FIALHO**DATA:** FEVEREIRO/2024**TAG:** COR - 1300**ANO:** N/C**NÚMERO:** 33730**ESCALA:** S/E**MATERIAL:**

4

3

2

1

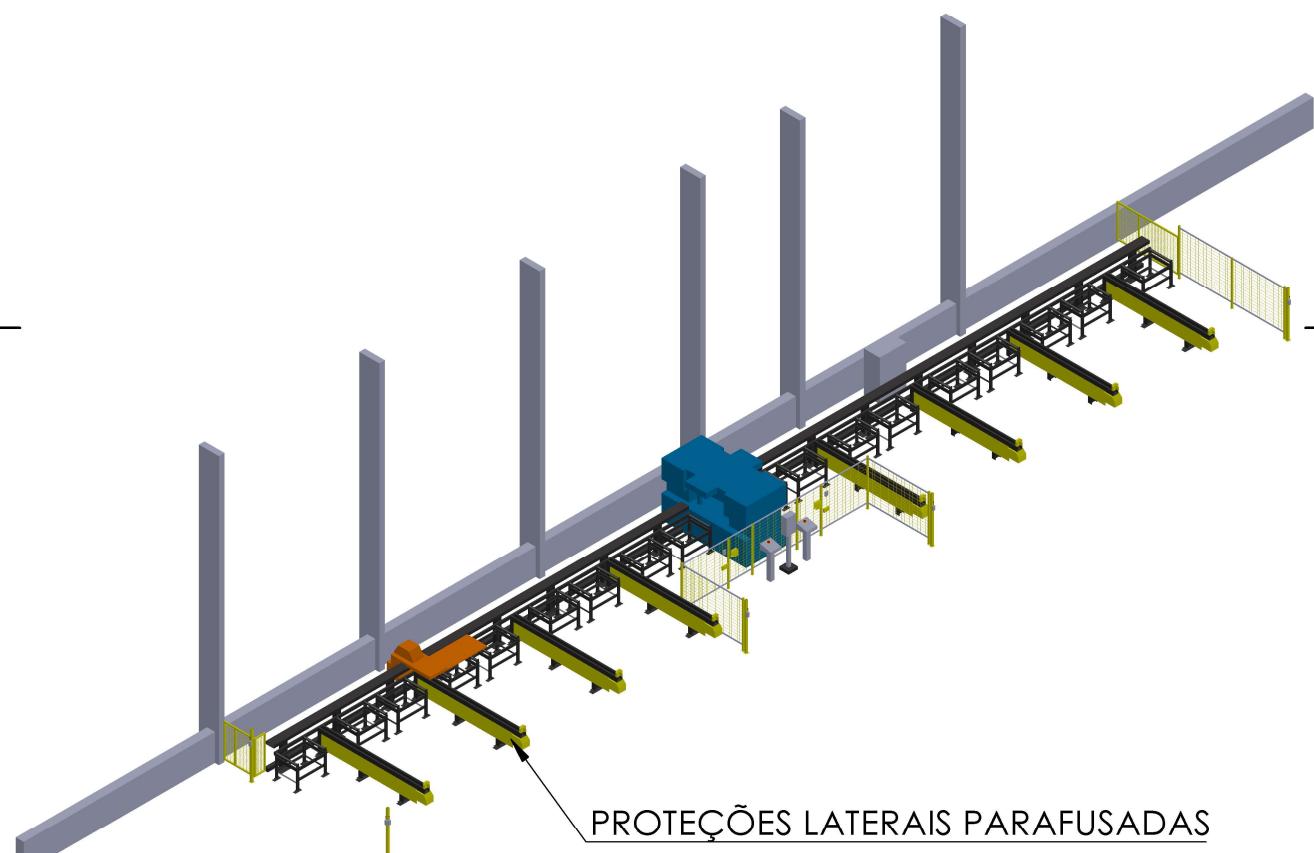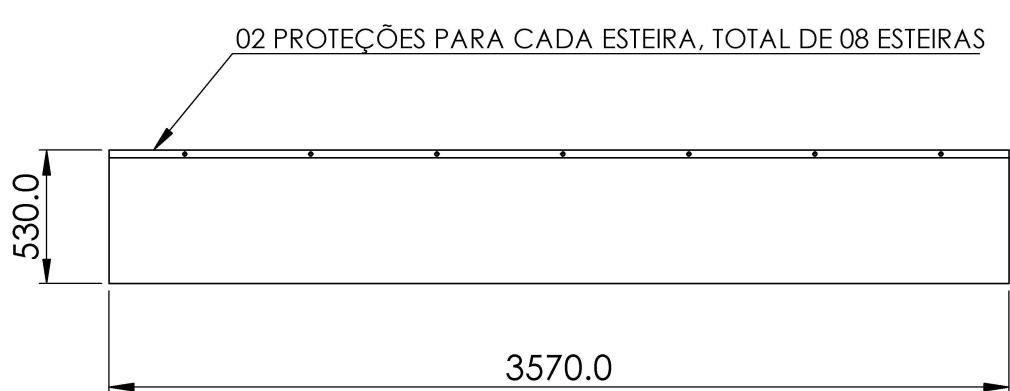**EMPRESA:****GRUPO NORMATEC****CLIENTE:**ISOESTE METALICA INDUSTRIA E COMERCIO LTDA.
CNPJ: 37.249.299/0001-22**DESCRIÇÃO:****CORTE LAMINADORA KATANA****FABRICANTE:** FICEP**APROVAÇÃO:** MATEUS FIALHO**DATA:** FEVEREIRO/2024**TAG:** COR - 1300**ANO:** N/C**NÚMERO:** 33730**ESCALA:** S/E**MATERIAL:**