

ITENS	NOMES
01	PROTEÇÃO FIXA 01
02	PROTEÇÃO FIXA 02
03	SENSOR CORTINA DE LUZ
04	ESCADA DE ACESSO C/ GUARDA CORPO
05	GUARDA CORPO P/ PLATAFORMA 01
06	GUARDA CORPO P/ PLATAFORMA 02
07	GUARDA CORPO P/ PLATAFORMA 03
08	GUARDA CORPO P/ PLATAFORMA 04
09	GUARDA CORPO P/ PLATAFORMA 05
10	GUARDA CORPO P/ PLATAFORMA 06
11	GUARDA CORPO P/ PLATAFORMA 07
12	PLATAFORMA
13	PAINEL ELÉTRICO
14	PERFILADEIRA CANTONEIRA

EMPRESA:

GRUPO NORMATEC

CLIENTE:

ISOESTE METALICA INDUSTRIA E COMERCIO LTDA.
CNPJ: 37.249.299/0001-22

DESCRÍÇÃO:

CORTA FLECHA

FABRICANTE: N/C

APROVAÇÃO: MATHEUS FIALHO

DATA: JANEIRO/2024


TAG: CRF - 1300



ANO: N/C

NÚMERO: N/C

ESCALA: 1 : 60

MATERIAL:

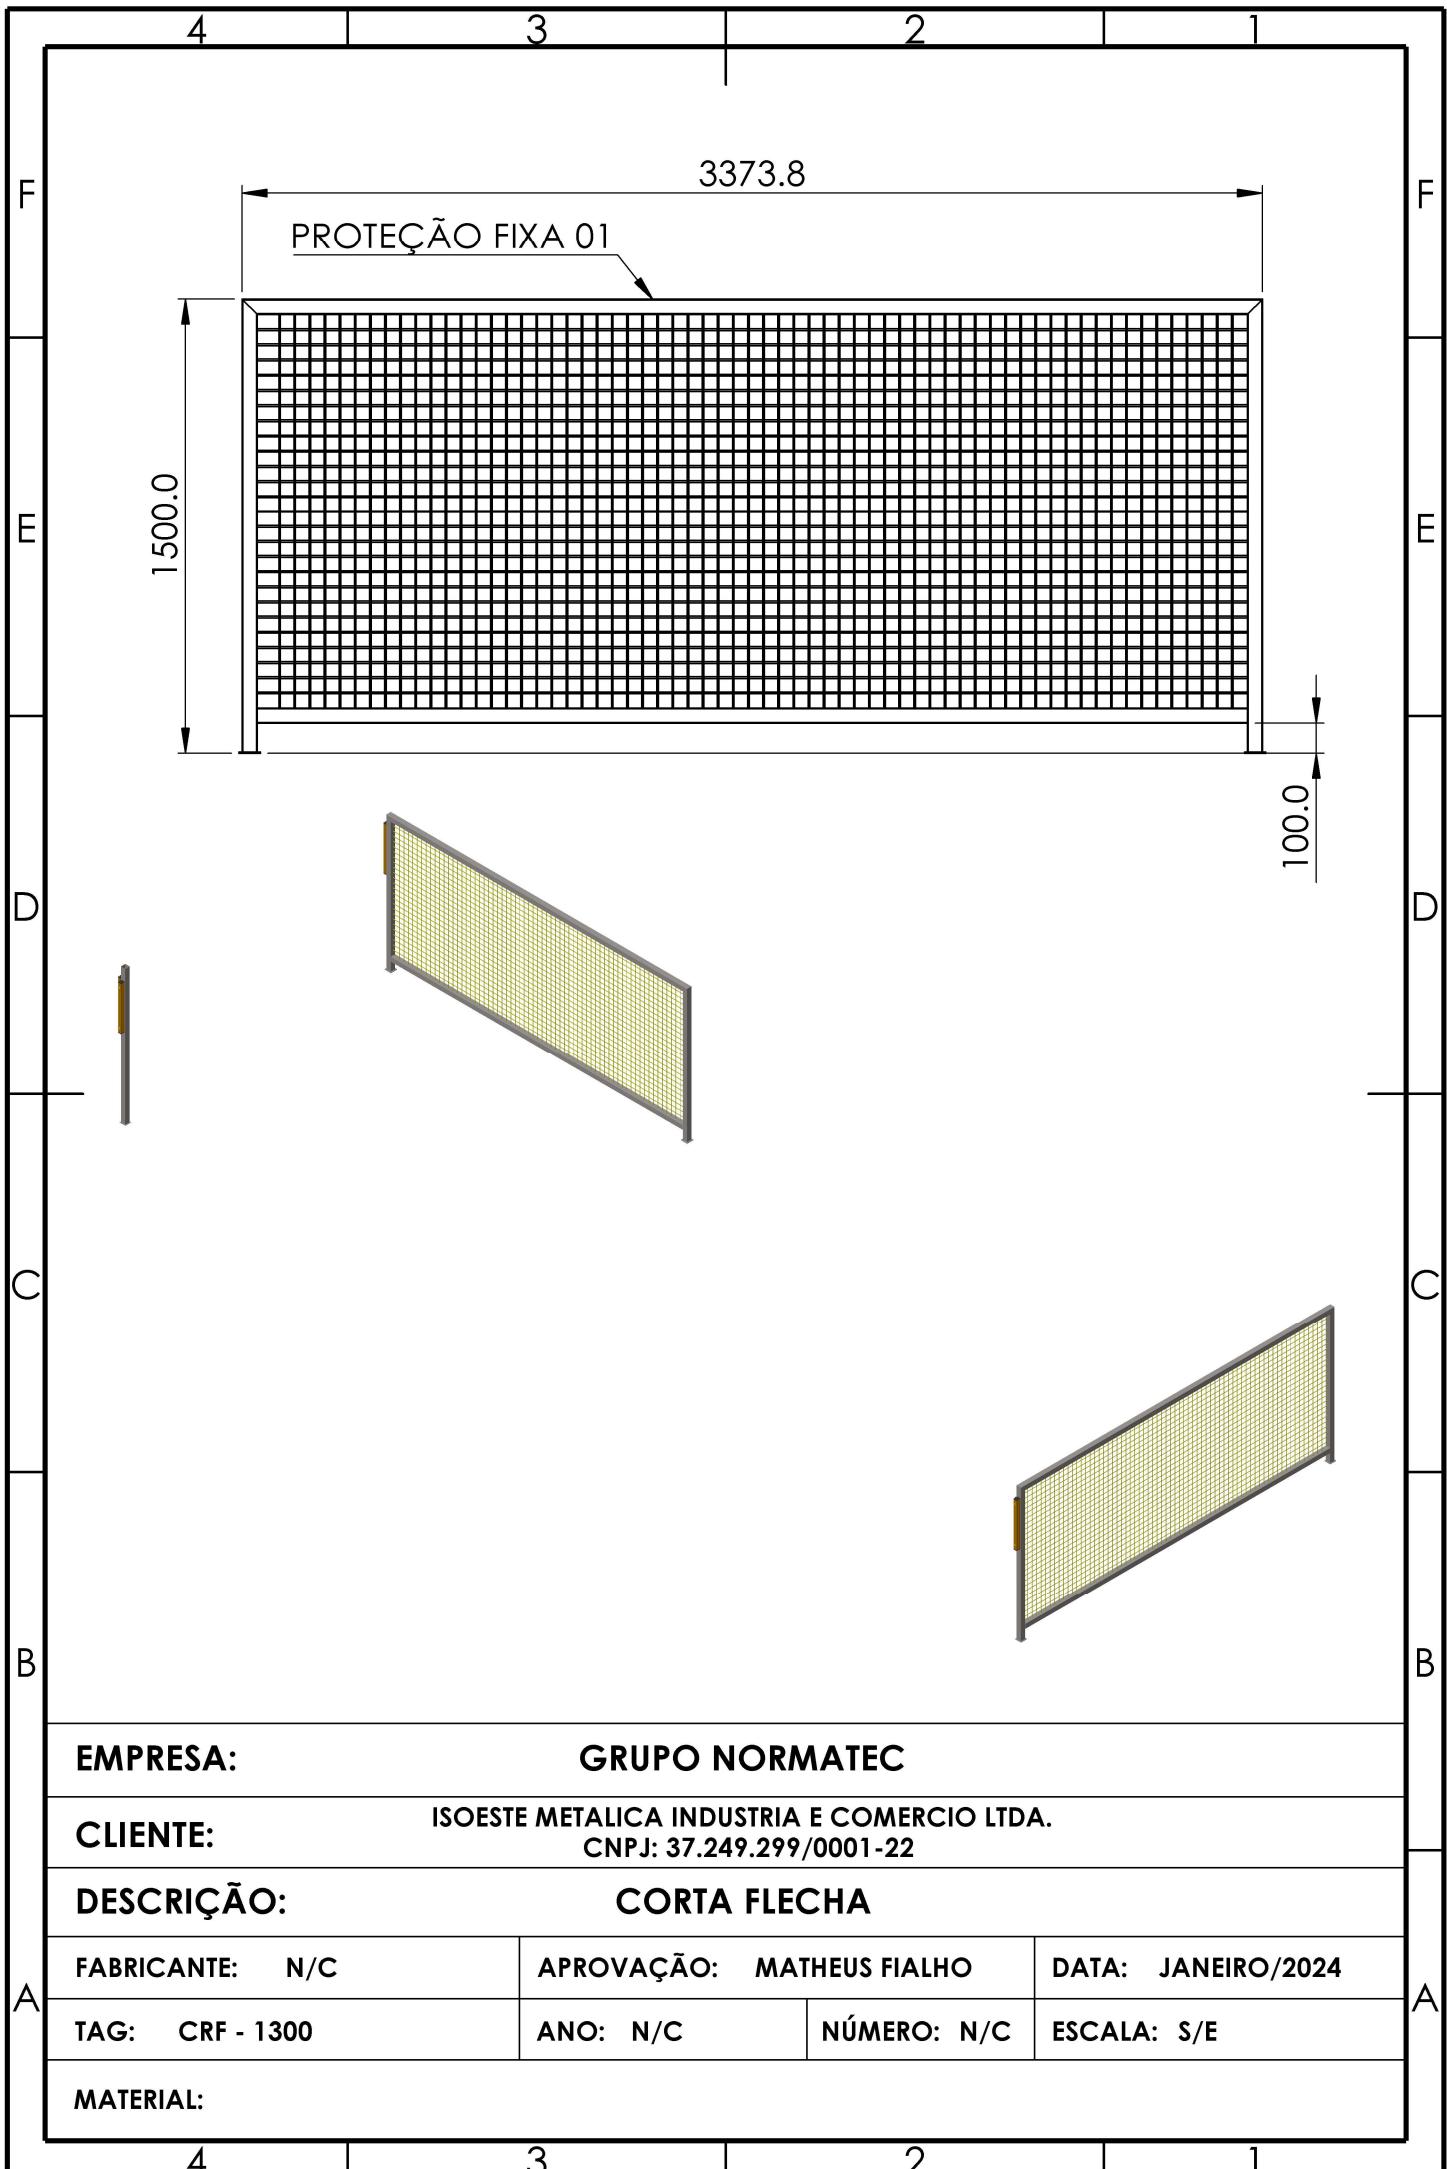

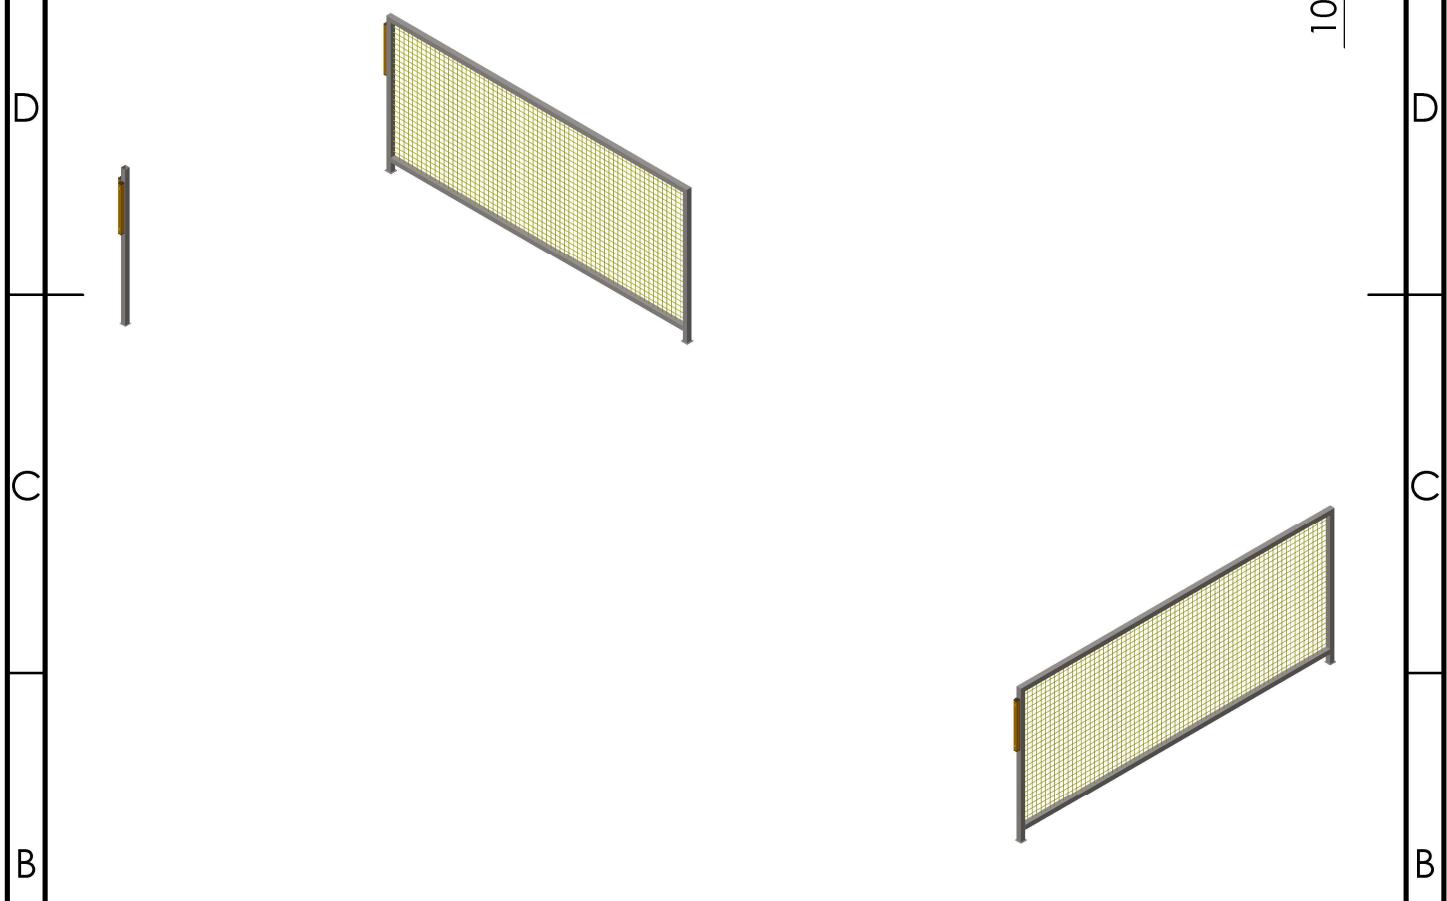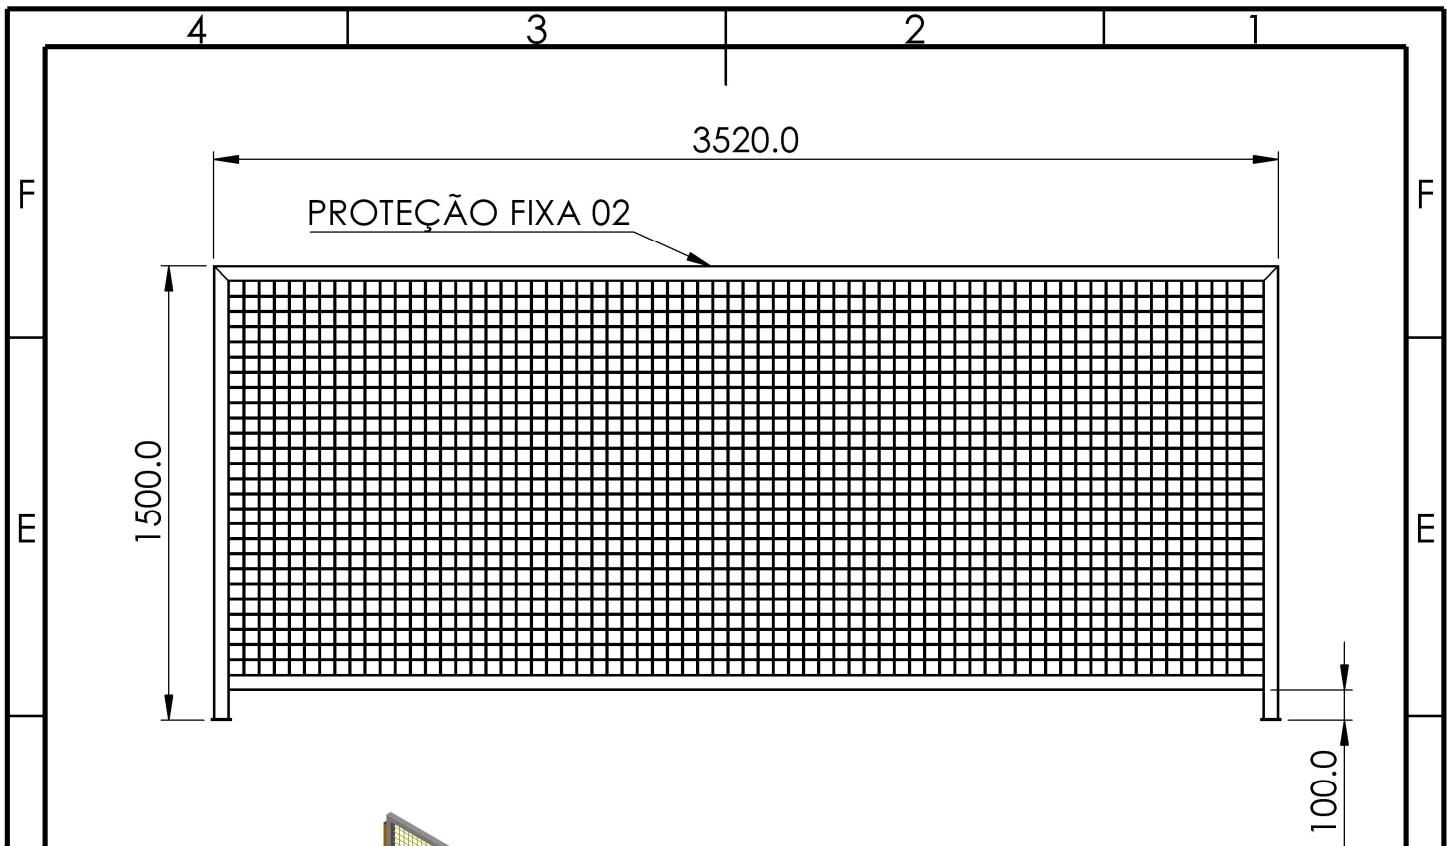

EMPRESA:

GRUPO NORMATEC

CLIENTE:

**ISOESTE METALICA INDUSTRIA E COMERCIO LTDA.
CNPJ: 37.249.299/0001-22**

DESCRIÇÃO:

CORTA FLECHA

FABRICANTE: N/C

APROVAÇÃO: MATHEUS FIALHO

DATA: JANEIRO/2024


TAG: CRF - 1300

ANO: N/C

NÚMERO: N/C

ESCALA: S/E

MATERIAL:

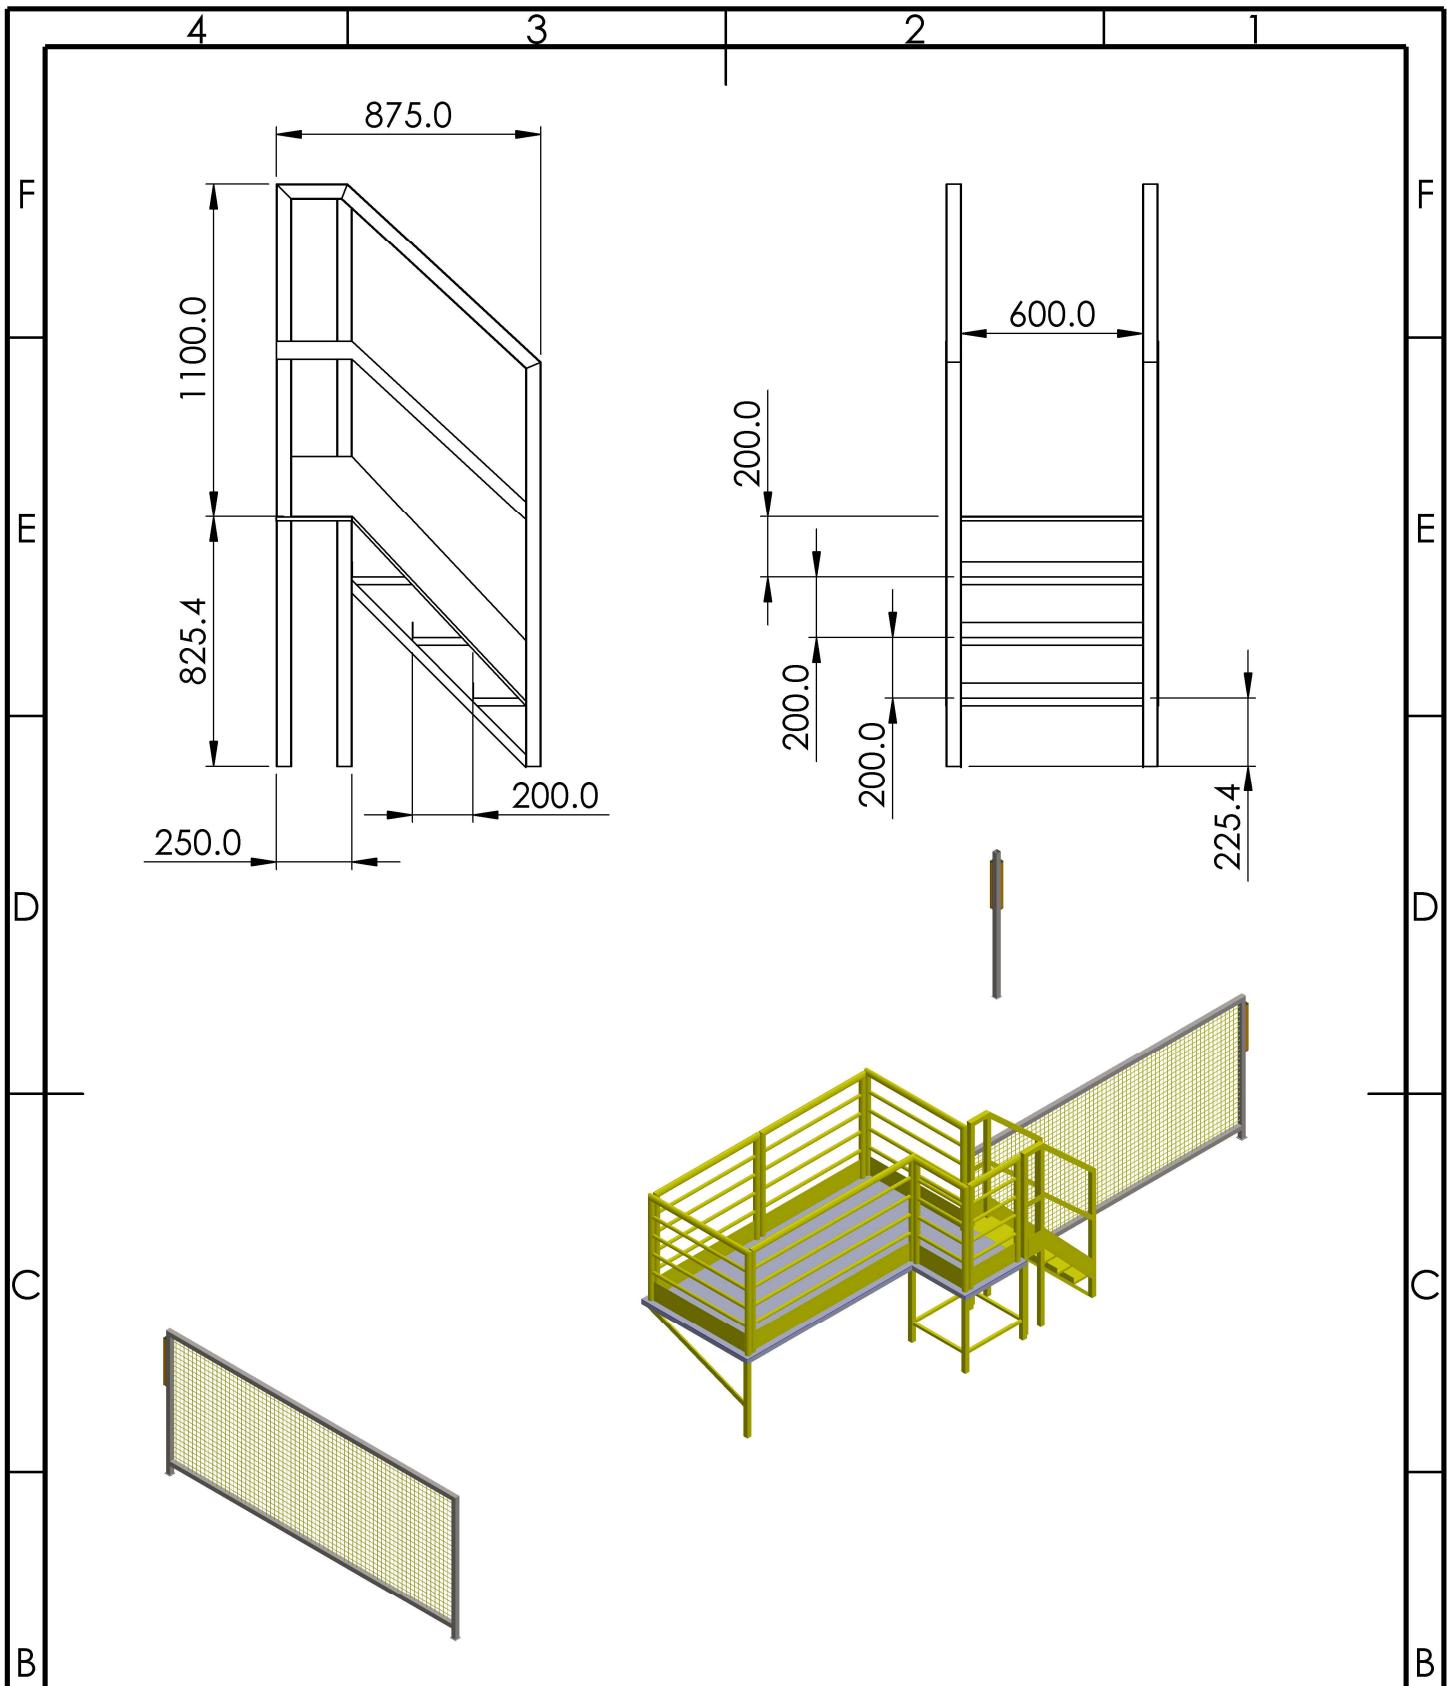

EMPRESA:

GRUPO NORMATEC

CLIENTE:

ISOESTE METALICA INDUSTRIA E COMERCIO LTDA.
CNPJ: 37.249.299/0001-22

DESCRIÇÃO:

CORTA FLECHA

FABRICANTE: N/C

APROVAÇÃO: MATHEUS FIALHO

DATA: JANEIRO/2024


TAG: CRF - 1300

ANO: N/C

NÚMERO: N/C

ESCALA: S/E

MATERIAL:

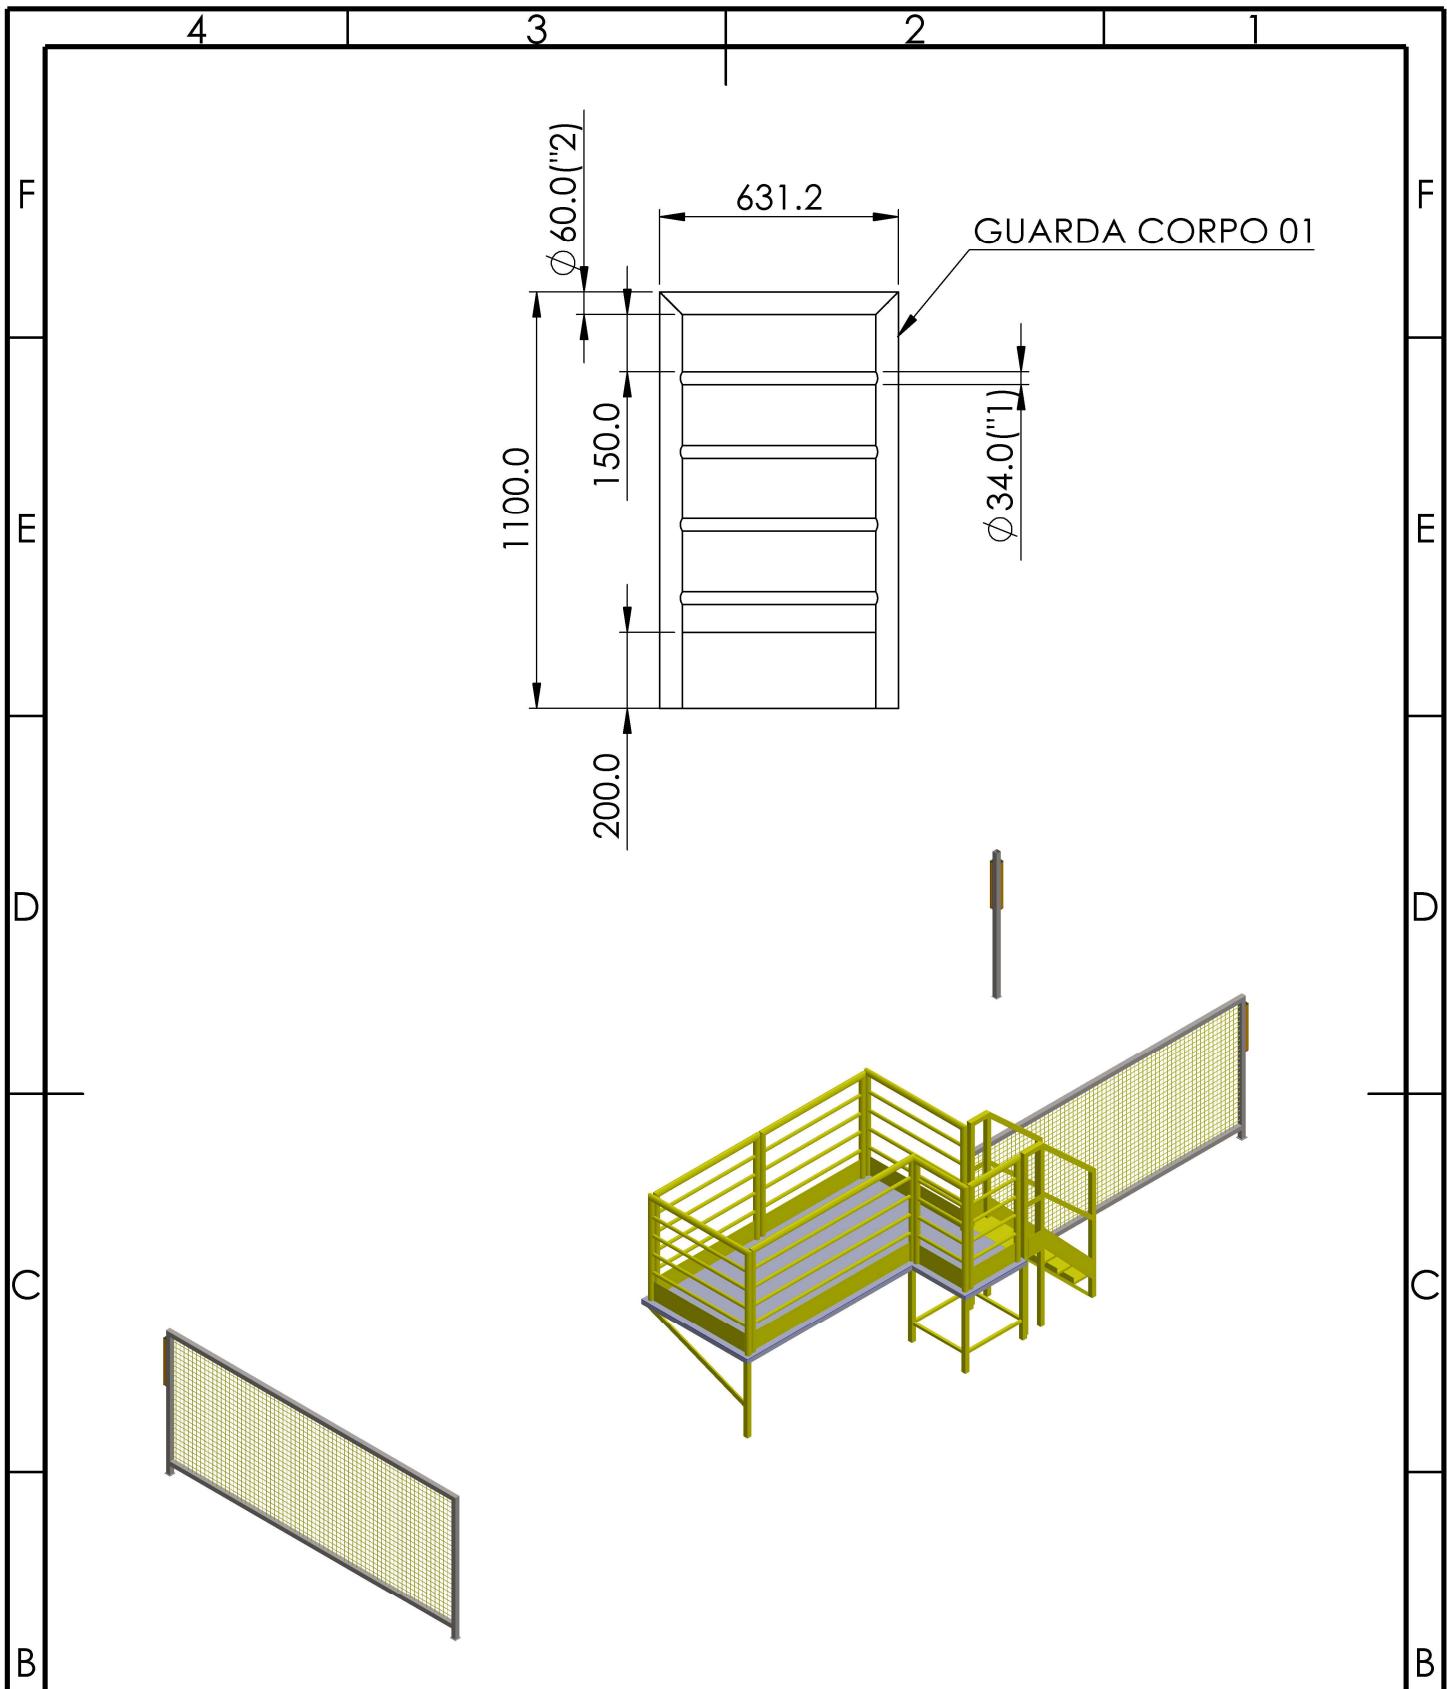

EMPRESA:

GRUPO NORMATEC

CLIENTE:

ISOESTE METALICA INDUSTRIA E COMERCIO LTDA.
CNPJ: 37.249.299/0001-22

DESCRIÇÃO:

CORTA FLECHA

FABRICANTE: N/C

APROVAÇÃO: MATHEUS FIALHO

DATA: JANEIRO/2024


TAG: CRF - 1300

ANO: N/C

NÚMERO: N/C

ESCALA: S/E

MATERIAL:

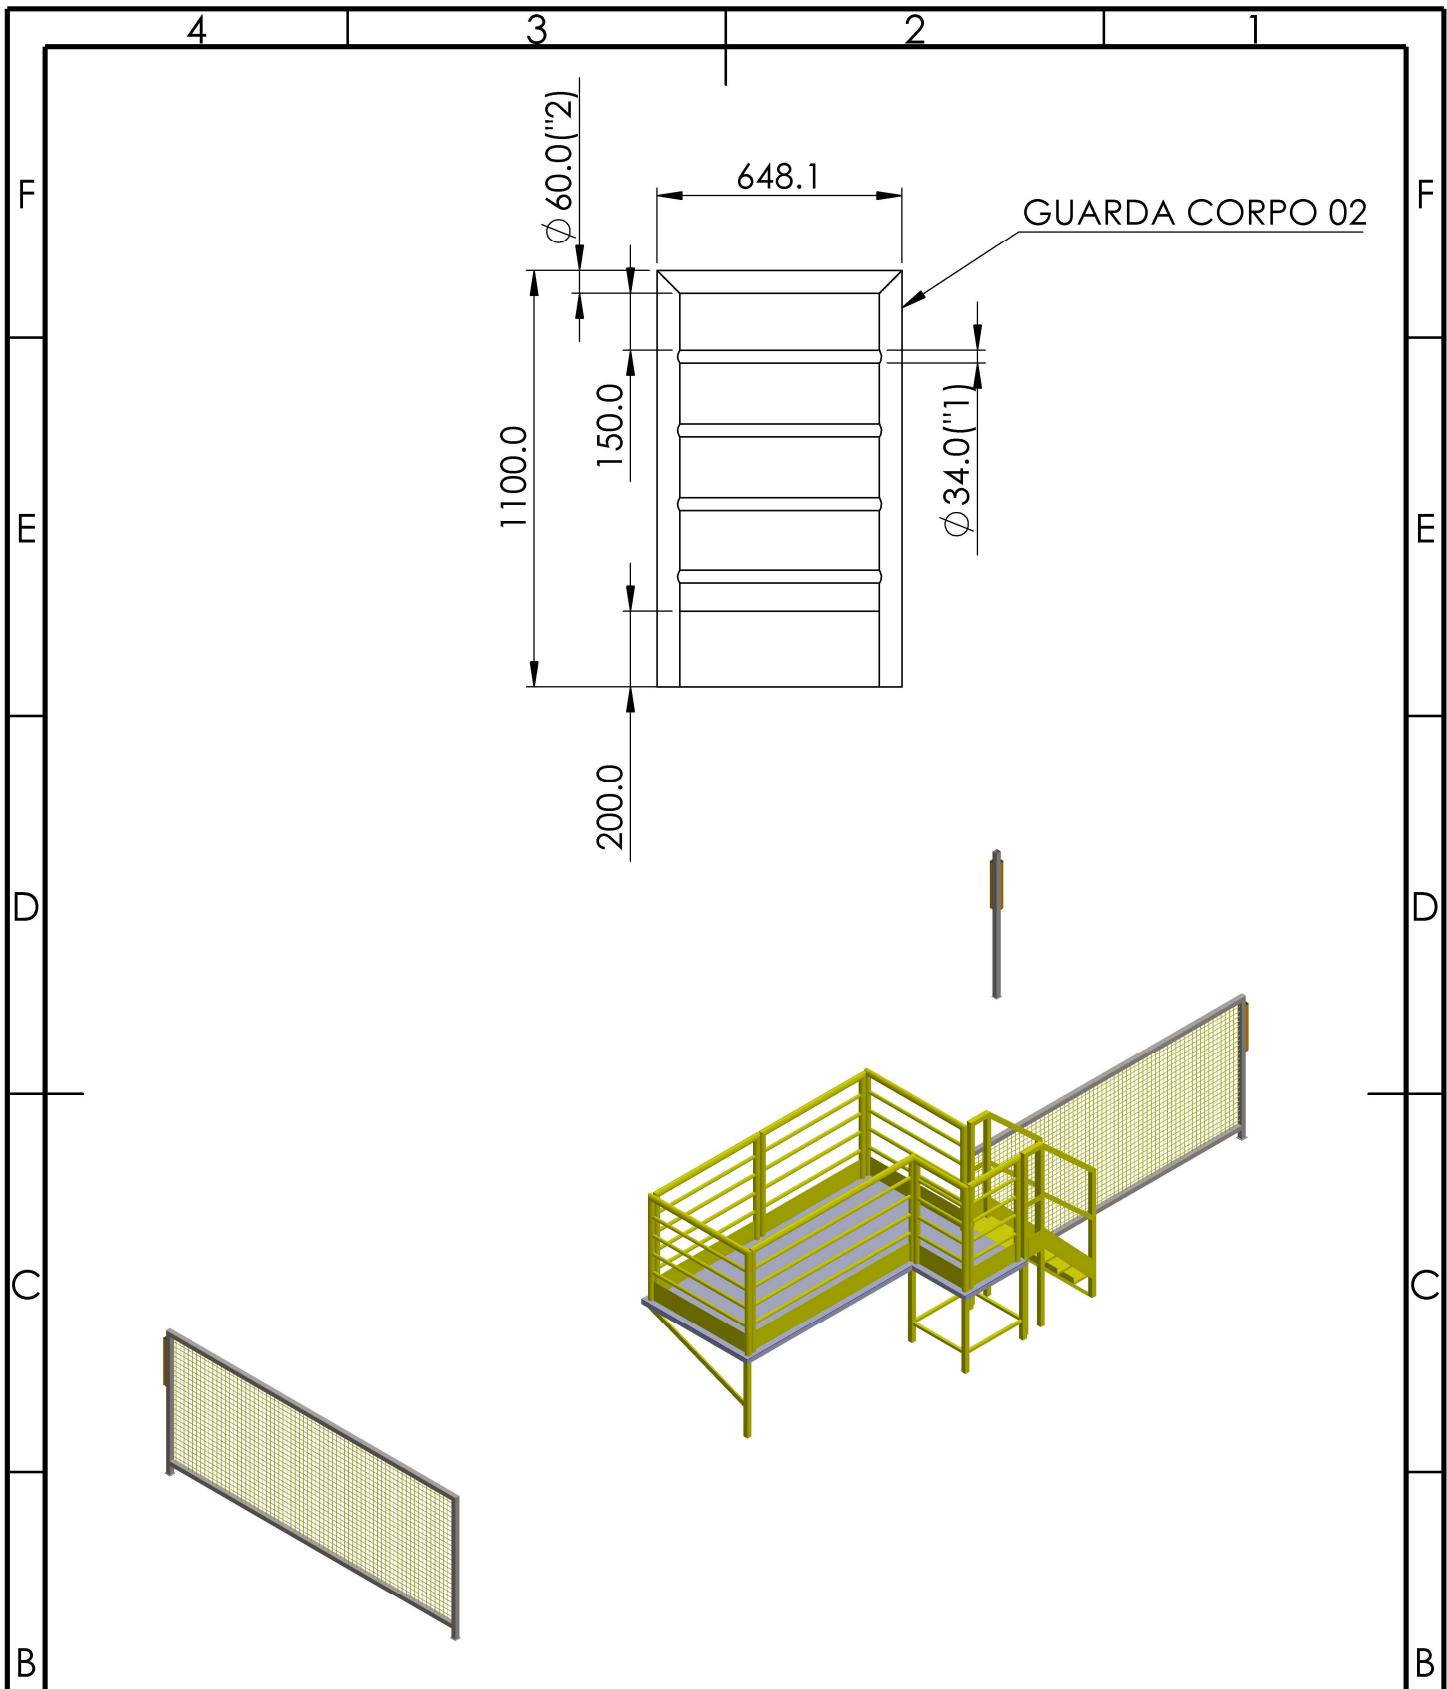

EMPRESA:

GRUPO NORMATEC

CLIENTE:

ISOESTE METALICA INDUSTRIA E COMERCIO LTDA.
CNPJ: 37.249.299/0001-22

DESCRIÇÃO:

CORTA FLECHA

FABRICANTE: N/C

APROVAÇÃO: MATHEUS FIALHO

DATA: JANEIRO/2024


TAG: CRF - 1300

ANO: N/C

NÚMERO: N/C

ESCALA: S/E

MATERIAL:

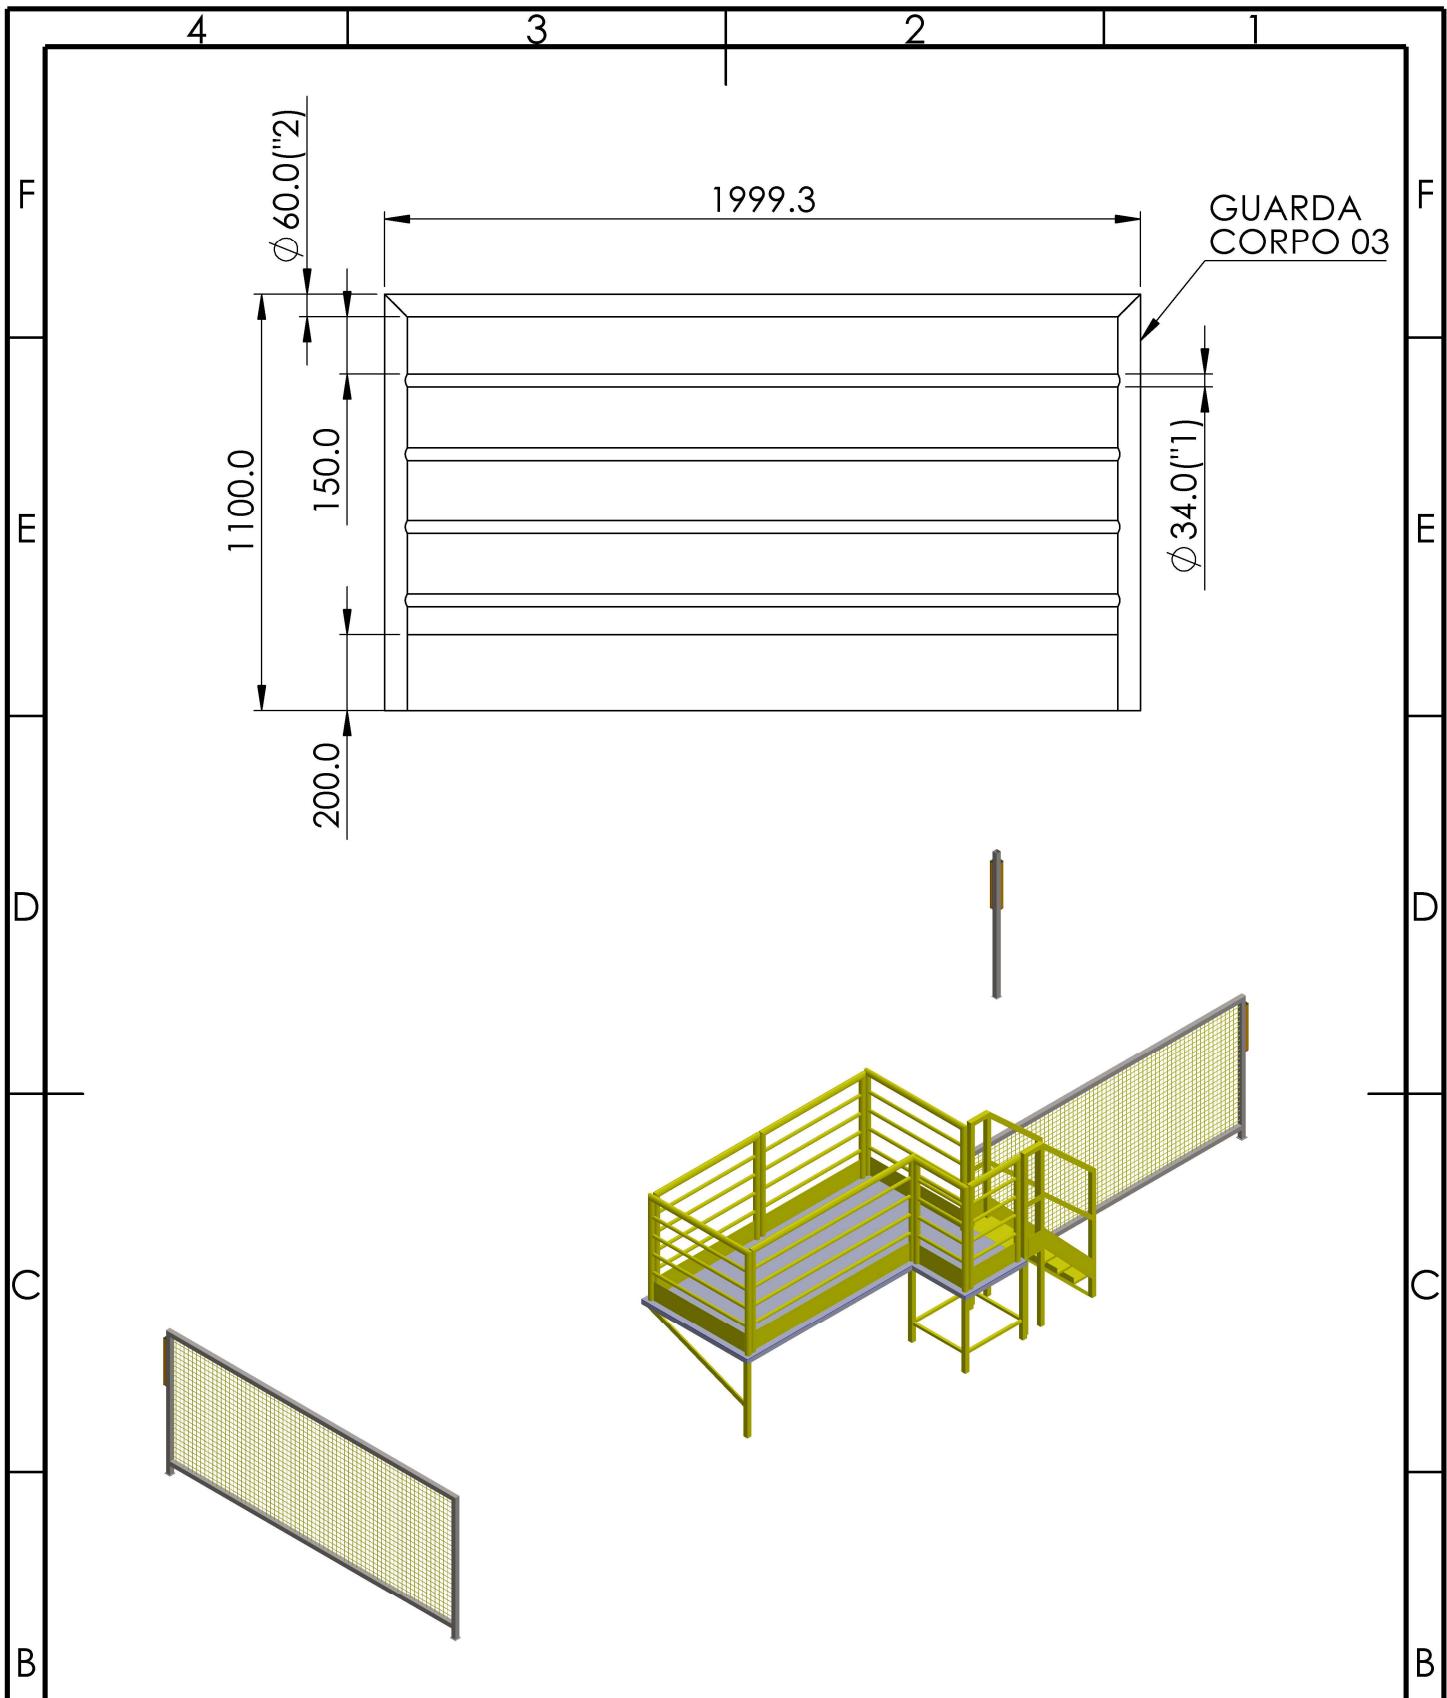

EMPRESA:

GRUPO NORMATEC

CLIENTE:

ISOESTE METALICA INDUSTRIA E COMERCIO LTDA.
CNPJ: 37.249.299/0001-22

DESCRIÇÃO:

CORTA FLECHA

FABRICANTE: N/C

APROVAÇÃO: MATHEUS FIALHO

DATA: JANEIRO/2024


TAG: CRF - 1300

ANO: N/C

NÚMERO: N/C

ESCALA: S/E

MATERIAL:

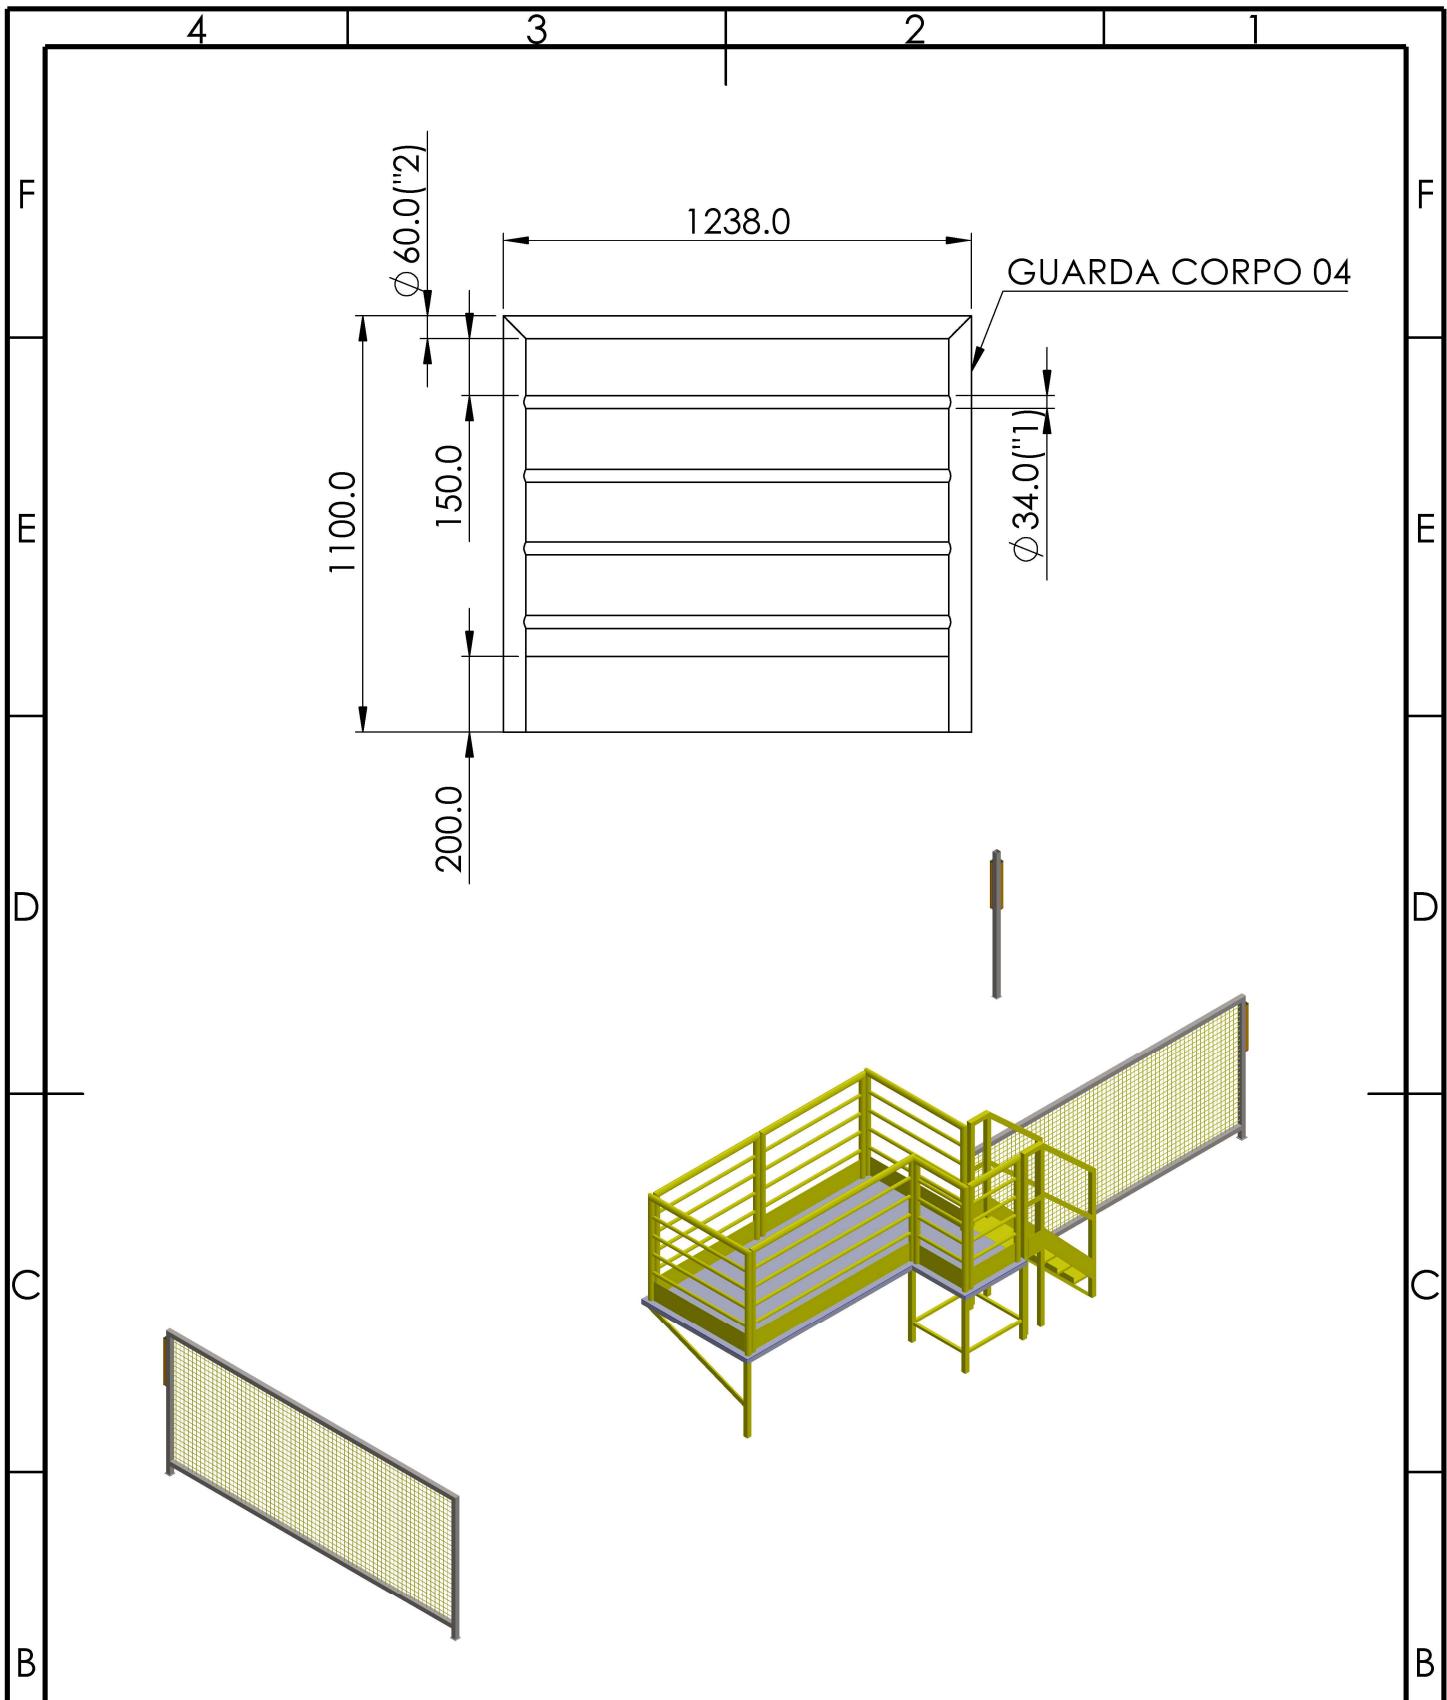

EMPRESA:

GRUPO NORMATEC

CLIENTE:

ISOESTE METALICA INDUSTRIA E COMERCIO LTDA.
CNPJ: 37.249.299/0001-22

DESCRIÇÃO:

CORTA FLECHA

FABRICANTE: N/C

APROVAÇÃO: MATHEUS FIALHO

DATA: JANEIRO/2024


TAG: CRF - 1300

ANO: N/C

NÚMERO: N/C

ESCALA: S/E

MATERIAL:

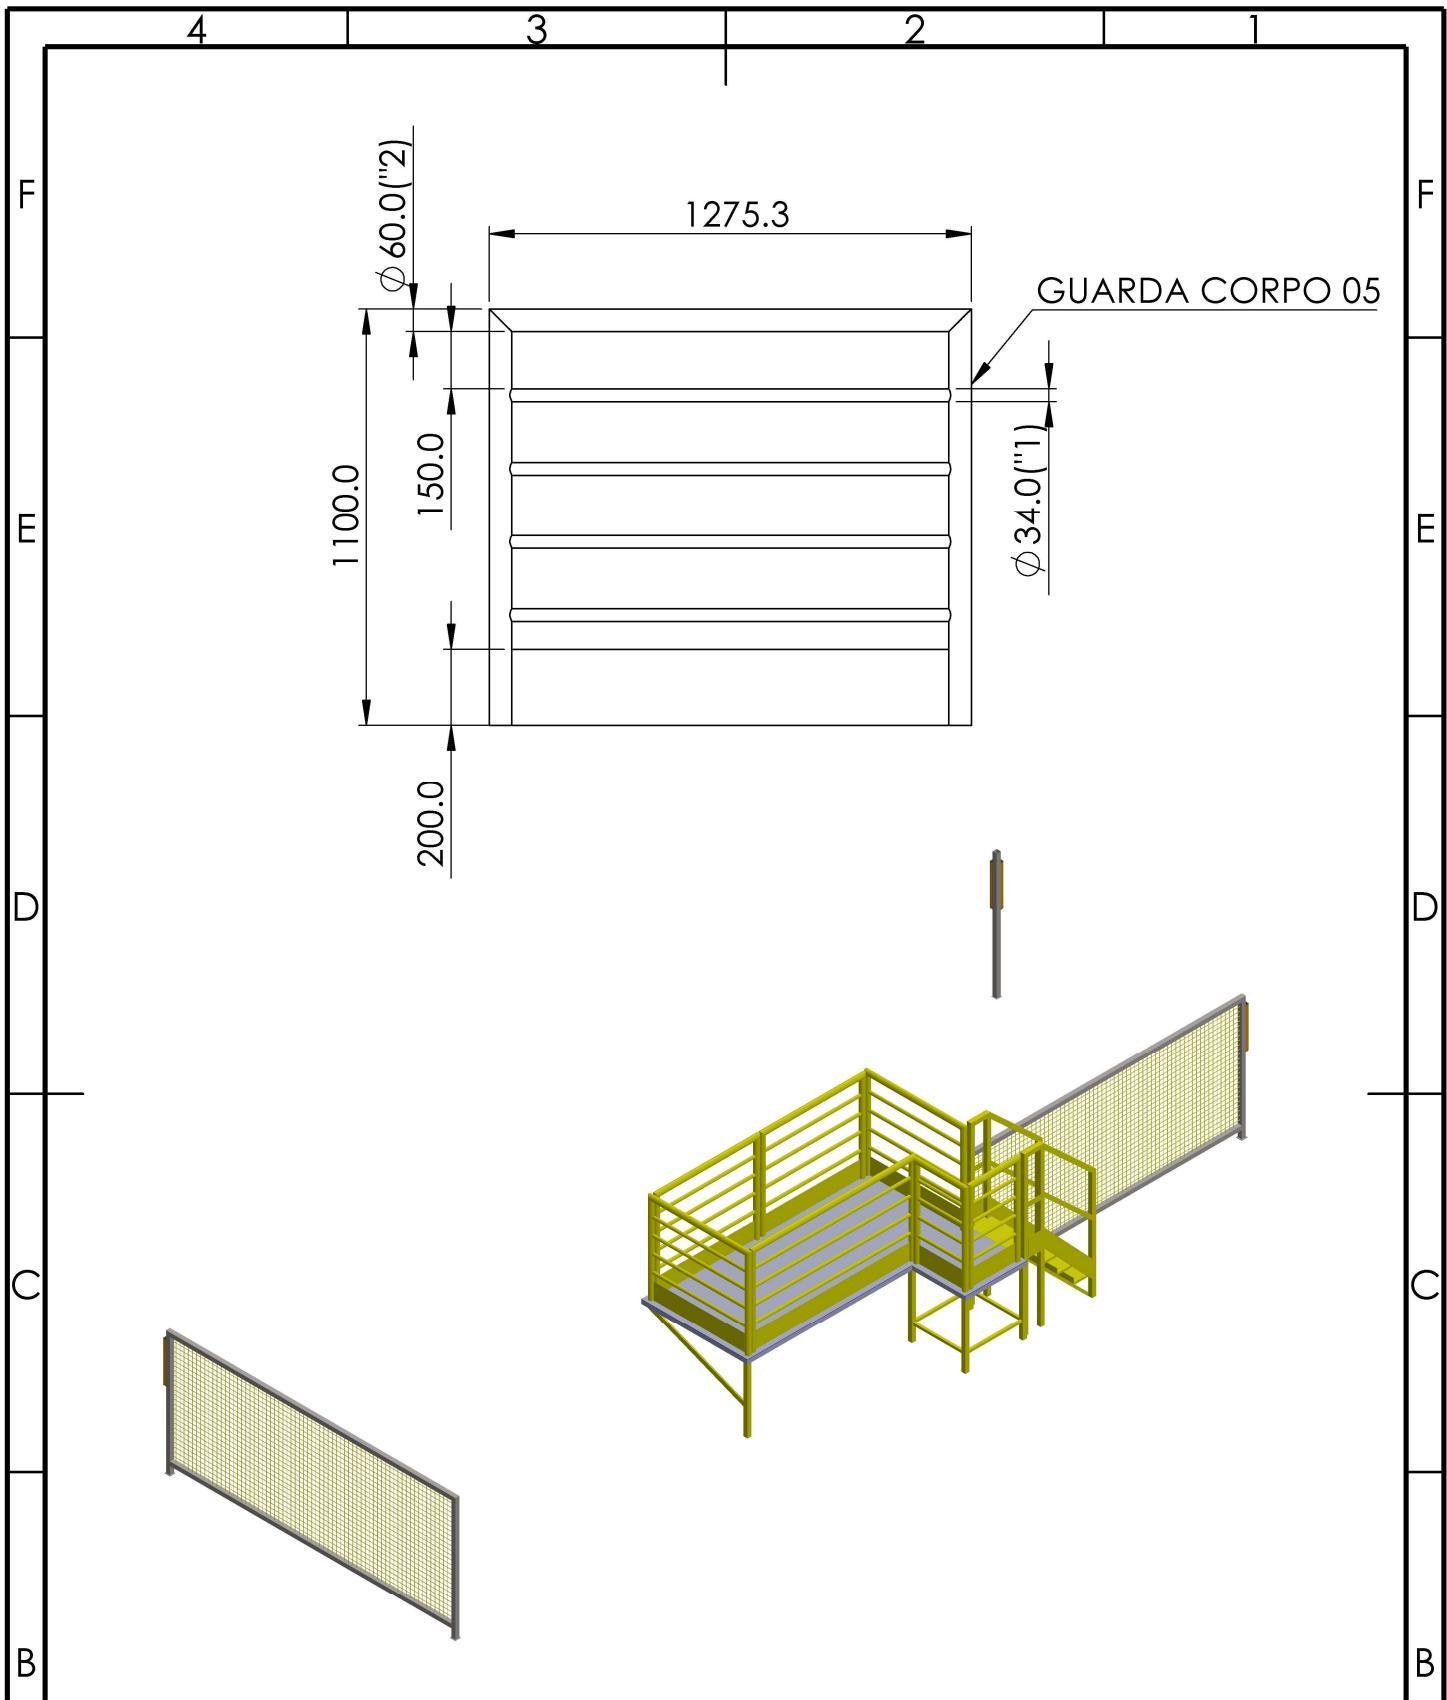

EMPRESA:

GRUPO NORMATEC

CLIENTE:

ISOESTE METALICA INDUSTRIA E COMERCIO LTDA.
CNPJ: 37.249.299/0001-22

DESCRIÇÃO:

CORTA FLECHA

FABRICANTE: N/C

APROVAÇÃO: MATHEUS FIALHO

DATA: JANEIRO/2024


TAG: CRF - 1300

ANO: N/C

NÚMERO: N/C

ESCALA: S/E

MATERIAL:

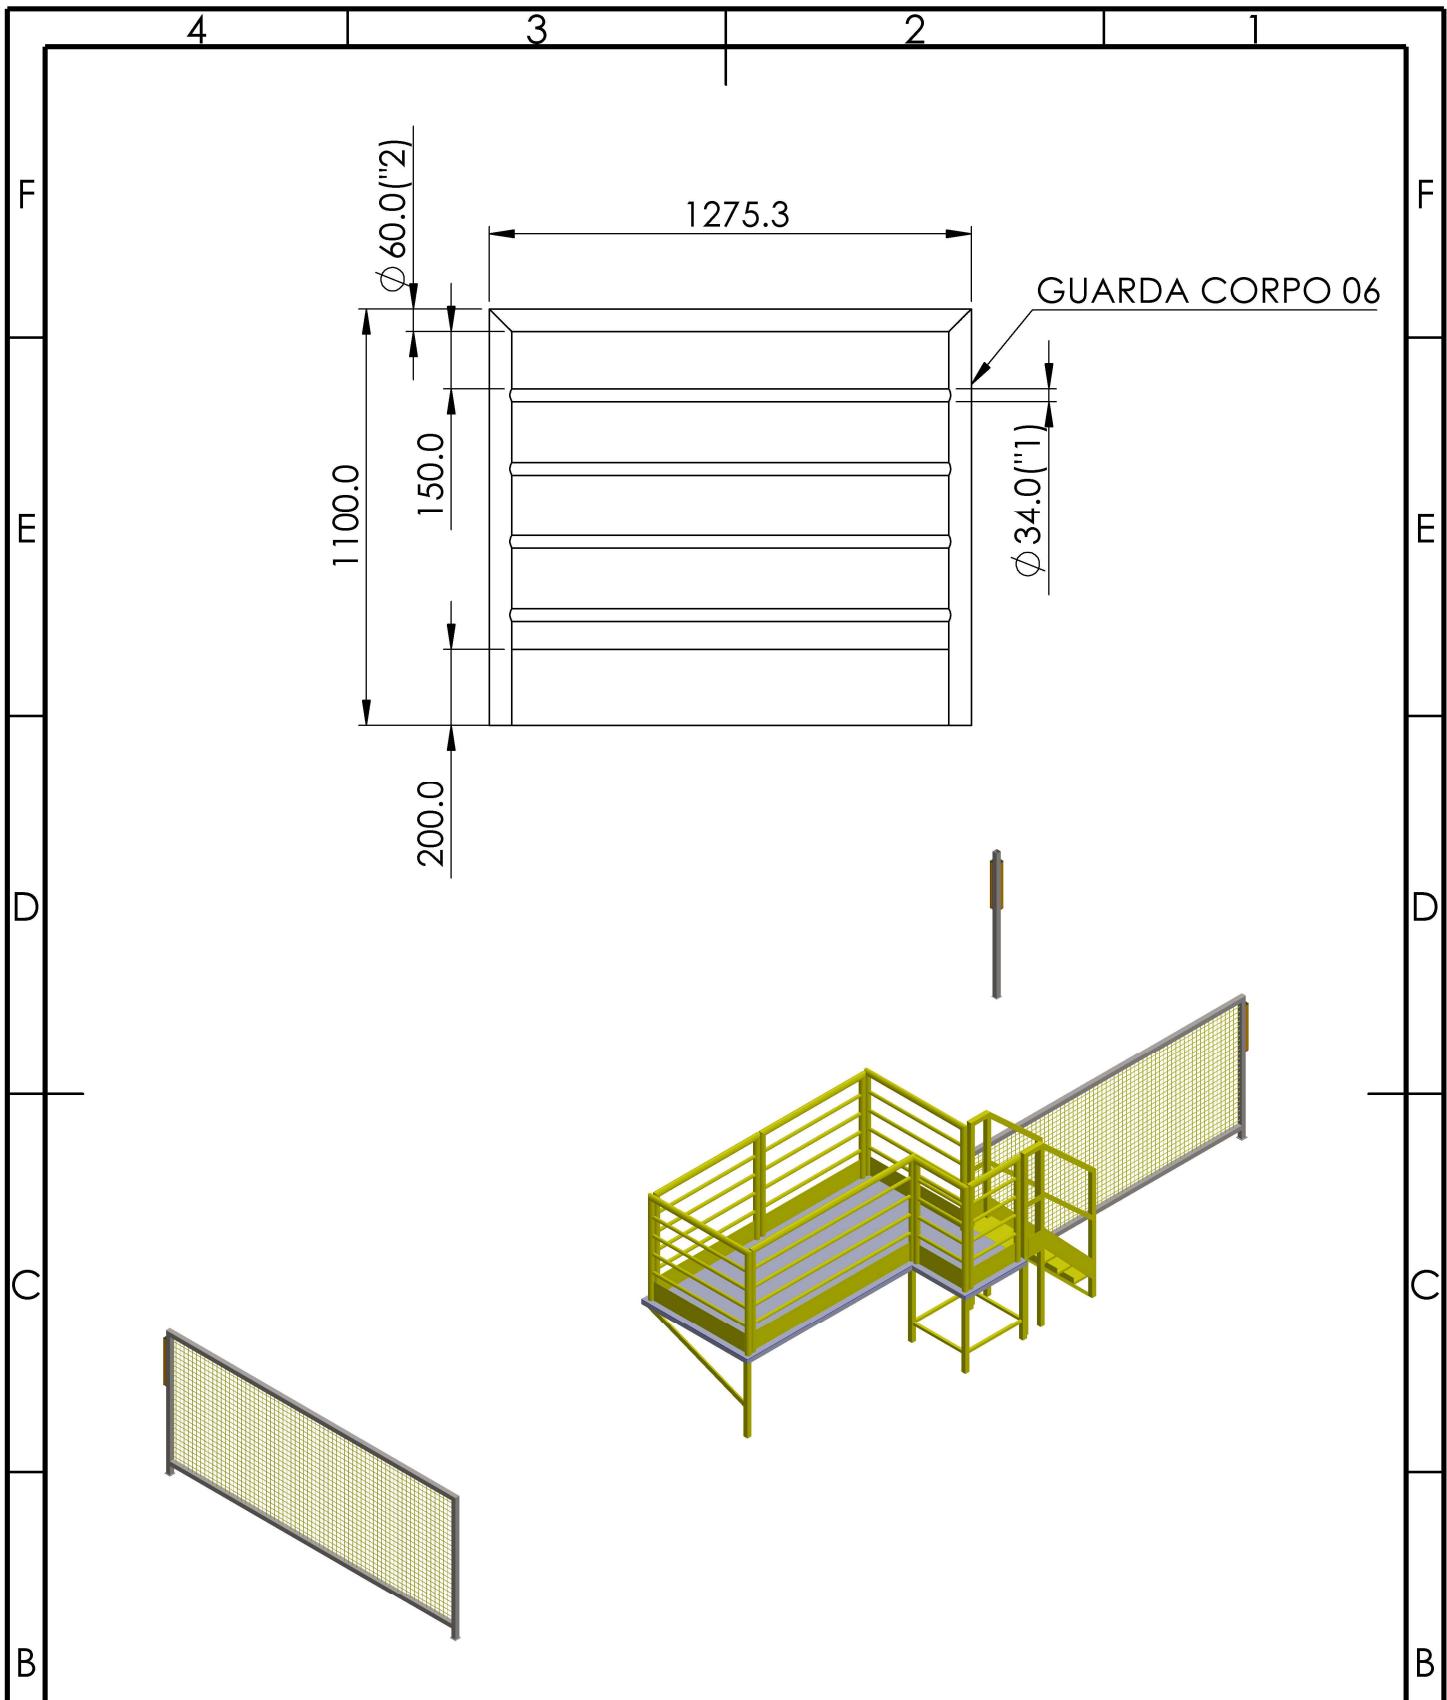

EMPRESA:

GRUPO NORMATEC

CLIENTE:

ISOESTE METALICA INDUSTRIA E COMERCIO LTDA.
CNPJ: 37.249.299/0001-22

DESCRIÇÃO:

CORTA FLECHA

FABRICANTE: N/C

APROVAÇÃO: MATHEUS FIALHO

DATA: JANEIRO/2024


TAG: CRF - 1300

ANO: N/C

NÚMERO: N/C

ESCALA: S/E

MATERIAL:

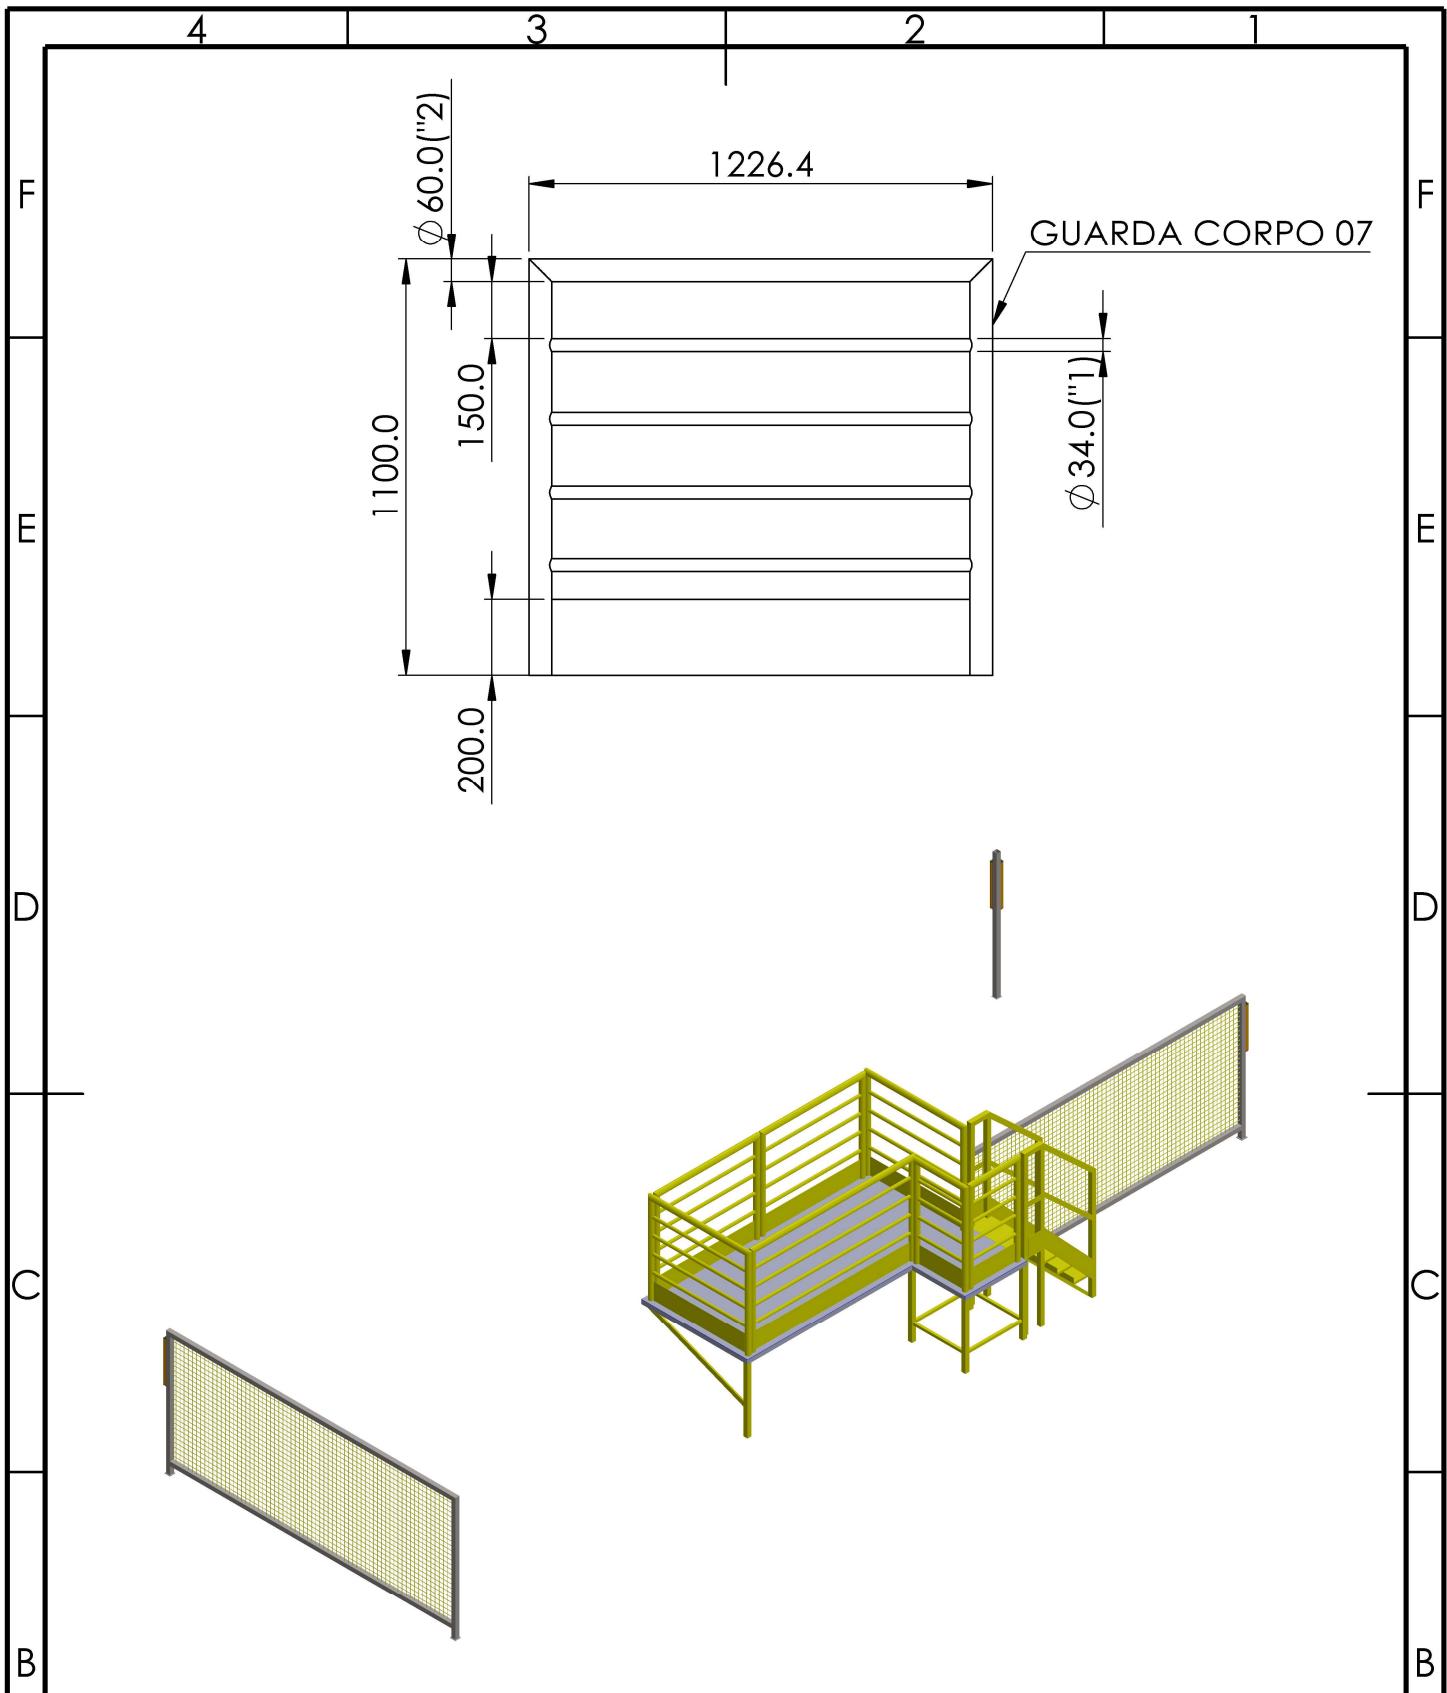

EMPRESA:

GRUPO NORMATEC

CLIENTE:

ISOESTE METALICA INDUSTRIA E COMERCIO LTDA.
CNPJ: 37.249.299/0001-22

DESCRIÇÃO:

CORTA FLECHA

FABRICANTE: N/C

APROVAÇÃO: MATHEUS FIALHO

DATA: JANEIRO/2024


TAG: CRF - 1300

ANO: N/C

NÚMERO: N/C

ESCALA: S/E

MATERIAL:

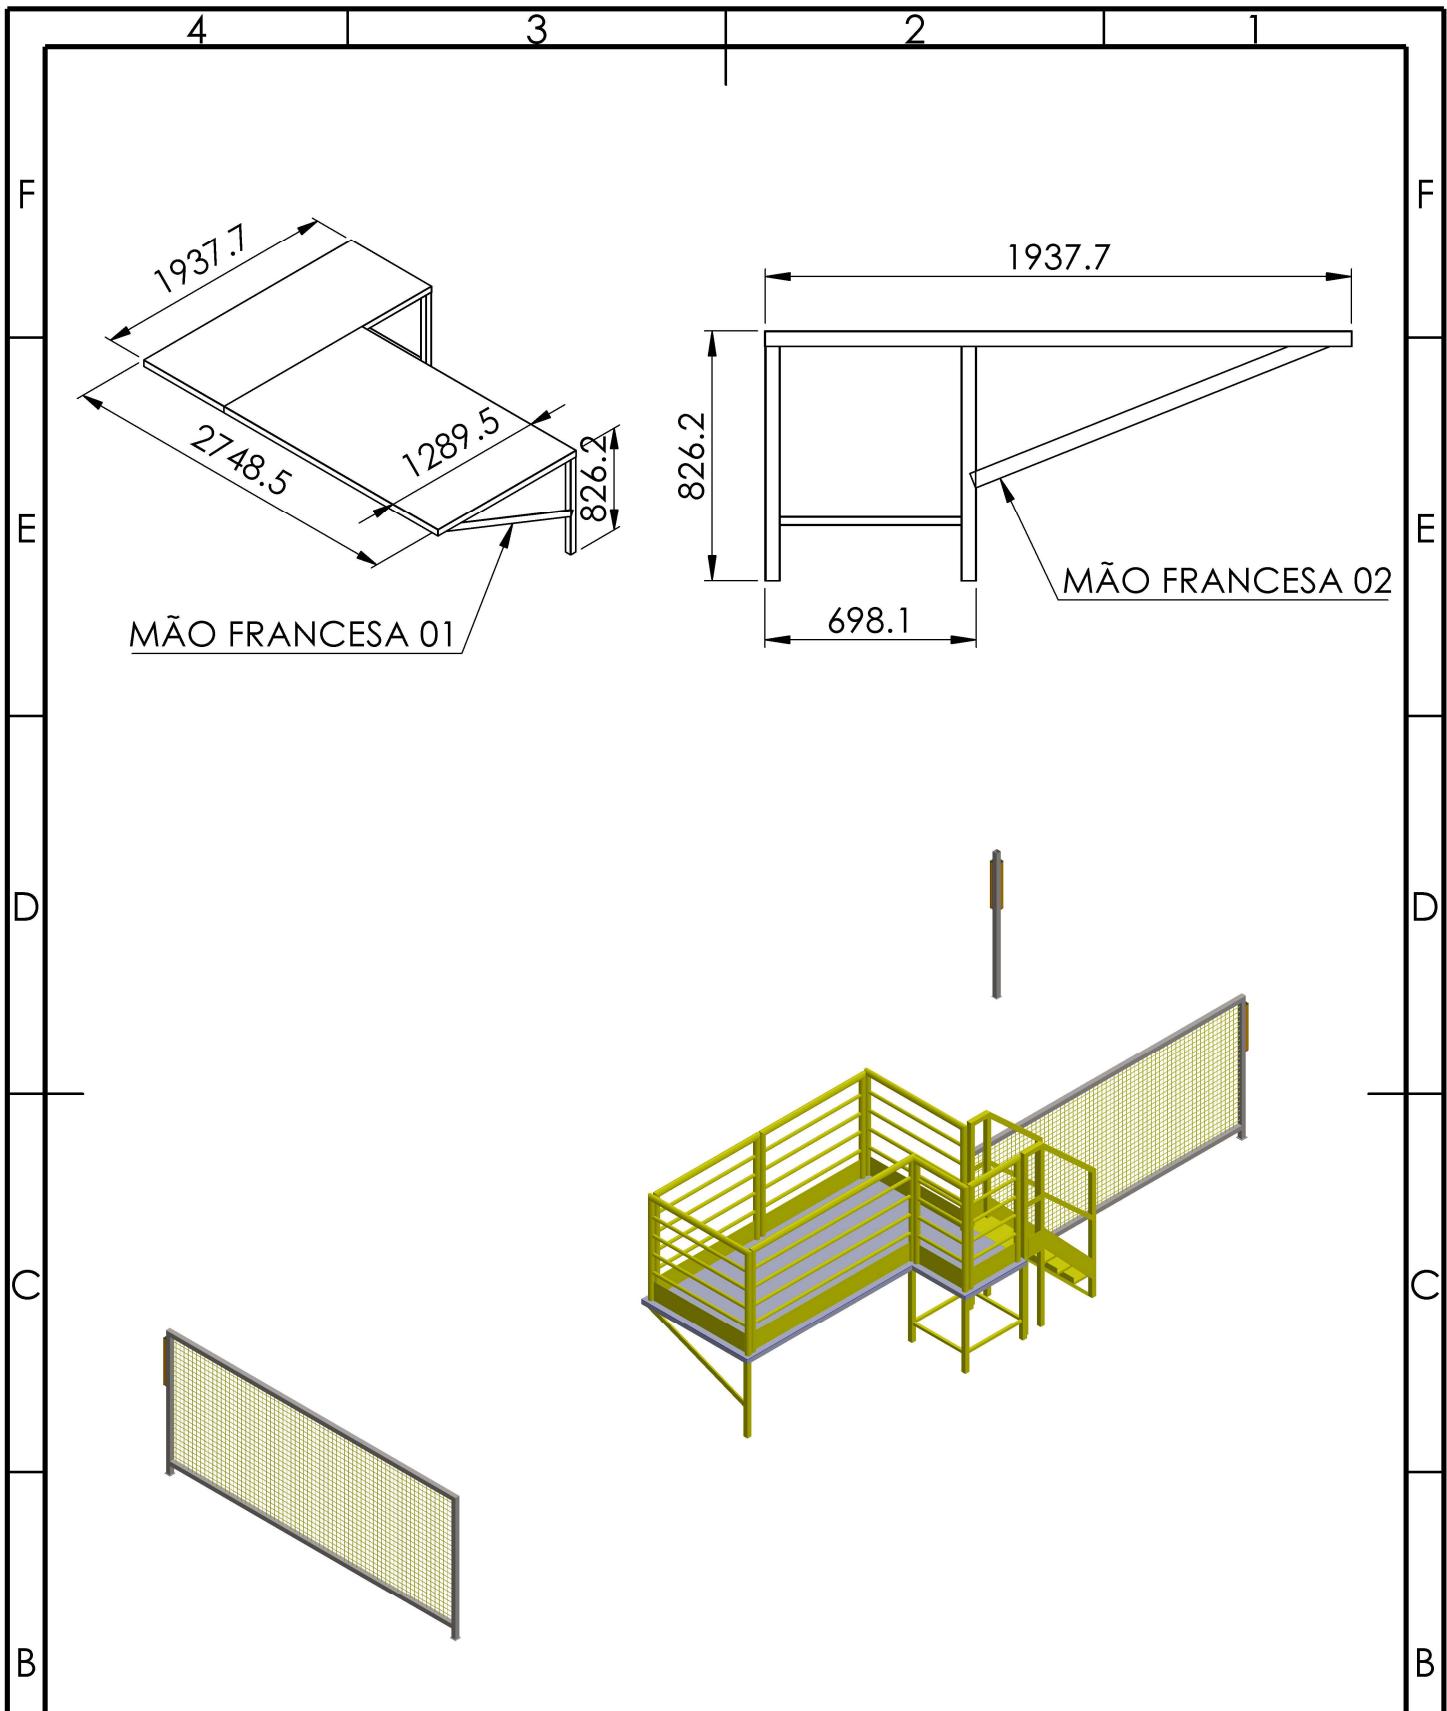

EMPRESA:

GRUPO NORMATEC

CLIENTE:

ISOESTE METALICA INDUSTRIA E COMERCIO LTDA.
CNPJ: 37.249.299/0001-22

DESCRIÇÃO:

CORTA FLECHA

FABRICANTE: N/C

APROVAÇÃO: MATHEUS FIALHO

DATA: JANEIRO/2024

TAG: CRF - 1300

ANO: N/C

NÚMERO: N/C

ESCALA: S/E

MATERIAL: