

4 3 2 1

F F


E E

D D

C C

B B

A A

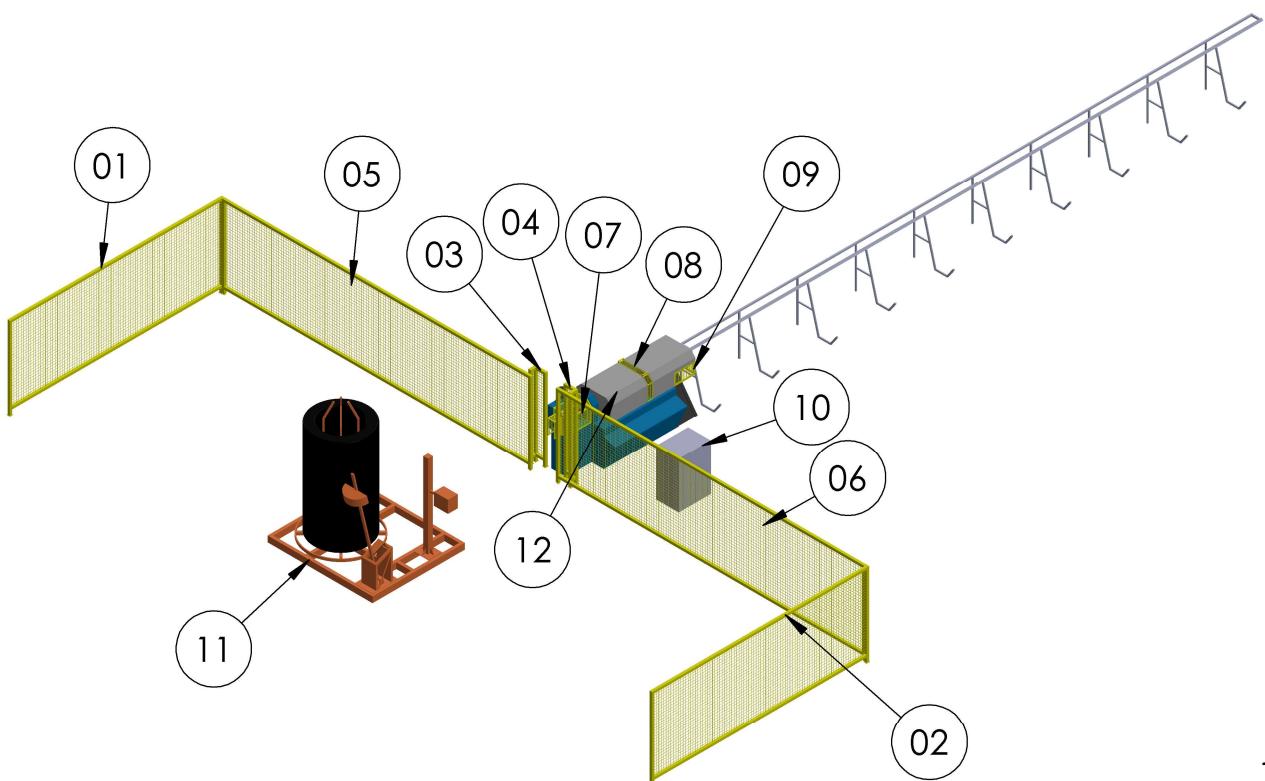


ITENS	NOMES
01	PROTEÇÃO FIXA 01
02	PROTEÇÃO FIXA 02
03	PROTEÇÃO FIXA 03
04	PROTEÇÃO FIXA 04
05	PROTEÇÃO MÓVEL COM SENSOR DE MOVIMENTO 01
06	PROTEÇÃO MÓVEL COM SENSOR DE MOVIMENTO 02
07	PROTEÇÃO MÓVEL ENTRADA DA MÁQUINA
08	PROTEÇÃO MÓVEL NA MÁQUINA
09	PROTEÇÃO MÓVEL SAÍDA DA MÁQUINA
10	PAINEL DE COMANDO
11	BOBINADORA
12	ENDIREITADEIRA


**EMPRESA:** GRUPO NORMATEC**CLIENTE:** ISOESTE METALICA INDUSTRIA E COMERCIO LTDA.  
CNPJ: 37.249.299/0001-22**DESCRIÇÃO:** ENDIREITADEIRA


FABRICANTE: N/C	APROVAÇÃO: MATEUS FIALHO	DATA: FEVEREIRO/2024	
TAG: END-ISO-001	ANO: N/C	NÚMERO: N	ESCALA: 1 : 110

**MATERIAL:**

4 3 2 1

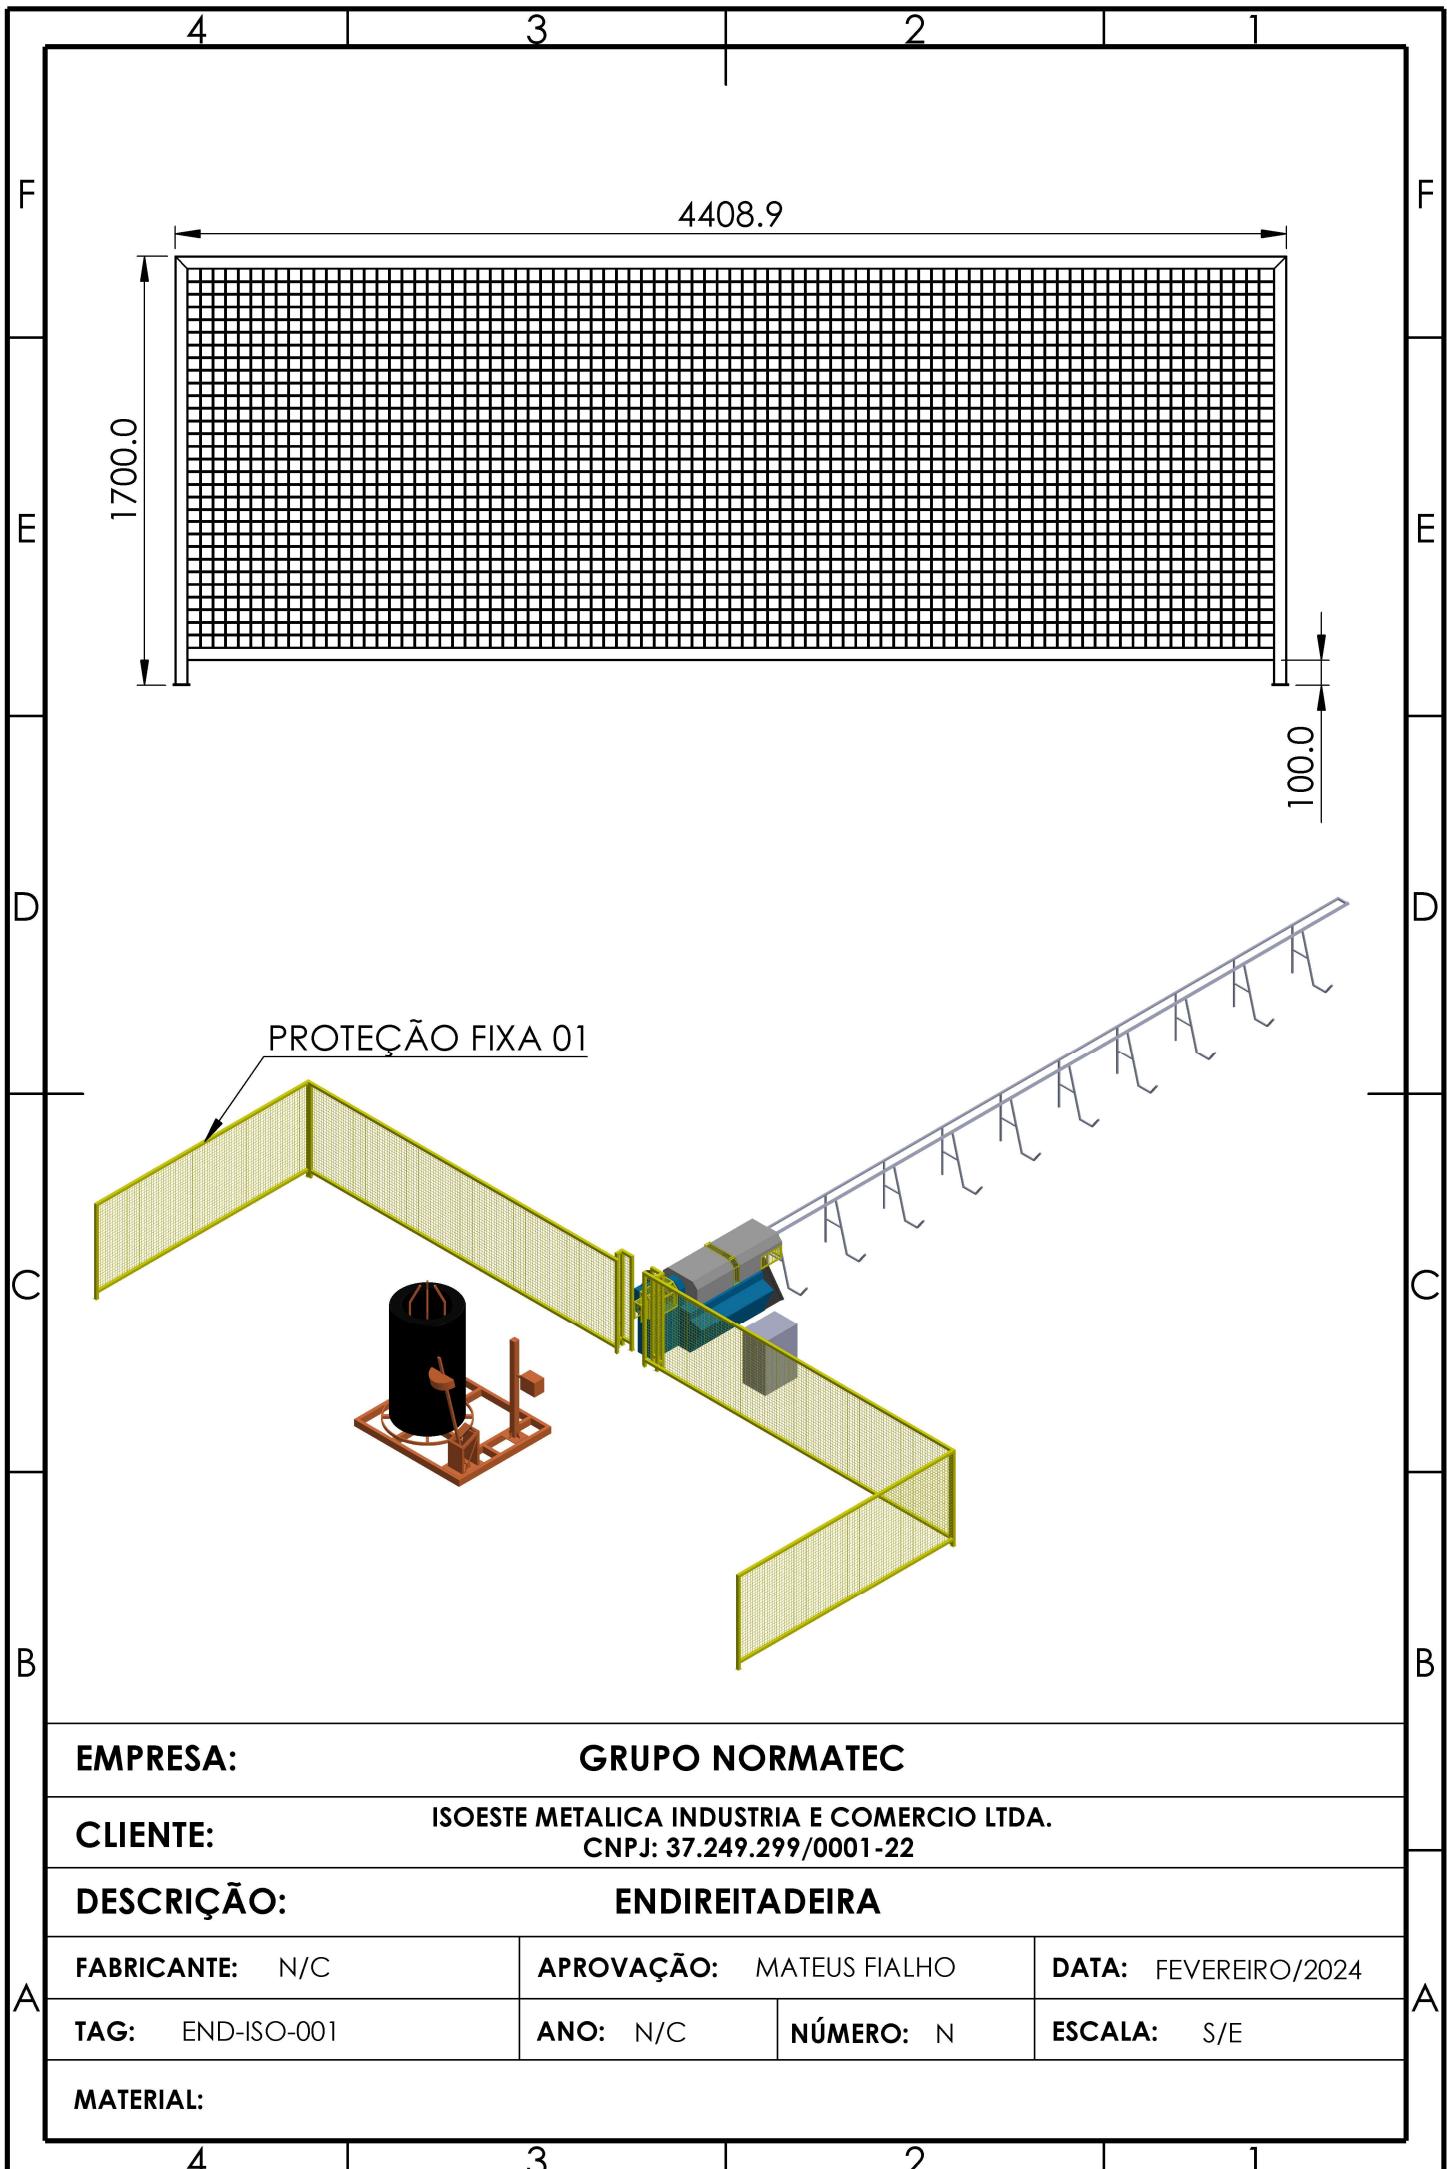

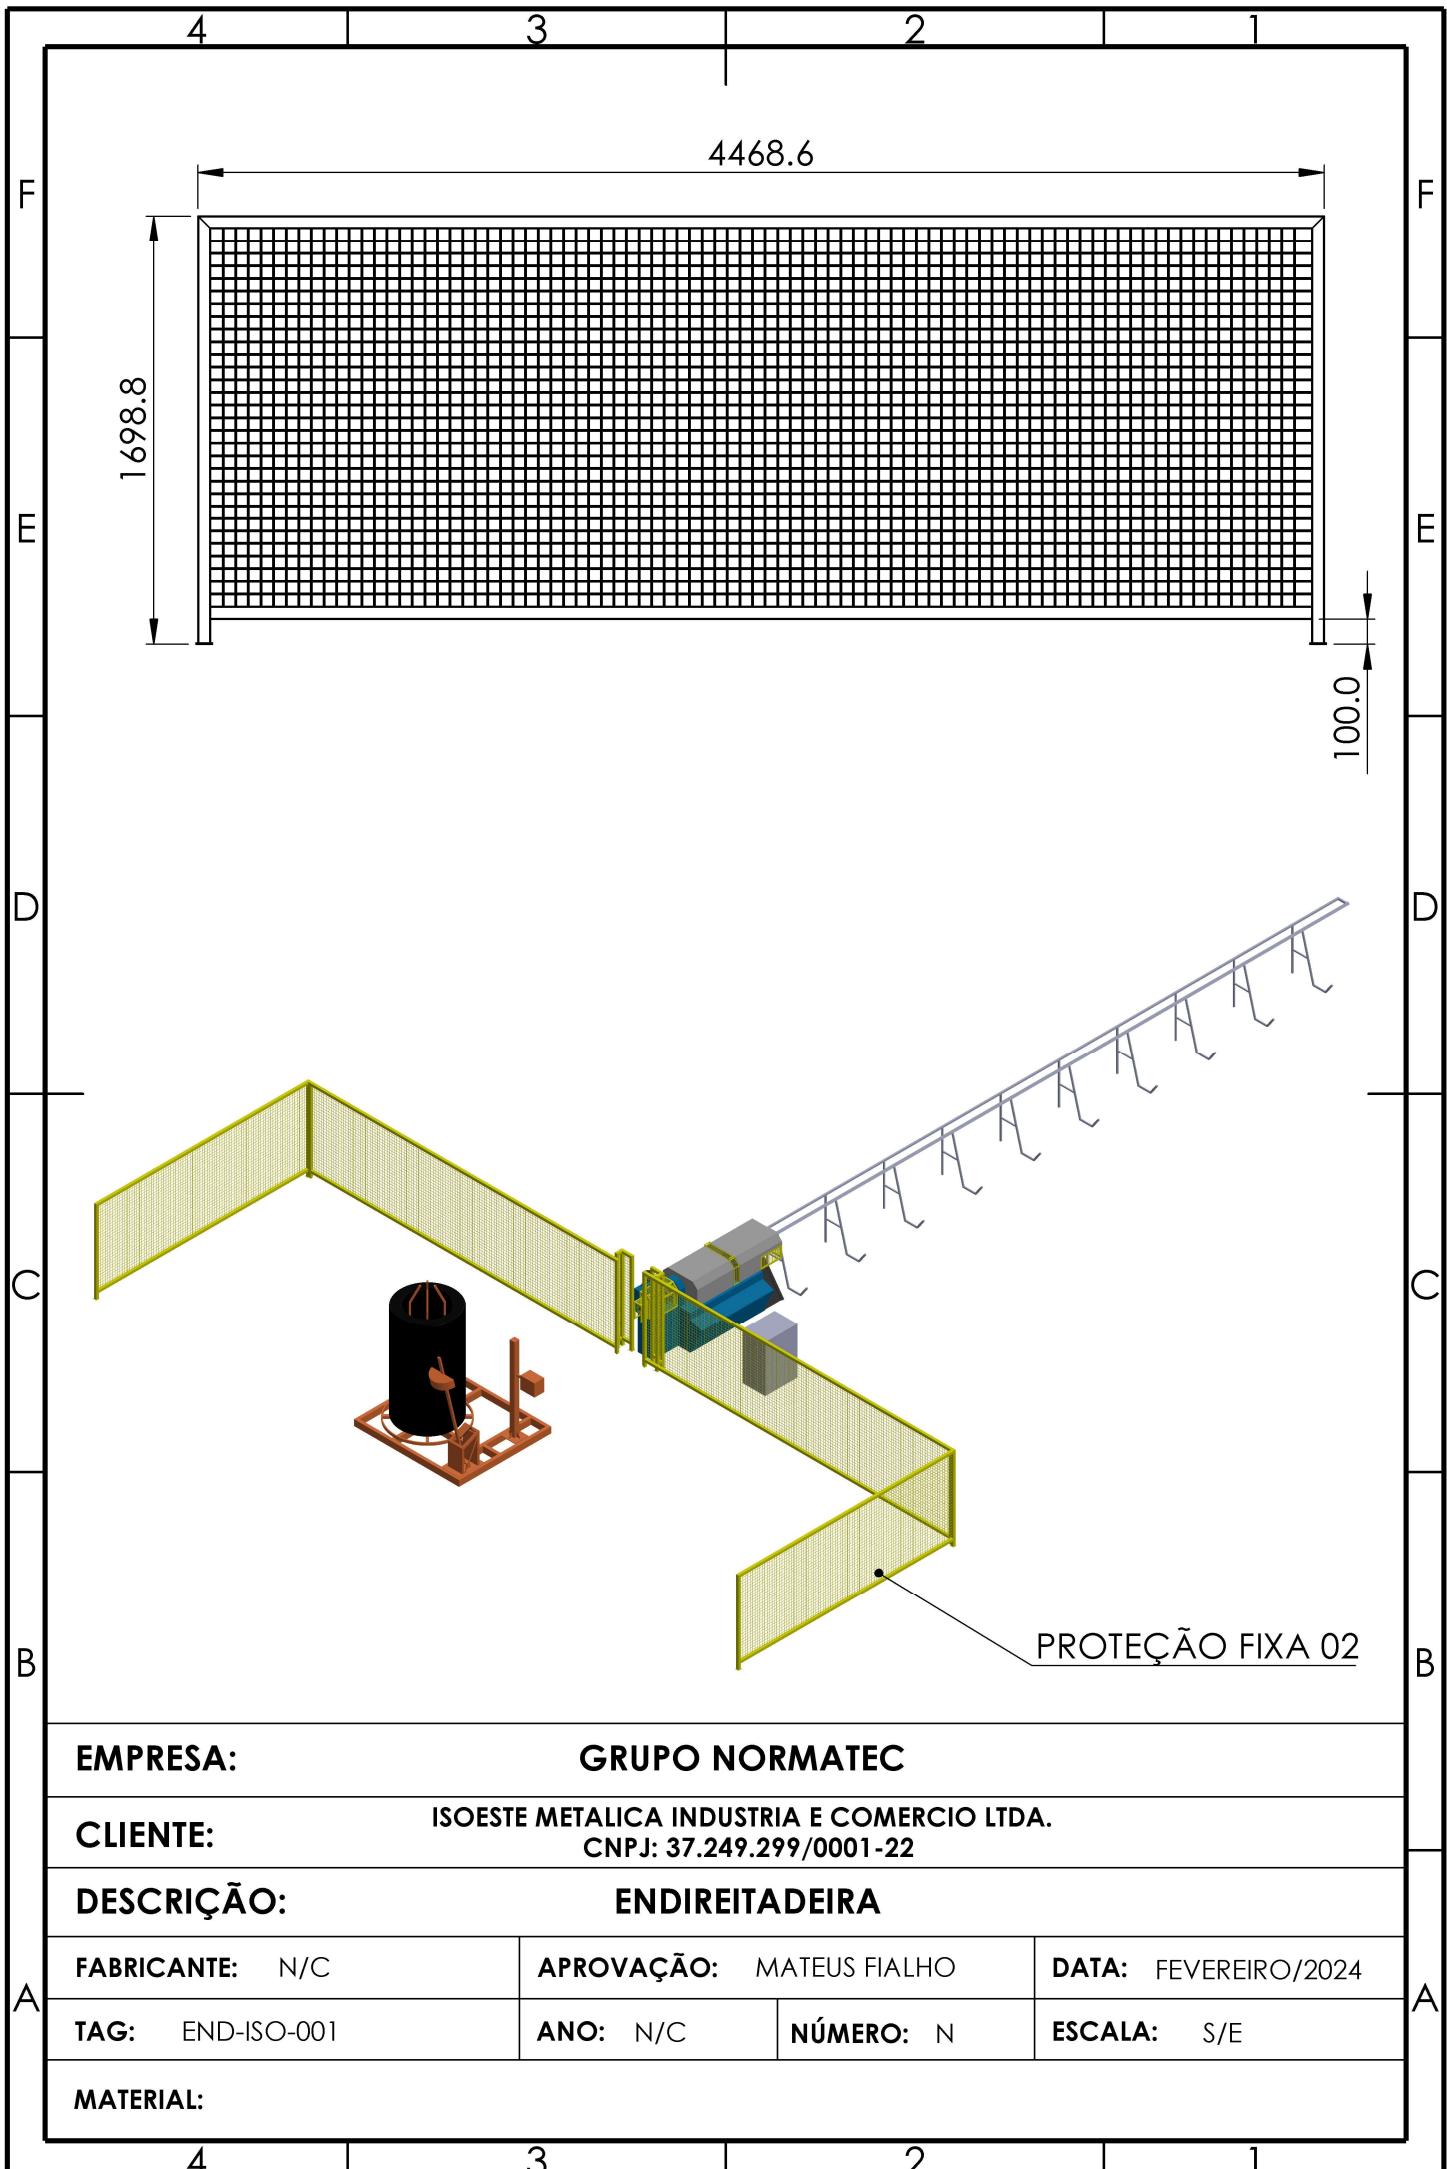

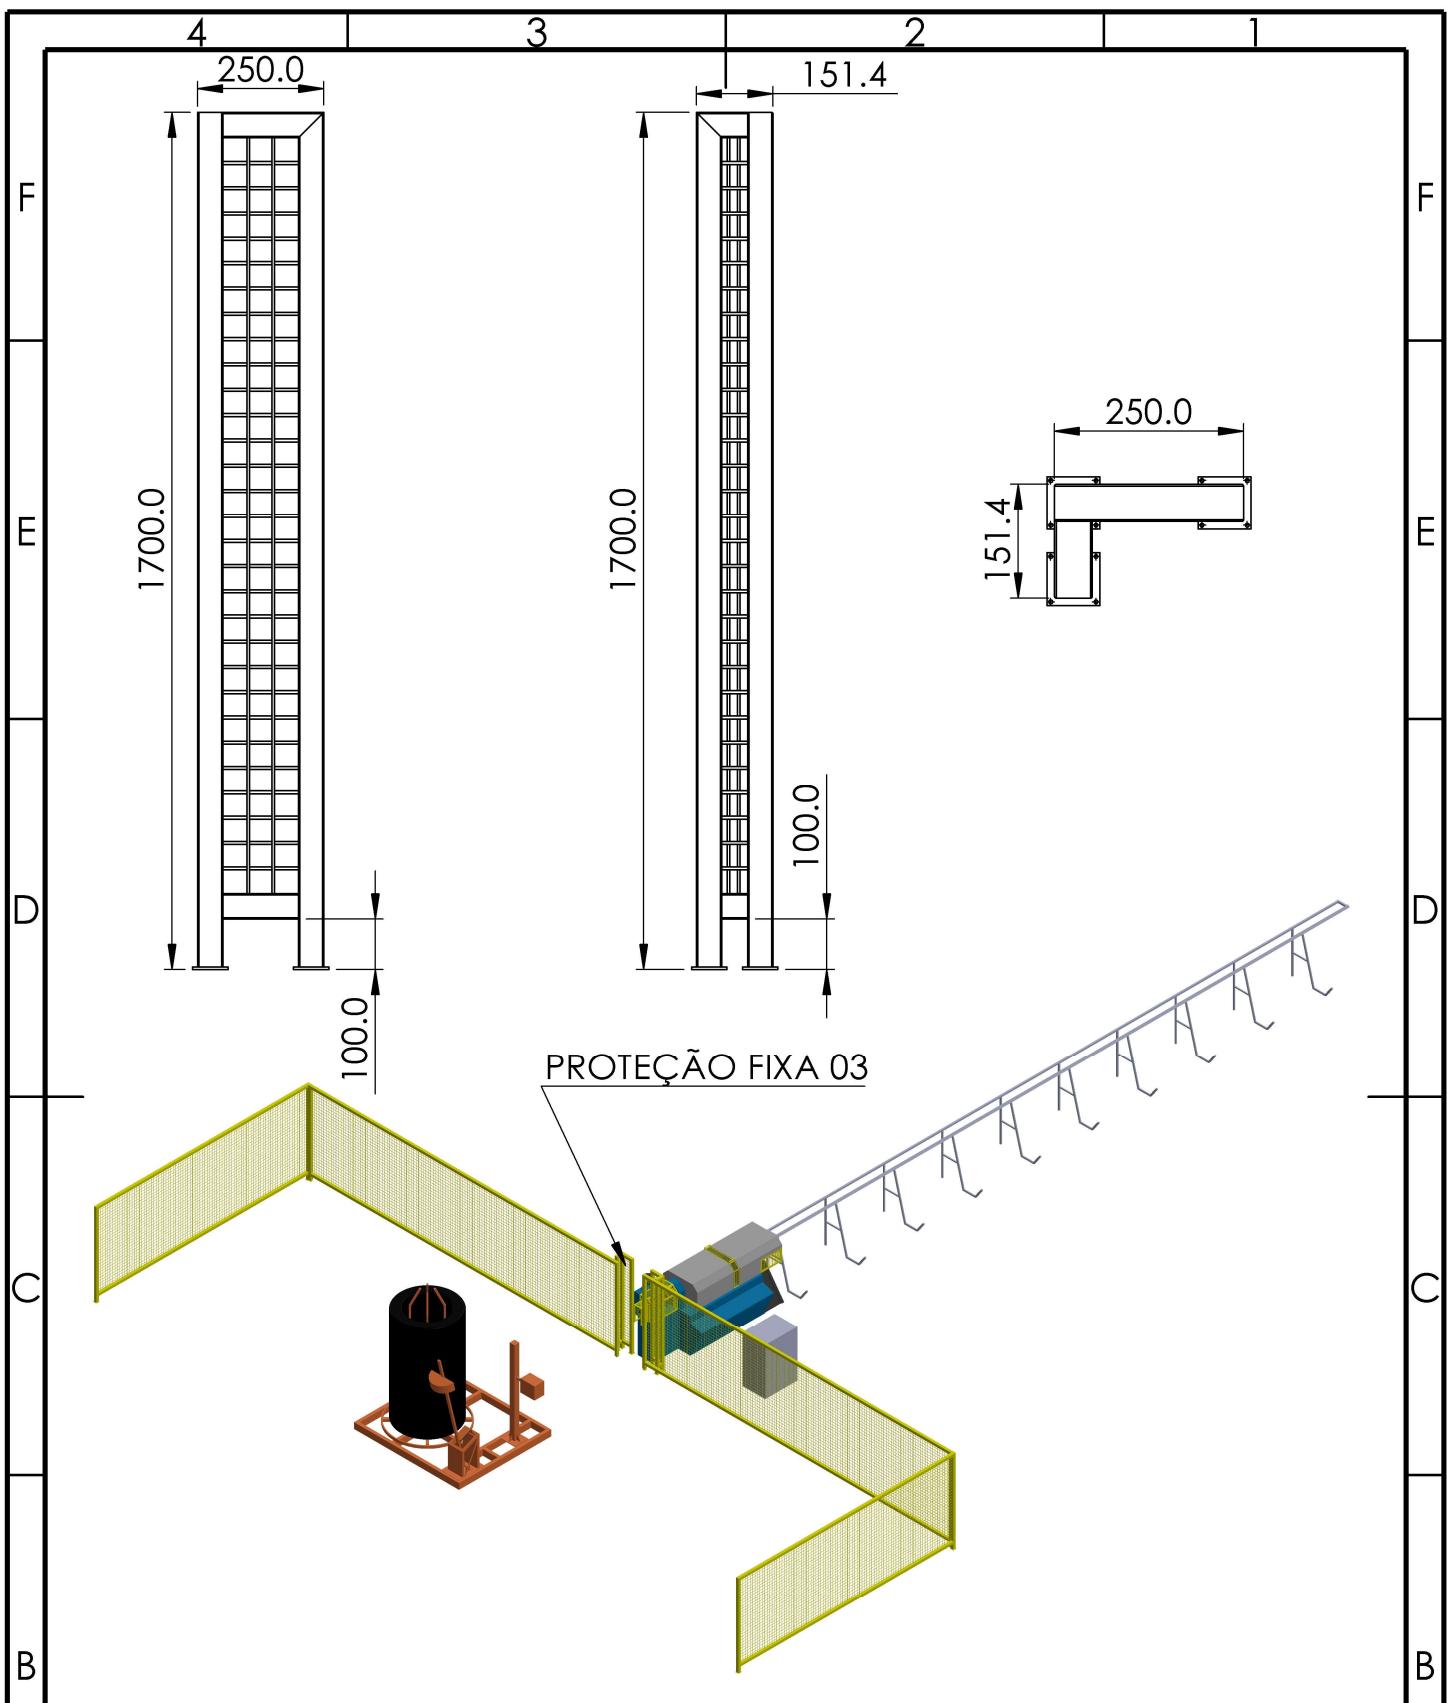

**EMPRESA:**

**GRUPO NORMATEC**

**CLIENTE:**

**ISOESTE METALICA INDUSTRIA E COMERCIO LTDA.**  
**CNPJ: 37.249.299/0001-22**

**DESCRIÇÃO:**

**ENDIREITADEIRA**

**FABRICANTE:** N/C

**APROVAÇÃO:** MATEUS FIALHO

**DATA:** FEVEREIRO/2024

**TAG:** END-ISO-001

**ANO:** N/C

**NÚMERO:** N

**ESCALA:** S/E


**MATERIAL:**

4

3

2

1

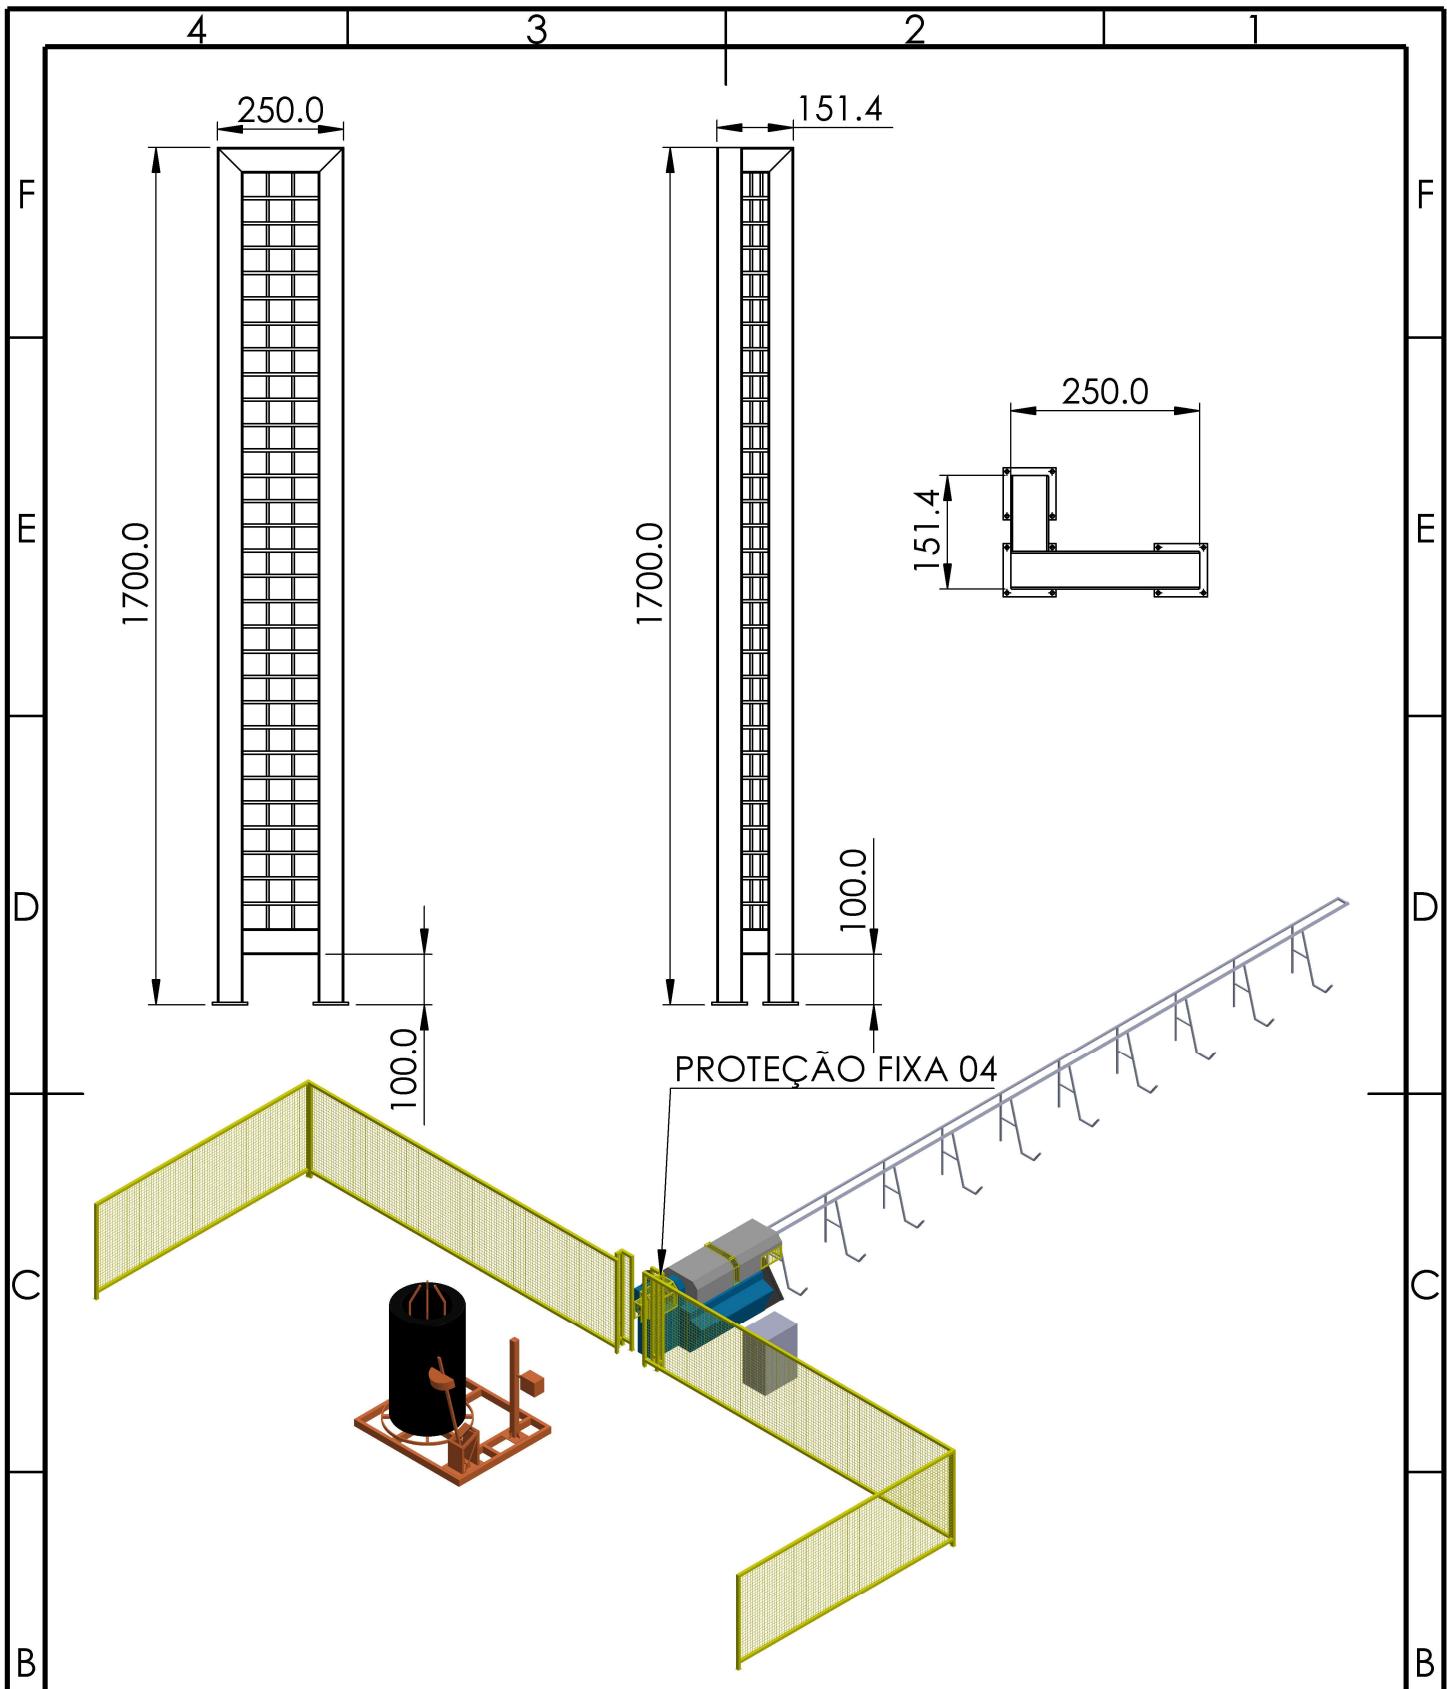

**EMPRESA:**

**GRUPO NORMATEC**

**CLIENTE:**

ISOESTE METALICA INDUSTRIA E COMERCIO LTDA.  
CNPJ: 37.249.299/0001-22

**DESCRIÇÃO:**

**ENDIREITADEIRA**

**FABRICANTE:** N/C

**APROVAÇÃO:** MATEUS FIALHO

**DATA:** FEVEREIRO/2024

**TAG:** END-ISO-001

**ANO:** N/C

**NÚMERO:** N

**ESCALA:** S/E


**MATERIAL:**

4

3

2

1

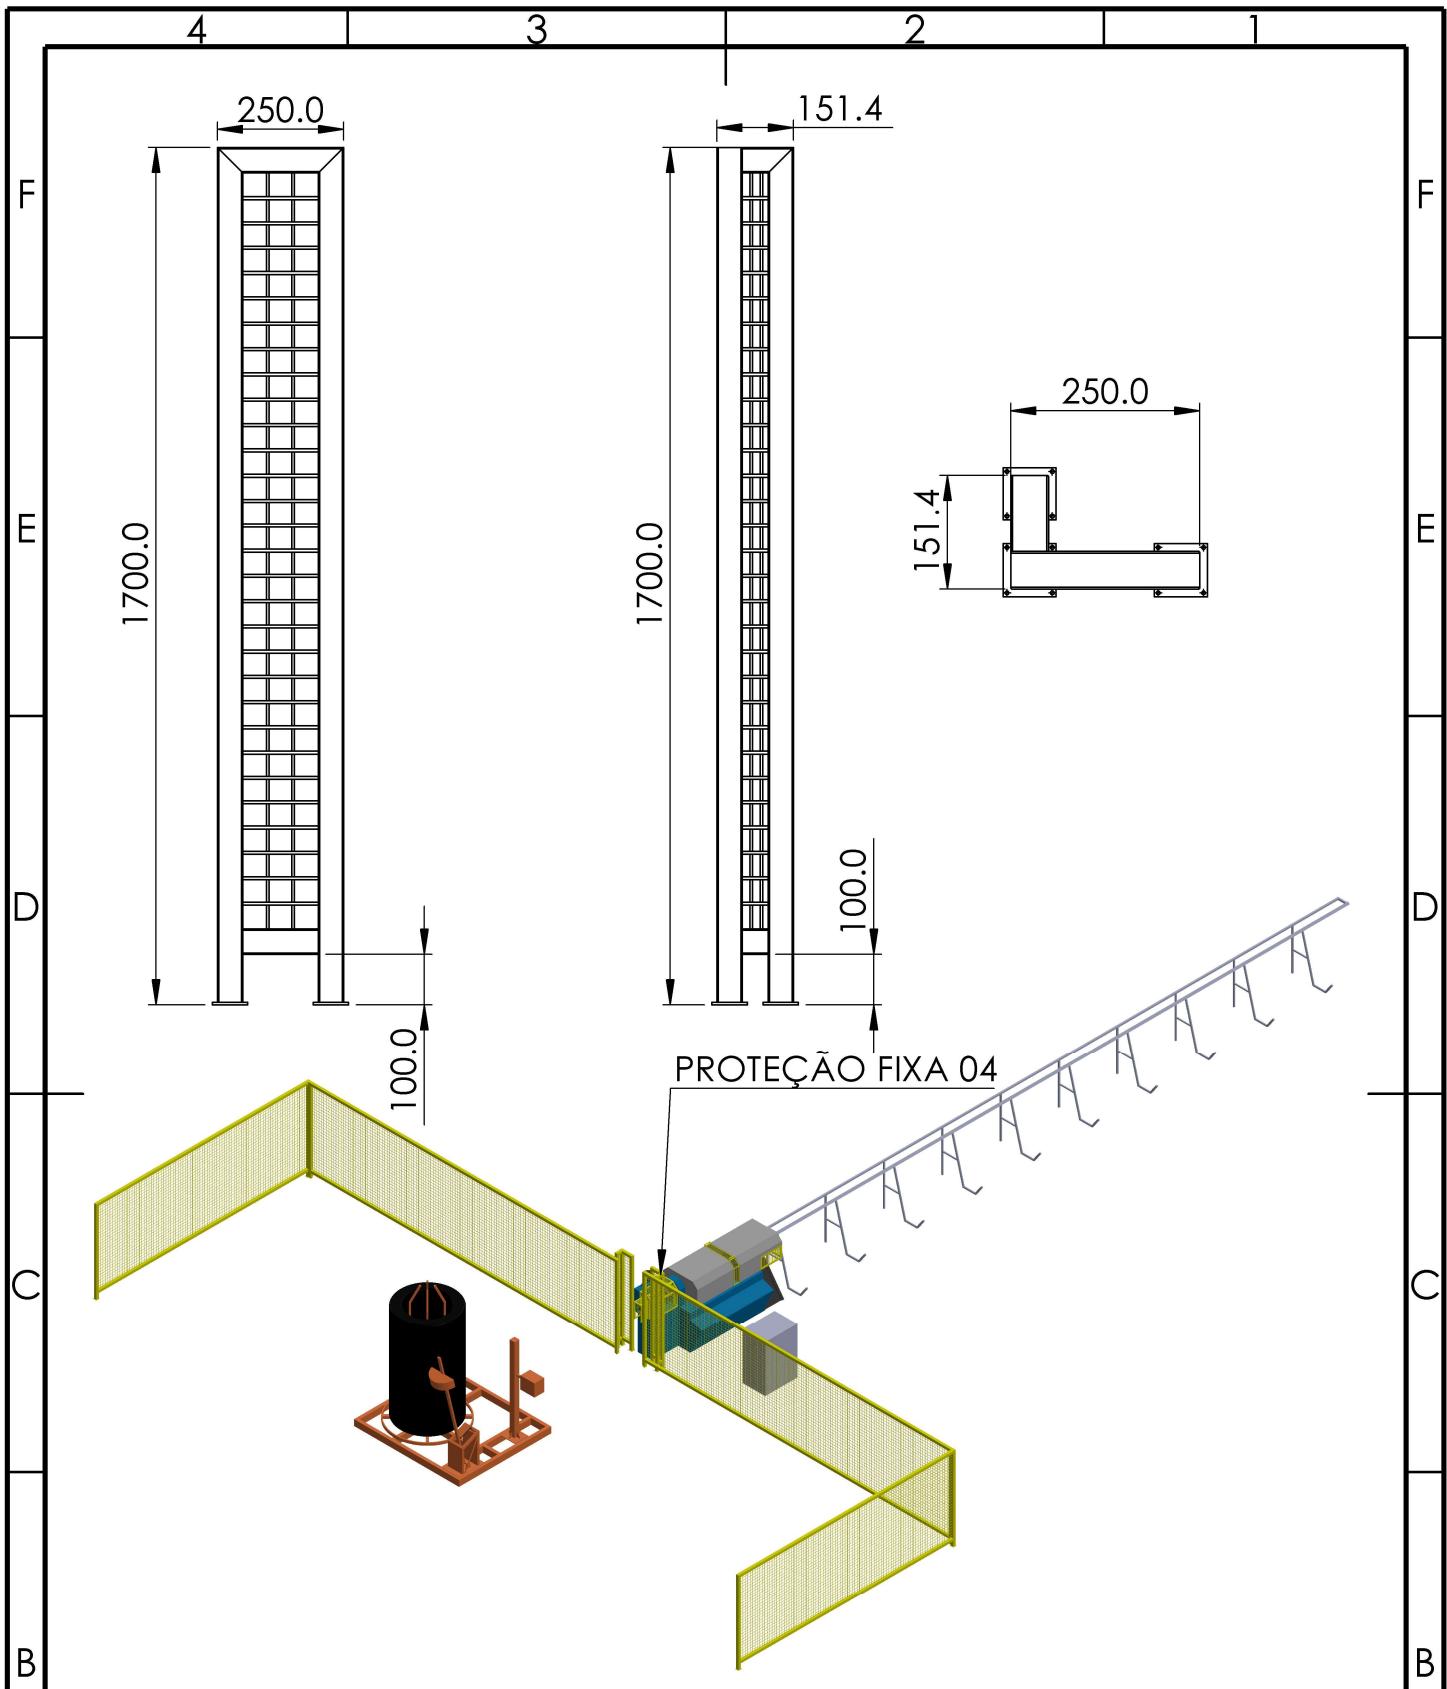

**EMPRESA:**

**GRUPO NORMATEC**

**CLIENTE:**

**ISOESTE METALICA INDUSTRIA E COMERCIO LTDA.**  
**CNPJ: 37.249.299/0001-22**

**DESCRIÇÃO:**

**ENDIREITADEIRA**

**FABRICANTE:** N/C

**APROVAÇÃO:** MATEUS FIALHO

**DATA:** FEVEREIRO/2024

**TAG:** END-ISO-001

**ANO:** N/C

**NÚMERO:** N

**ESCALA:** S/E


**MATERIAL:**

4

3

2

1

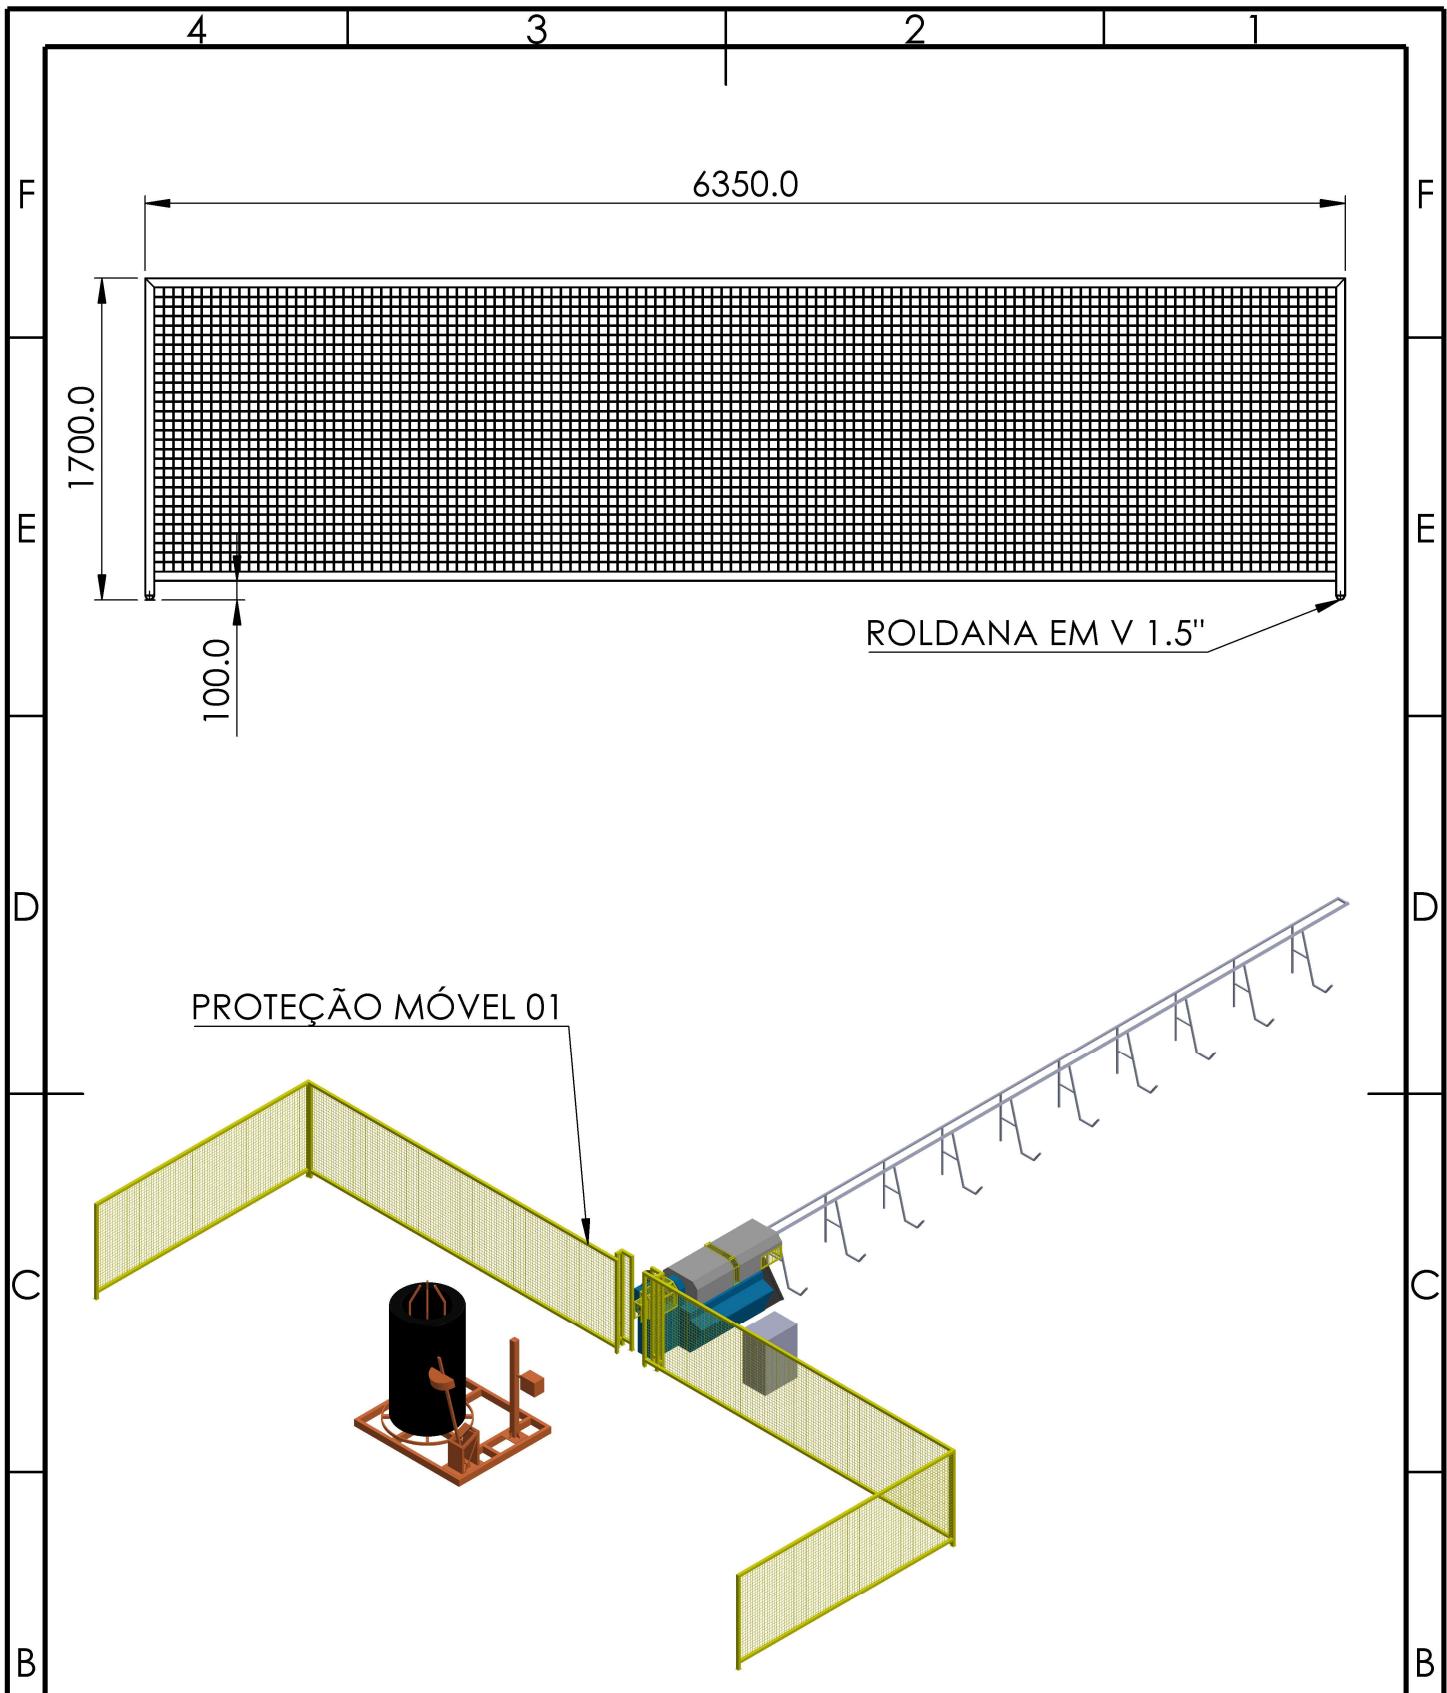

**EMPRESA:**

**GRUPO NORMATEC**

**CLIENTE:**

**ISOESTE METALICA INDUSTRIA E COMERCIO LTDA.**  
CNPJ: 37.249.299/0001-22

**DESCRIÇÃO:**

**ENDIREITADEIRA**

**FABRICANTE:** N/C

**APROVAÇÃO:** MATEUS FIALHO

**DATA:** FEVEREIRO/2024

**TAG:** END-ISO-001

**ANO:** N/C

**NÚMERO:** N

**ESCALA:** S/E


**MATERIAL:**


4

3


2

1

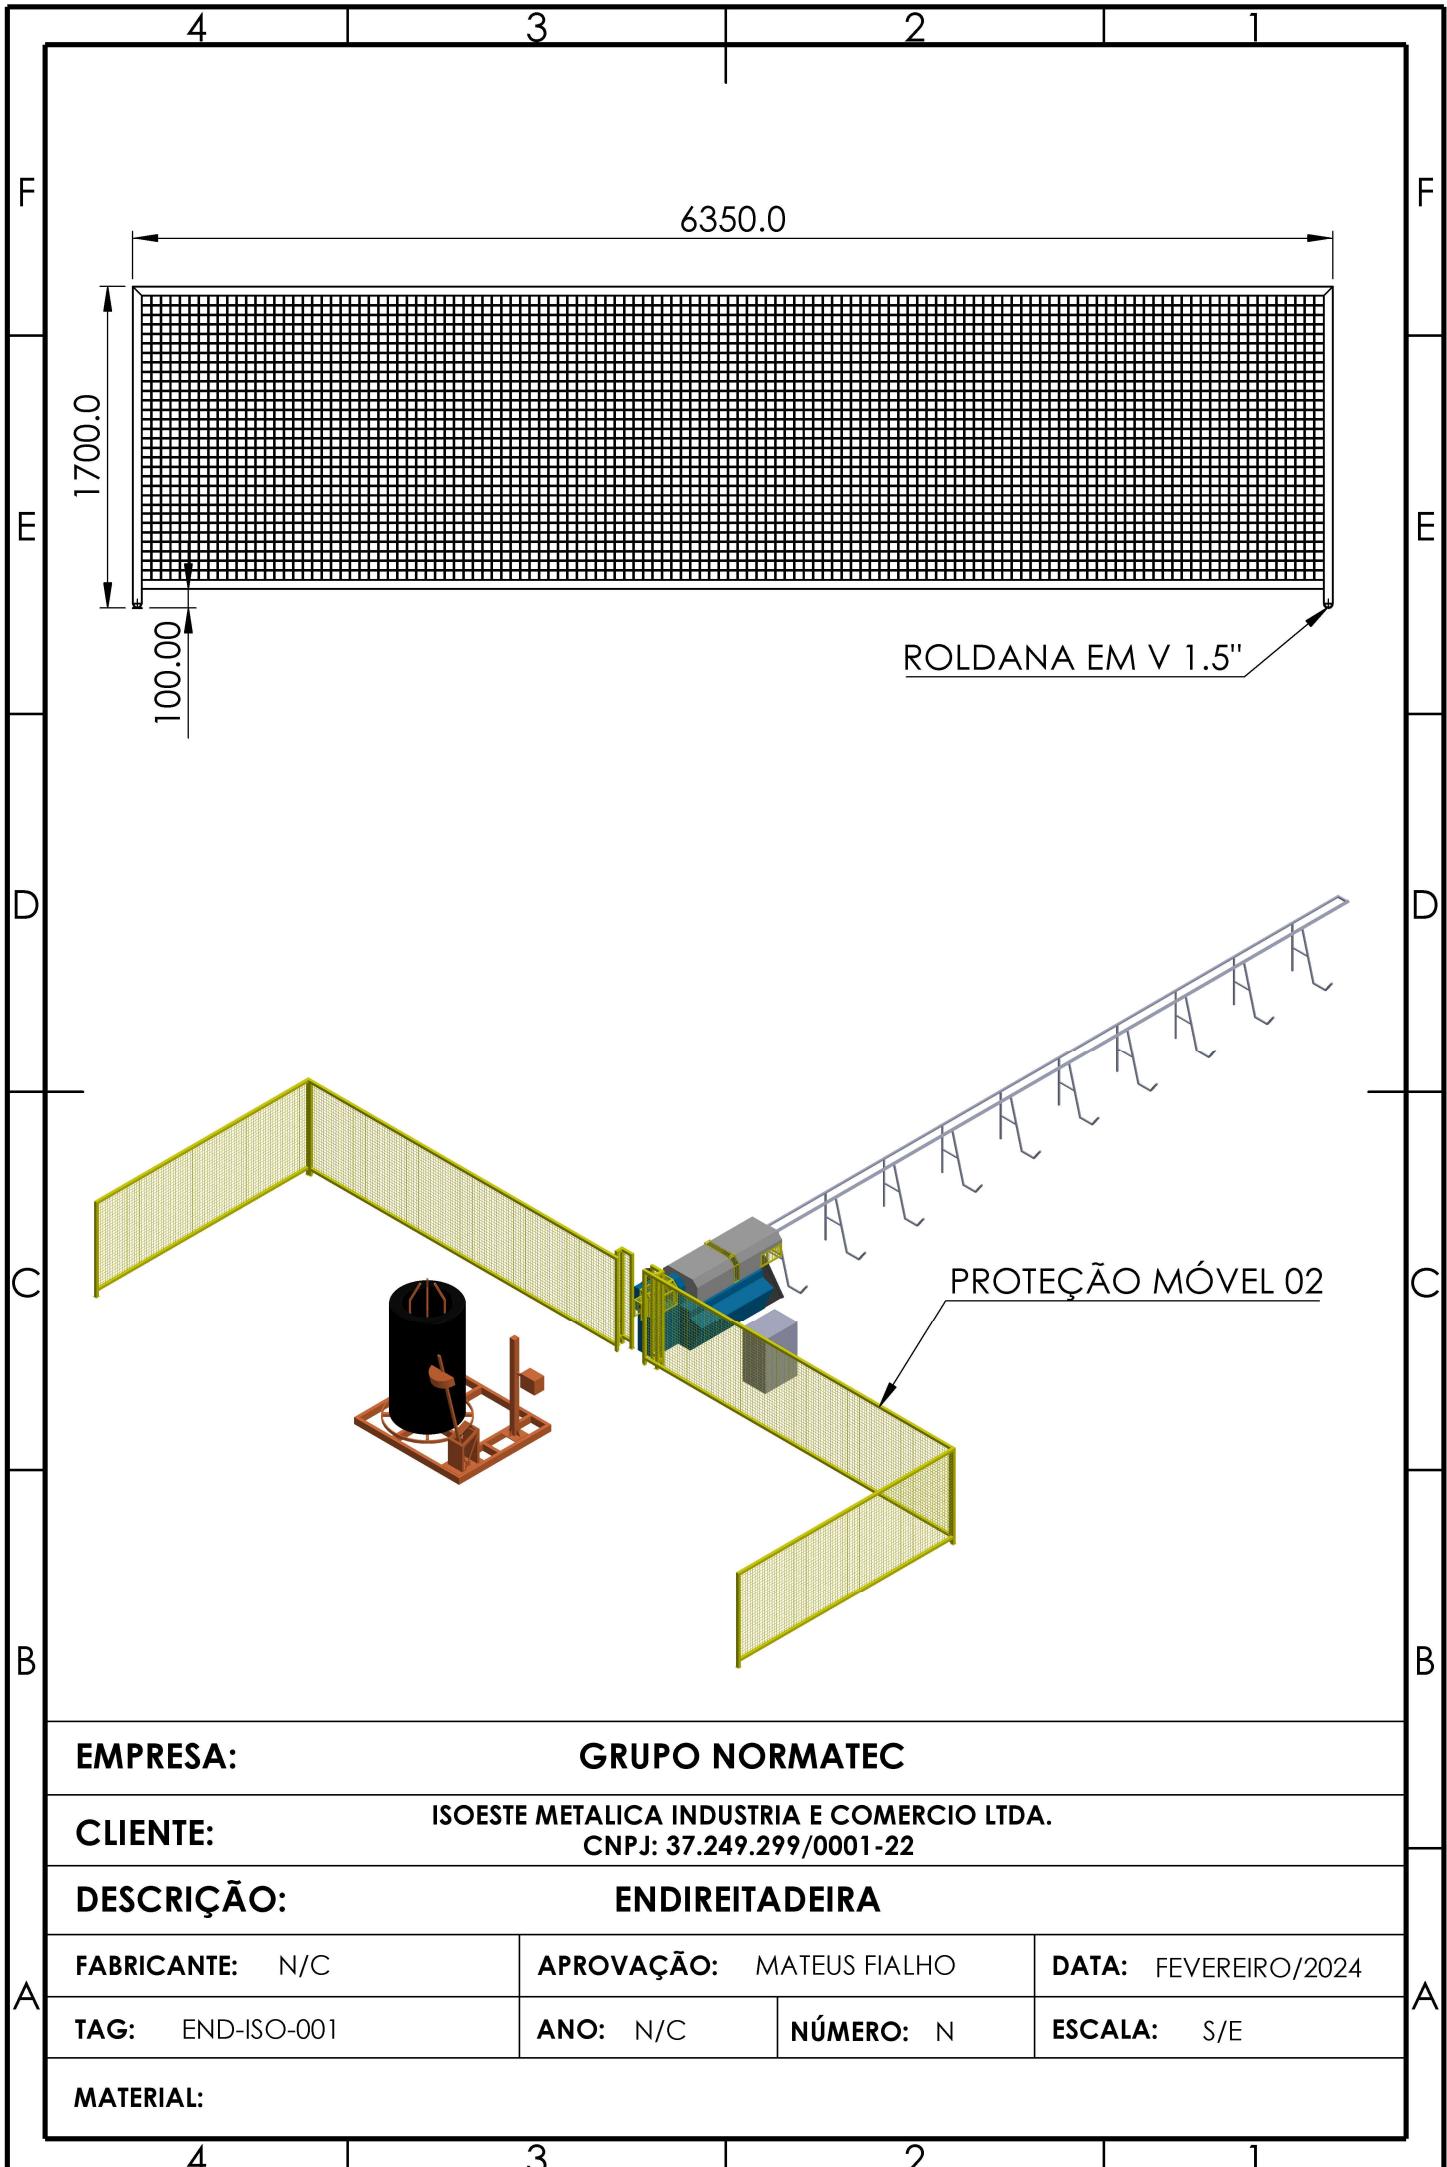

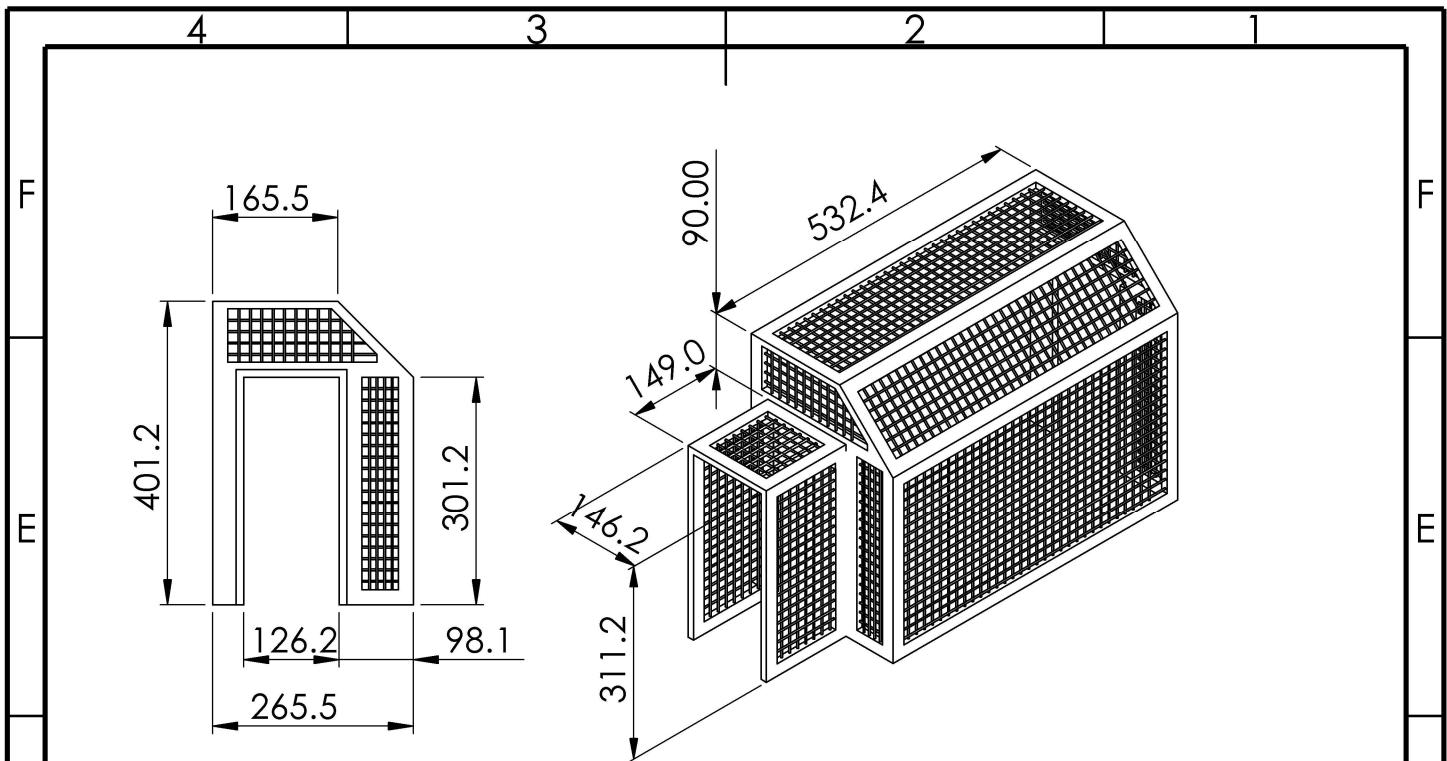

PROTEÇÃO ENTRADA DO EQUIPAMENTO

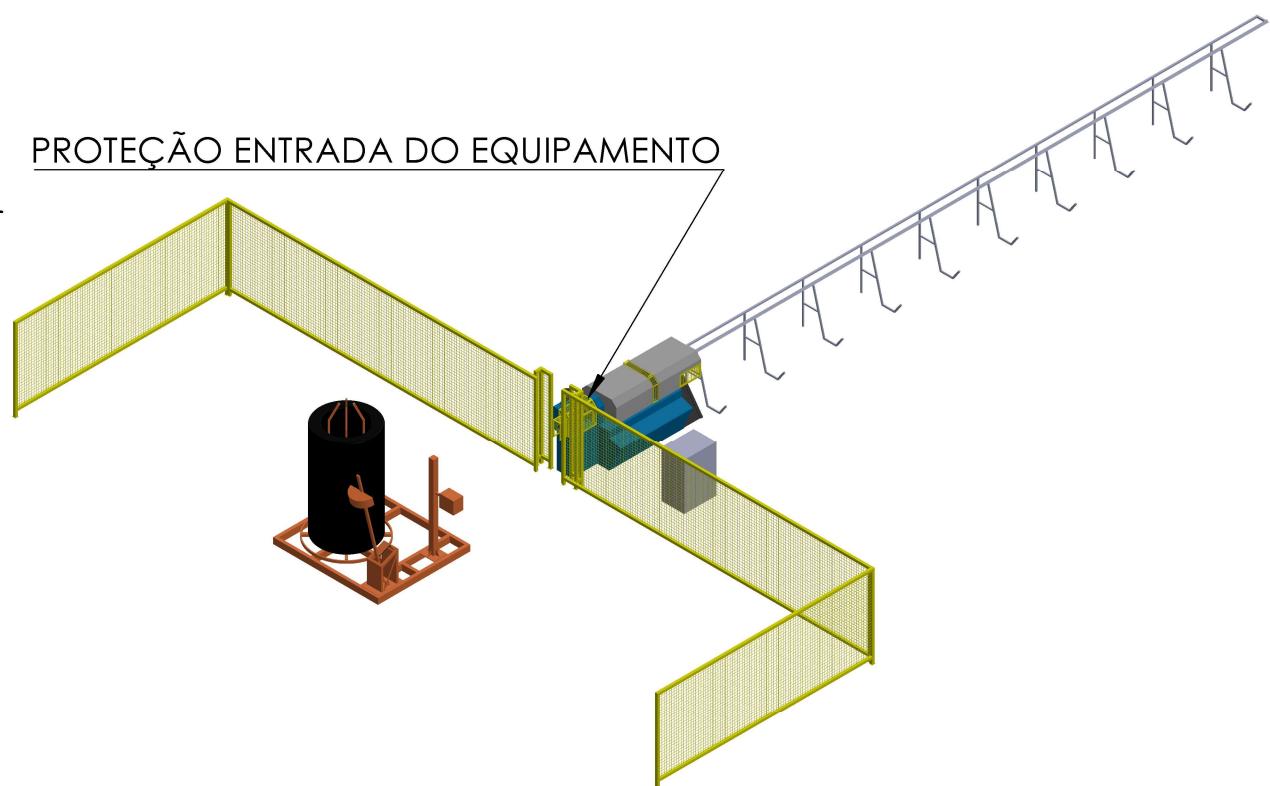

**EMPRESA:**

**GRUPO NORMATEC**

**CLIENTE:**

**ISOESTE METALICA INDUSTRIA E COMERCIO LTDA.**  
**CNPJ: 37.249.299/0001-22**

**DESCRÍÇÃO:**

**ENDIREITADEIRA**

**FABRICANTE:** N/C

**APROVAÇÃO:** MATEUS FIALHO

**DATA:** FEVEREIRO/2024

**TAG:** END-ISO-001

**ANO:** N/C

**NÚMERO:** N

**ESCALA:** S/E


**MATERIAL:**

4

3

2

1

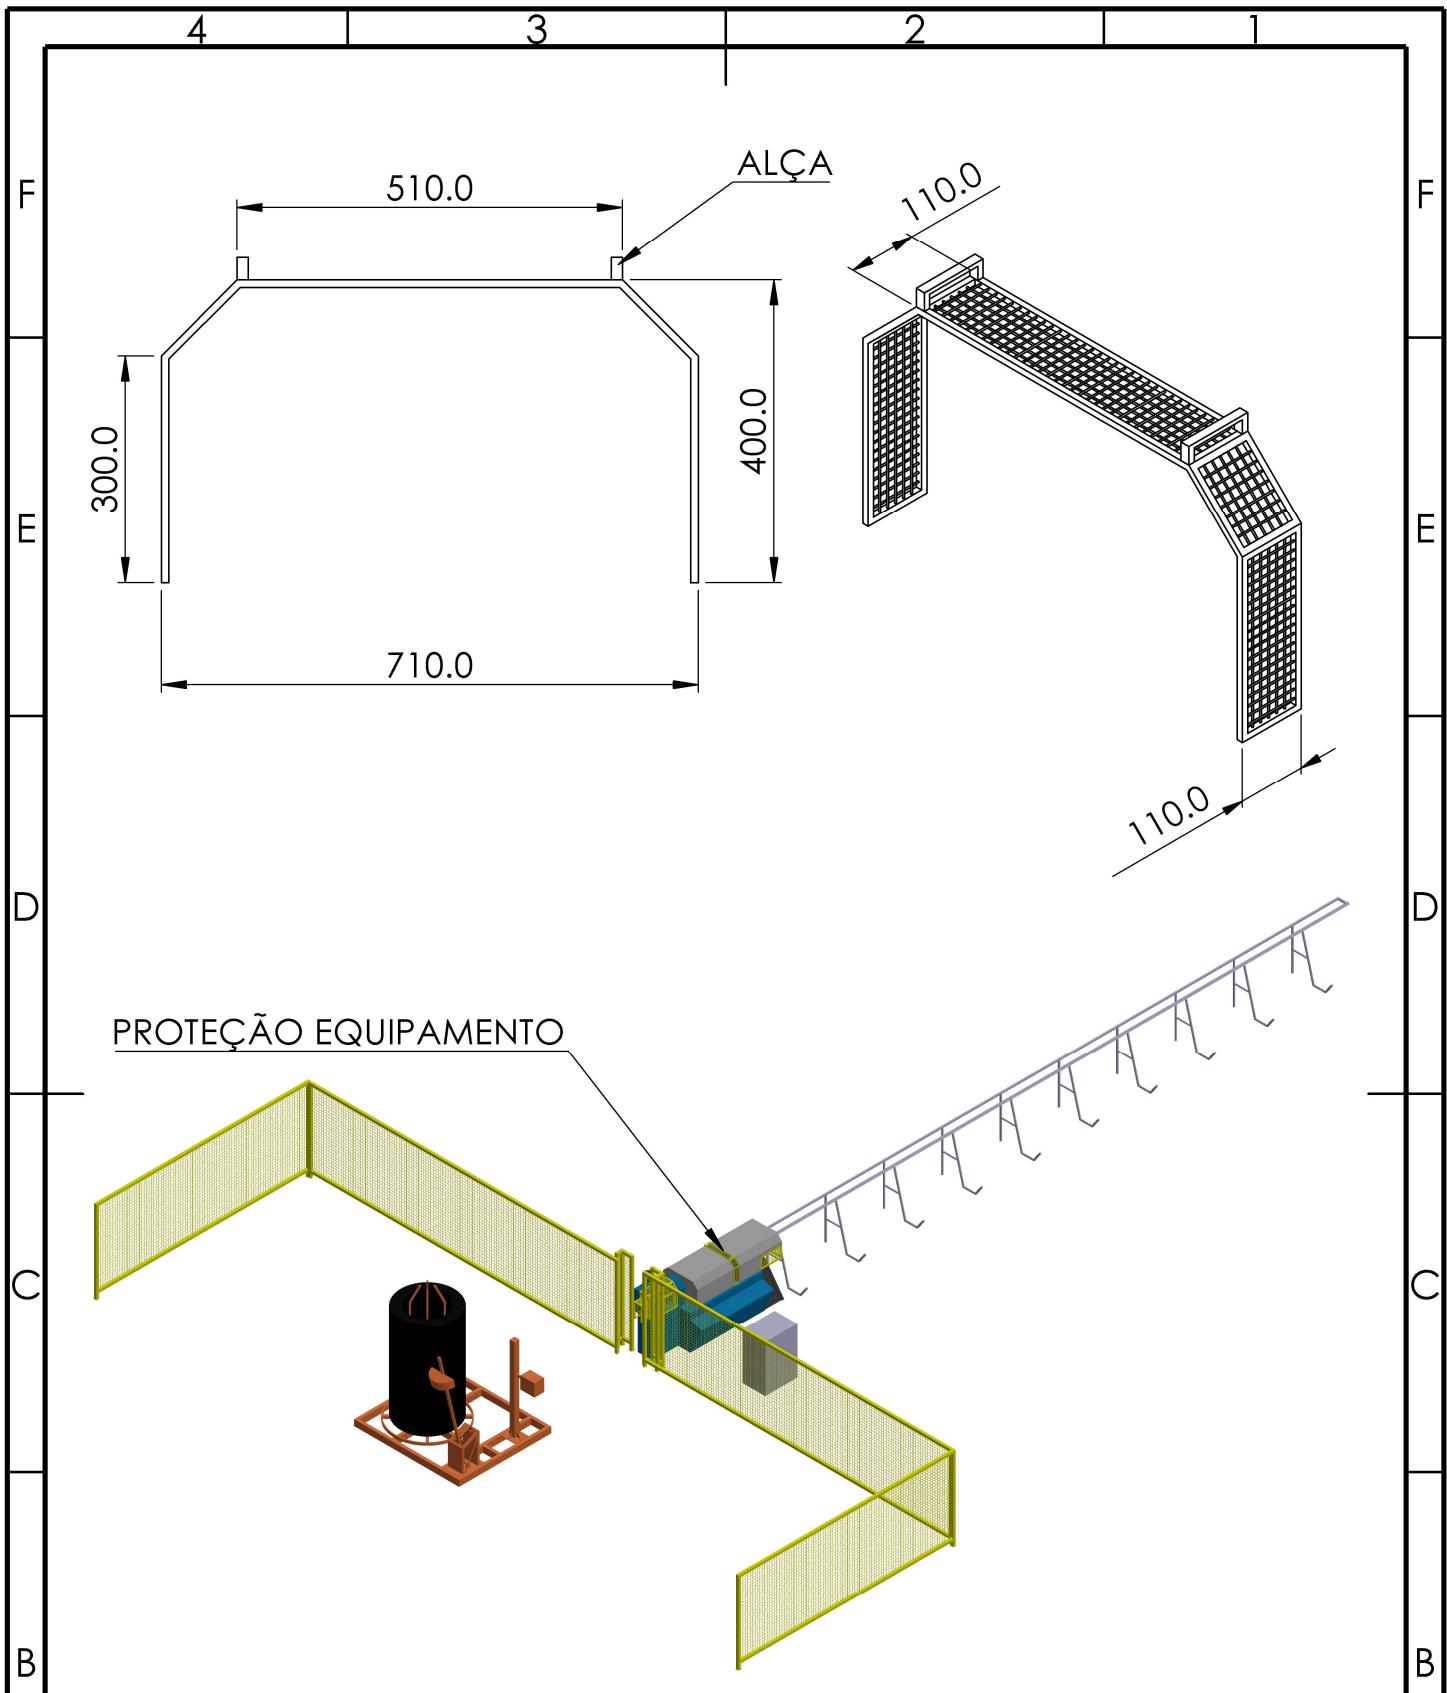

**EMPRESA:**

**GRUPO NORMATEC**

**CLIENTE:**

**ISOESTE METALICA INDUSTRIA E COMERCIO LTDA.**  
CNPJ: 37.249.299/0001-22

**DESCRIÇÃO:**

**ENDIREITADEIRA**

**FABRICANTE:** N/C

**APROVAÇÃO:** MATEUS FIALHO

**DATA:** FEVEREIRO/2024

**TAG:** END-ISO-001

**ANO:** N/C

**NÚMERO:** N

**ESCALA:** S/E

**MATERIAL:**

4

3

2

1

