

ITENS	NOMES
01	PROTEÇÃO FIXA 01
02	PROTEÇÃO FIXA 02
03	PROTEÇÃO FIXA 03
04	PROTEÇÃO MÓVEL COM SENSOR DE MOVIMENTO 01
05	PROTEÇÃO MÓVEL COM SENSOR DE MOVIMENTO 02
06	PROTEÇÃO MÓVEL COM SENSOR DE MOVIMENTO 03
07	PROTEÇÃO MÓVEL COM SENSOR DE MOVIMENTO 04
08	PROTEÇÃO FIXA PARAFUSADA
09	BOTÃO BIMANUAL C/ PEDAL
10	SUPORTE C/ BOMBA HIDRÁULICA
11	PAINEL ELÉTRICO 01
12	PAINEL ELÉTRICO 02
13	PAINEL ELÉTRICO 03
14	PAINEL ELÉTRICO 04
15	PAINEL ELÉTRICO
16	BOBINADORA
17	BLANQUE
18	PRENSA HIDRÁULICA

EMPRESA:

GRUPO NORMATEC

CLIENTE:

ISOESTE METALICA INDUSTRIA E COMERCIO LTDA.
CNPJ: 37.249.299/0001-22

DESCRIÇÃO:

PRENSA HIDRÁULICA

FABRICANTE: HIDRAL - MAC

APROVAÇÃO: MATHEUS FIALHO

DATA: JANEIRO/2024


TAG: PRH - 1231


ANO: 2011


NÚMERO: 3285


ESCALA: 1 : 60


MATERIAL:

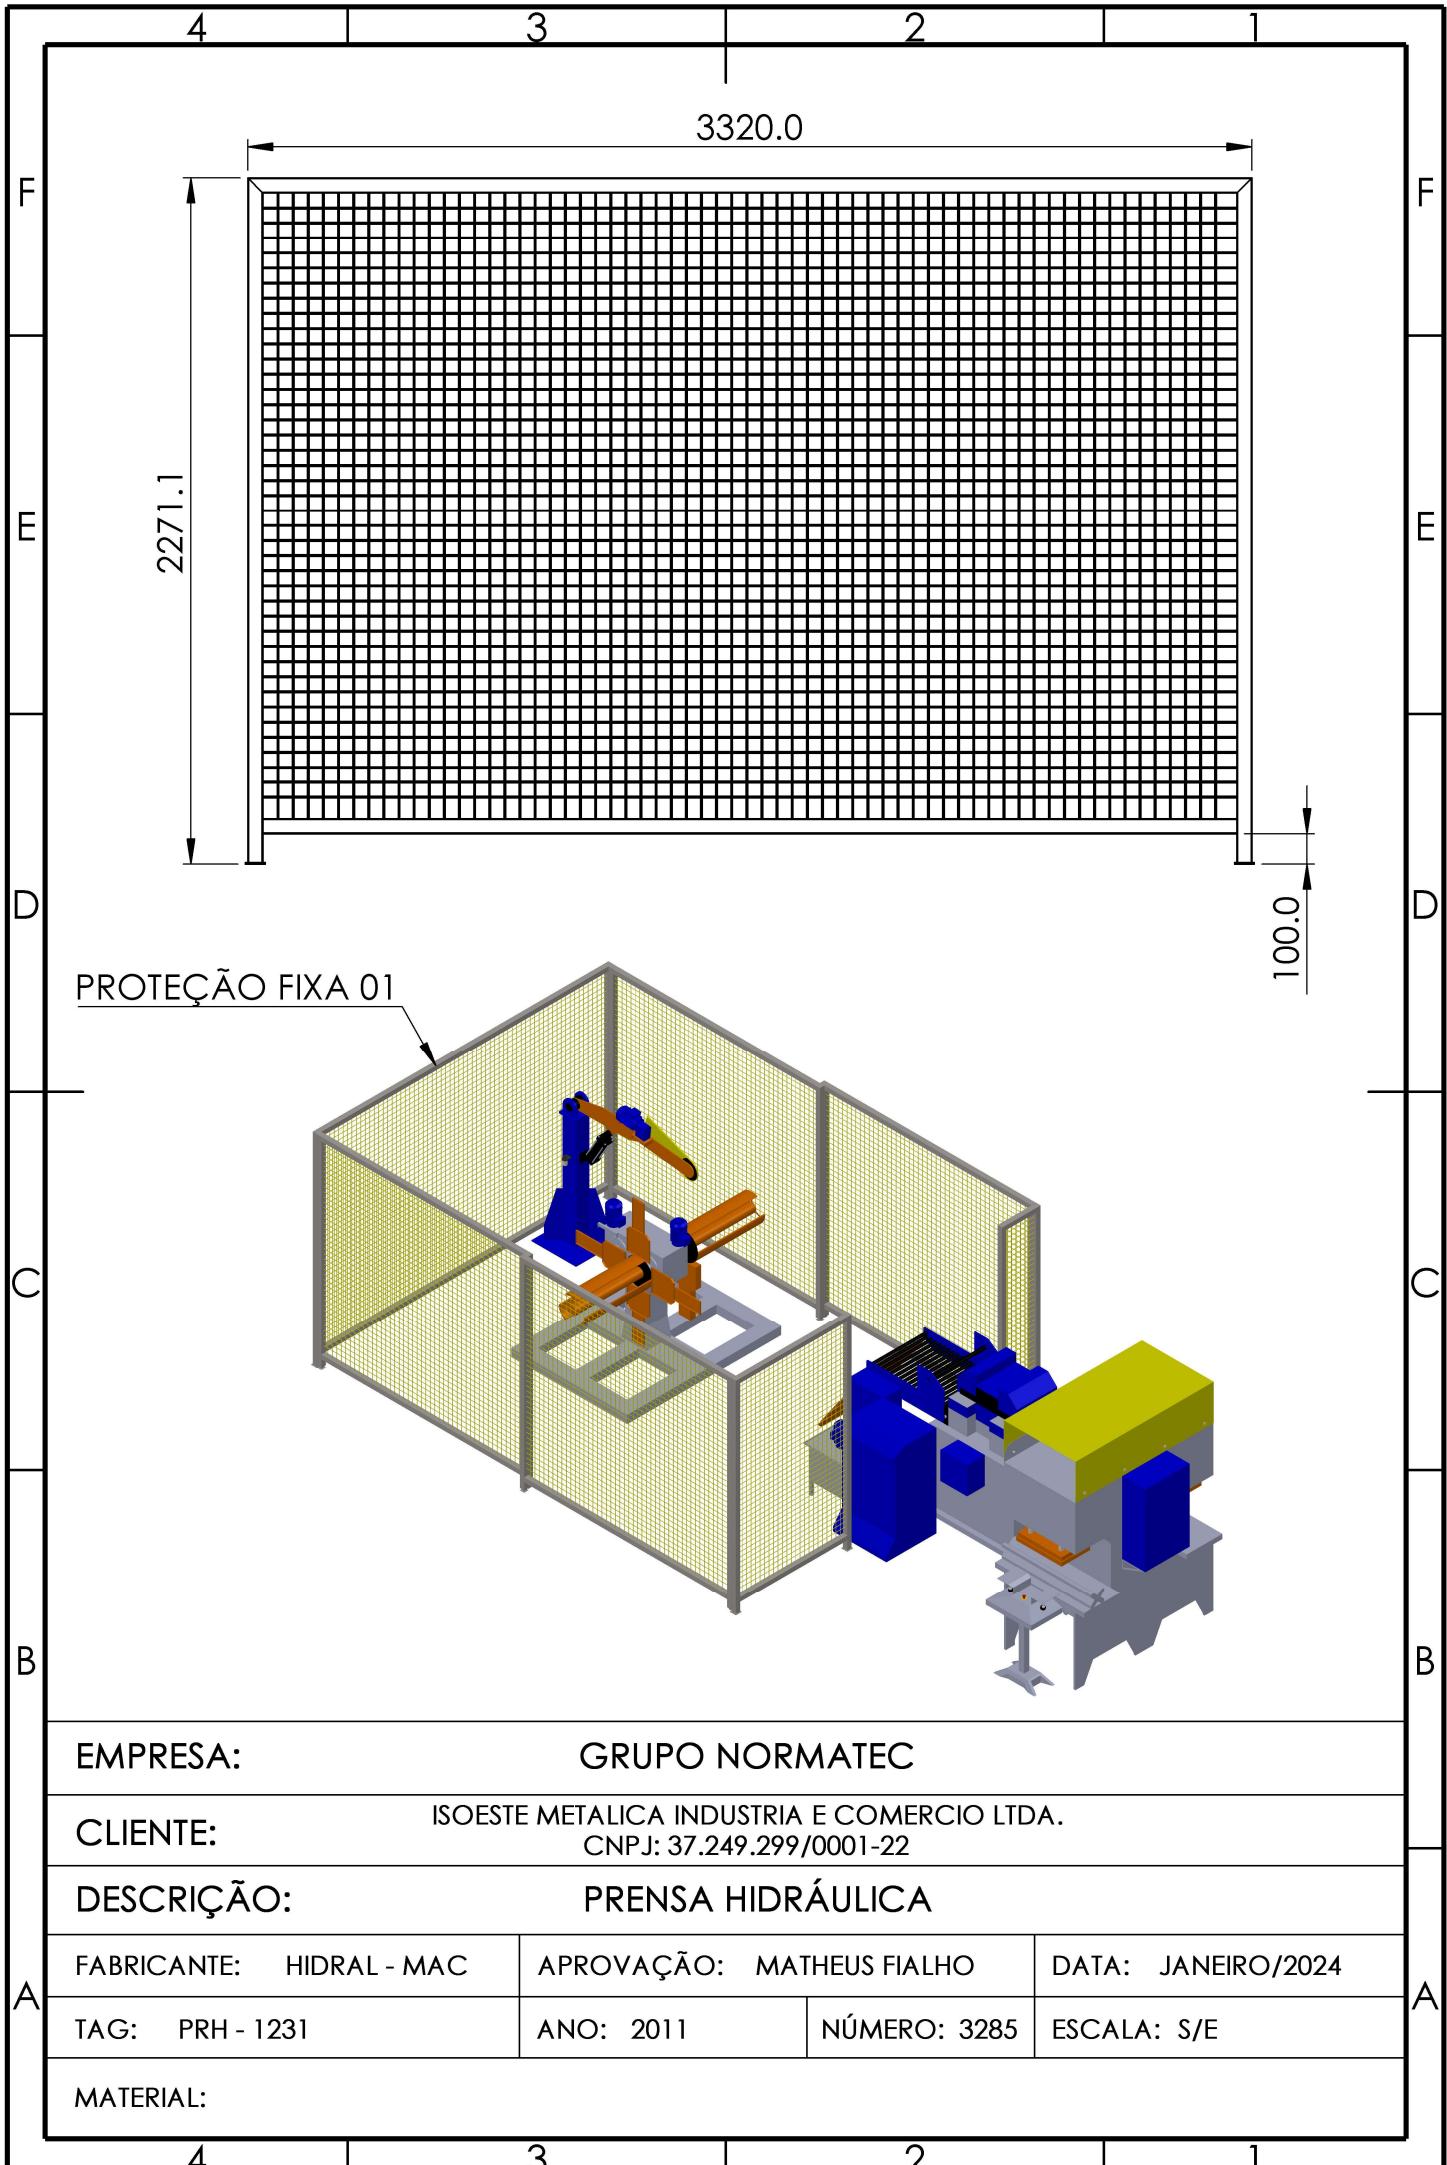


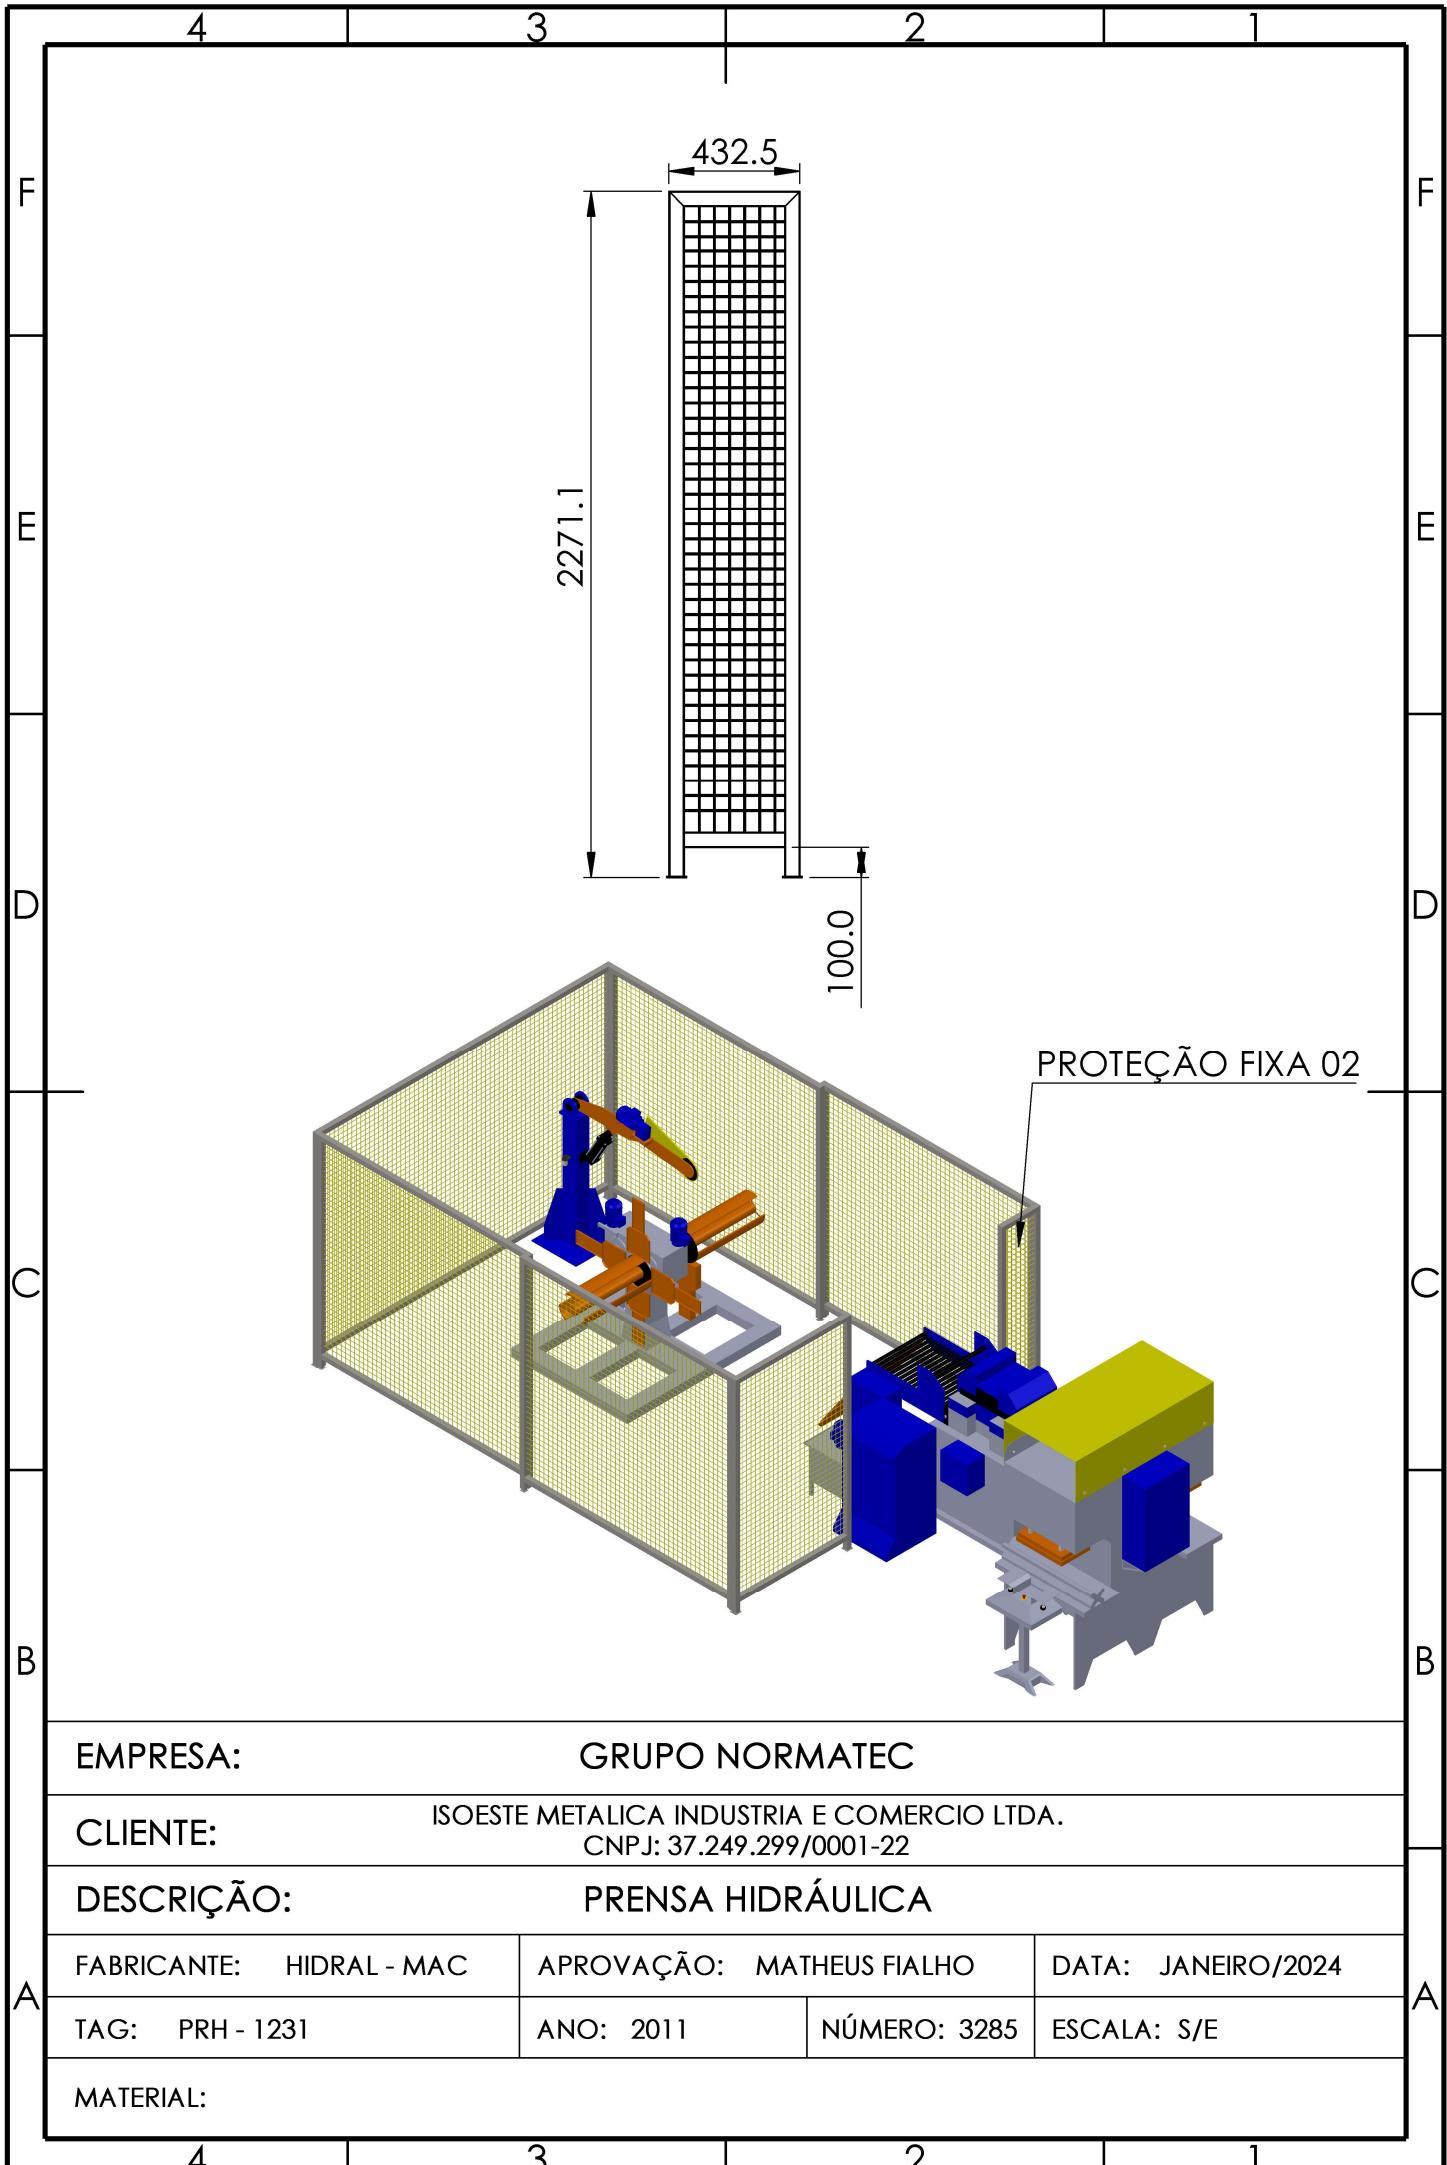


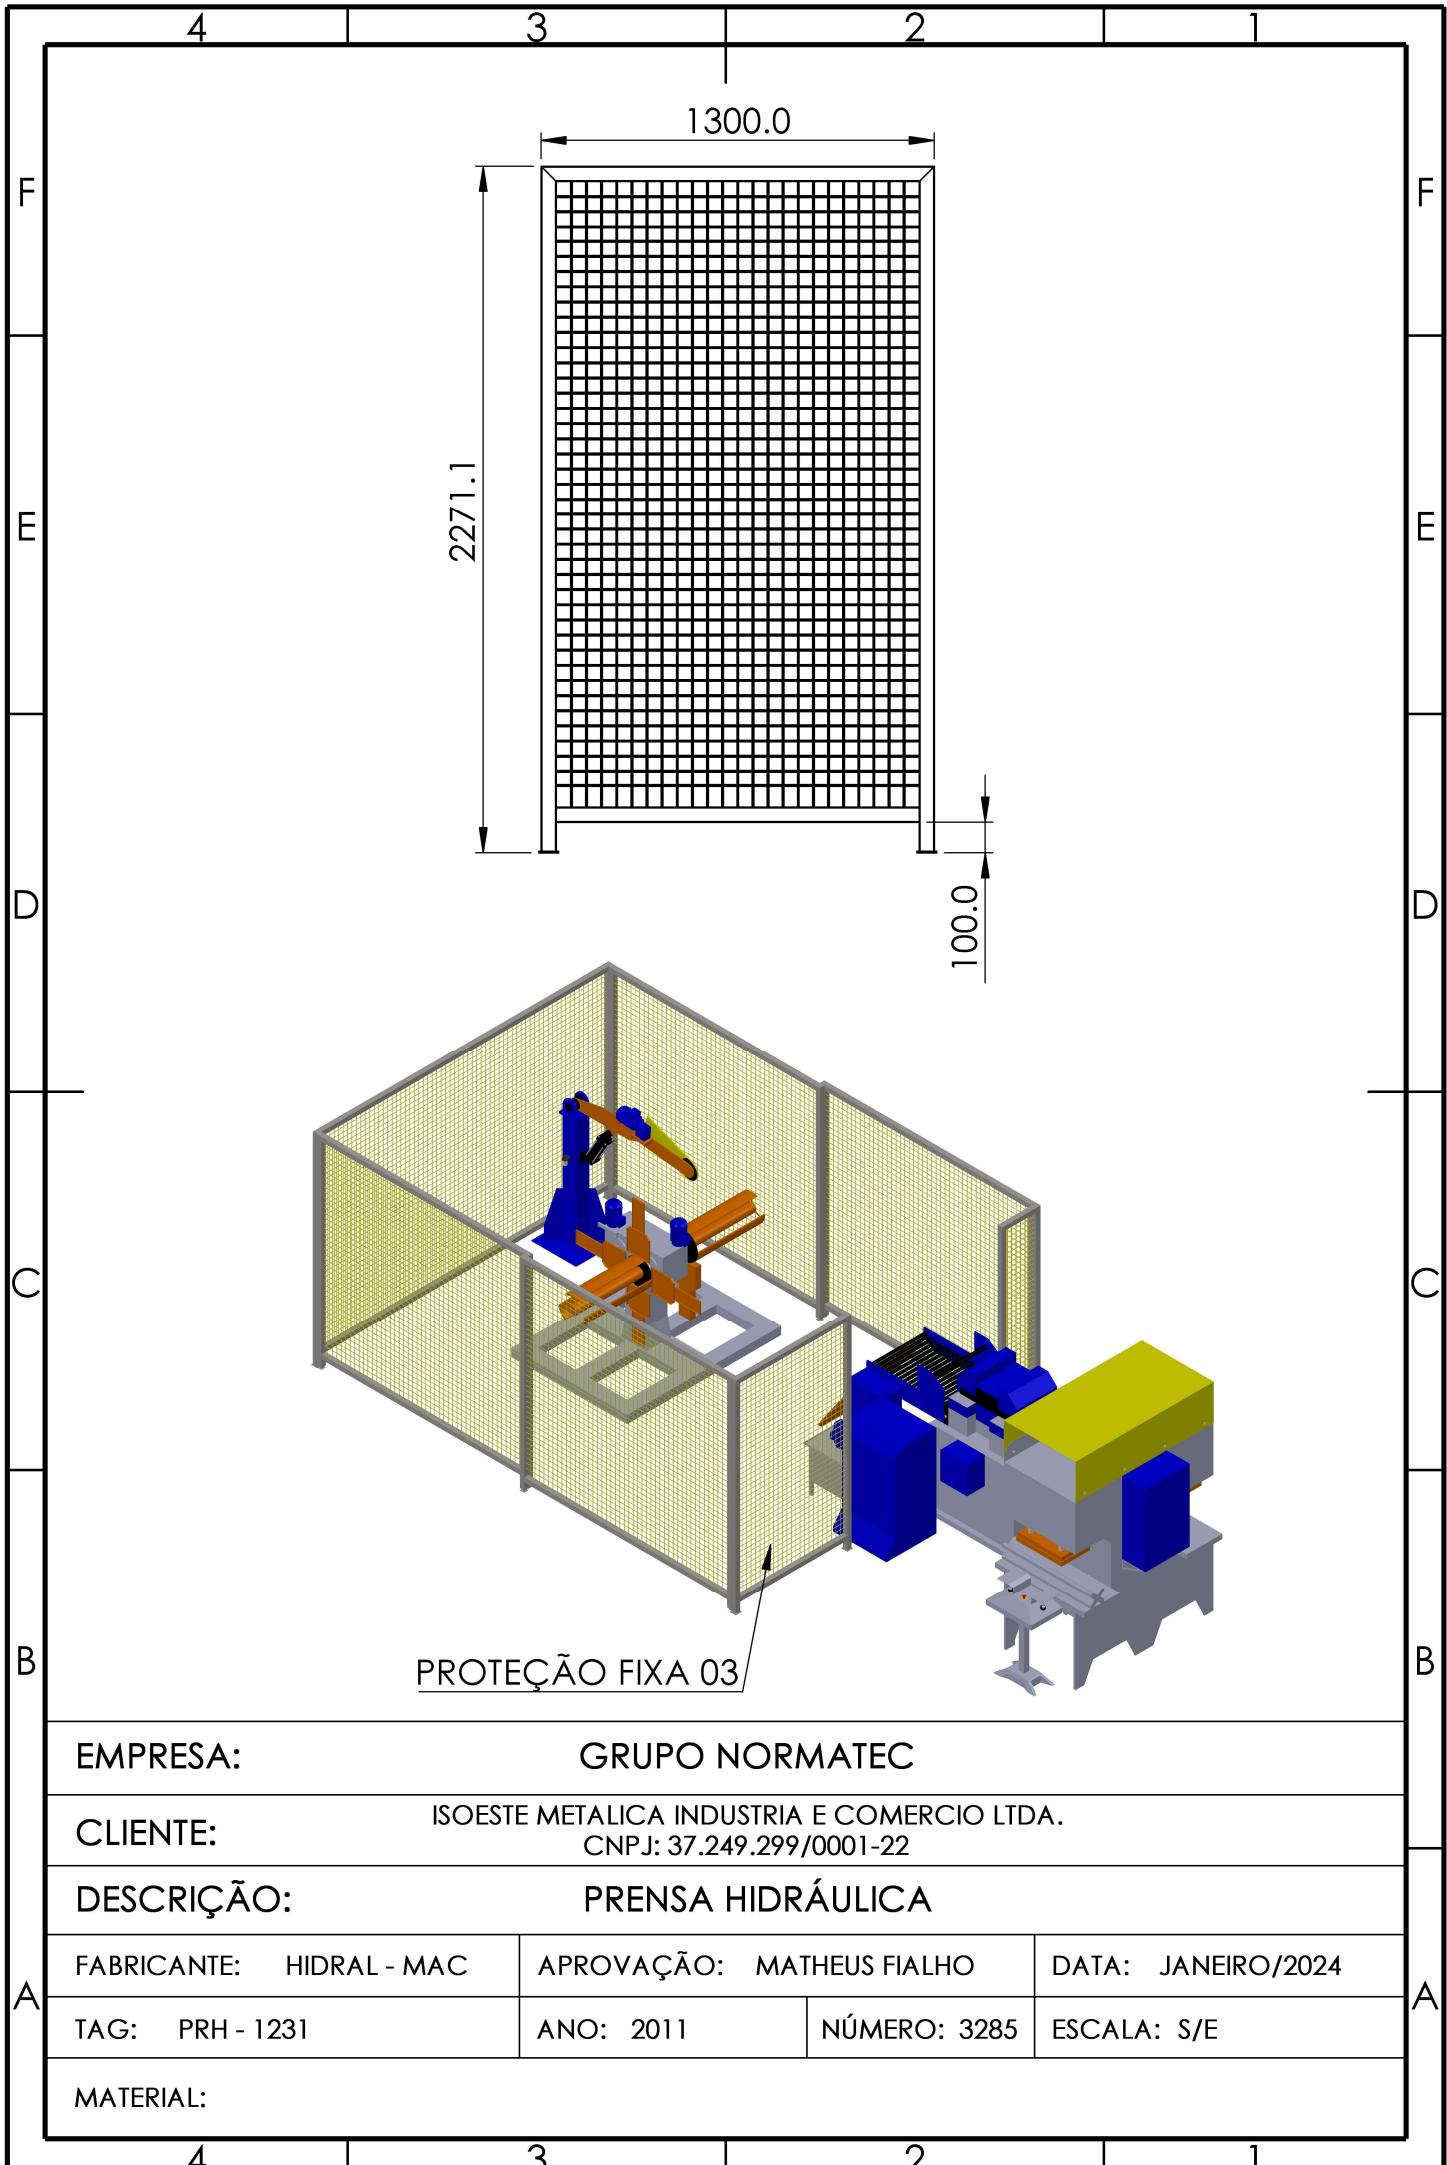


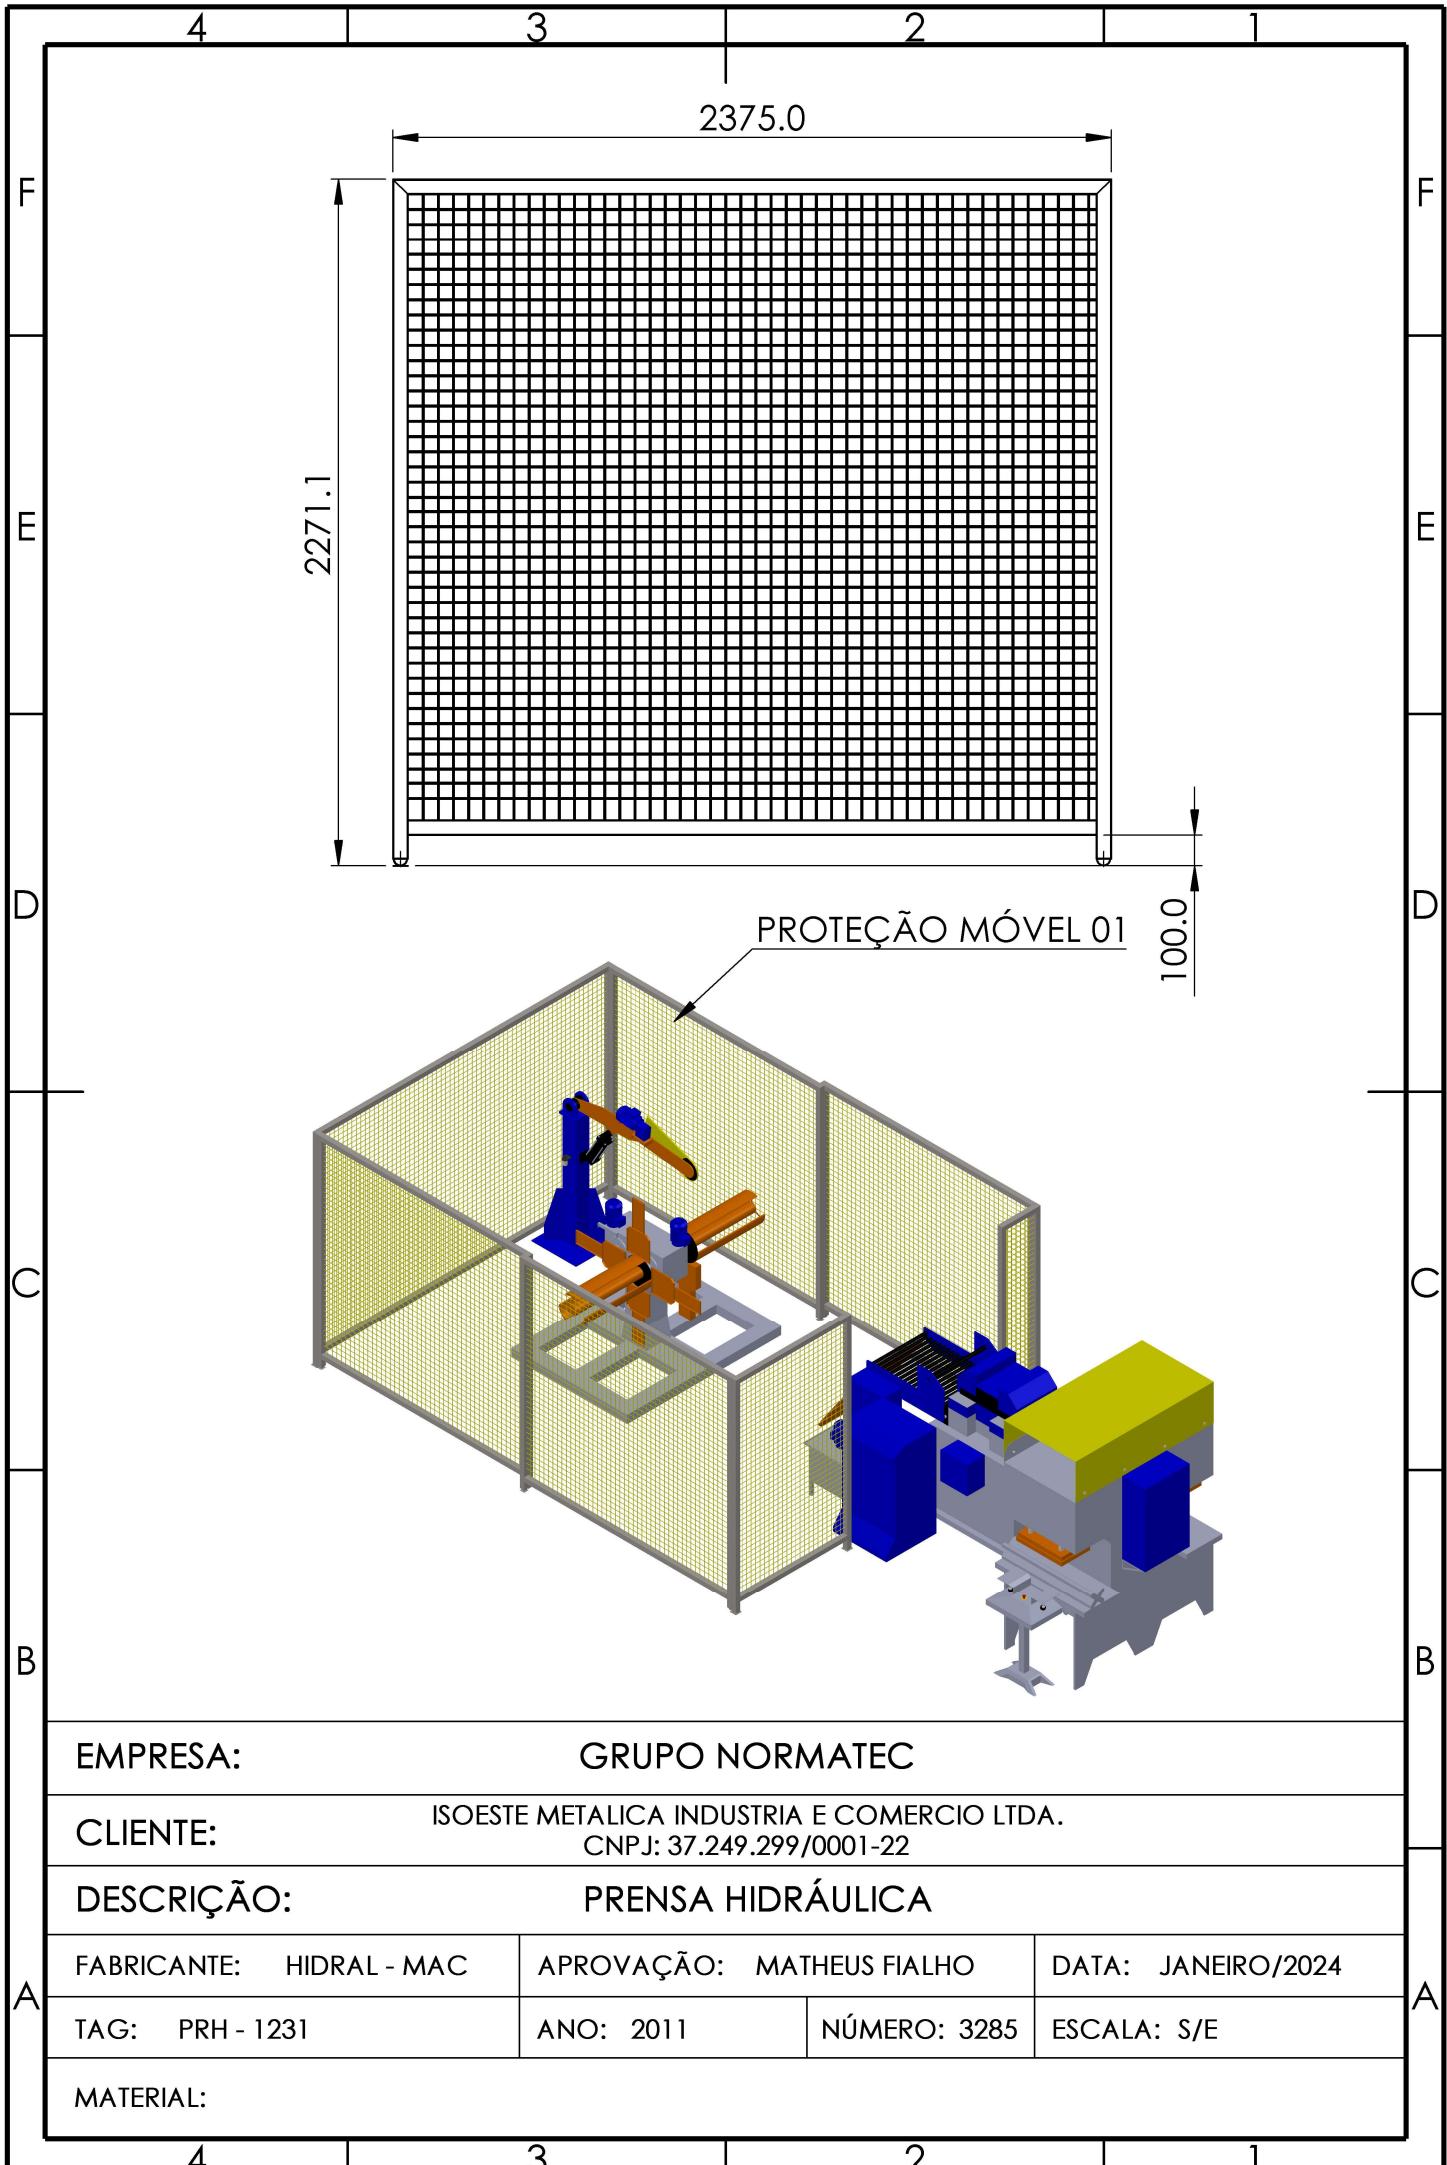


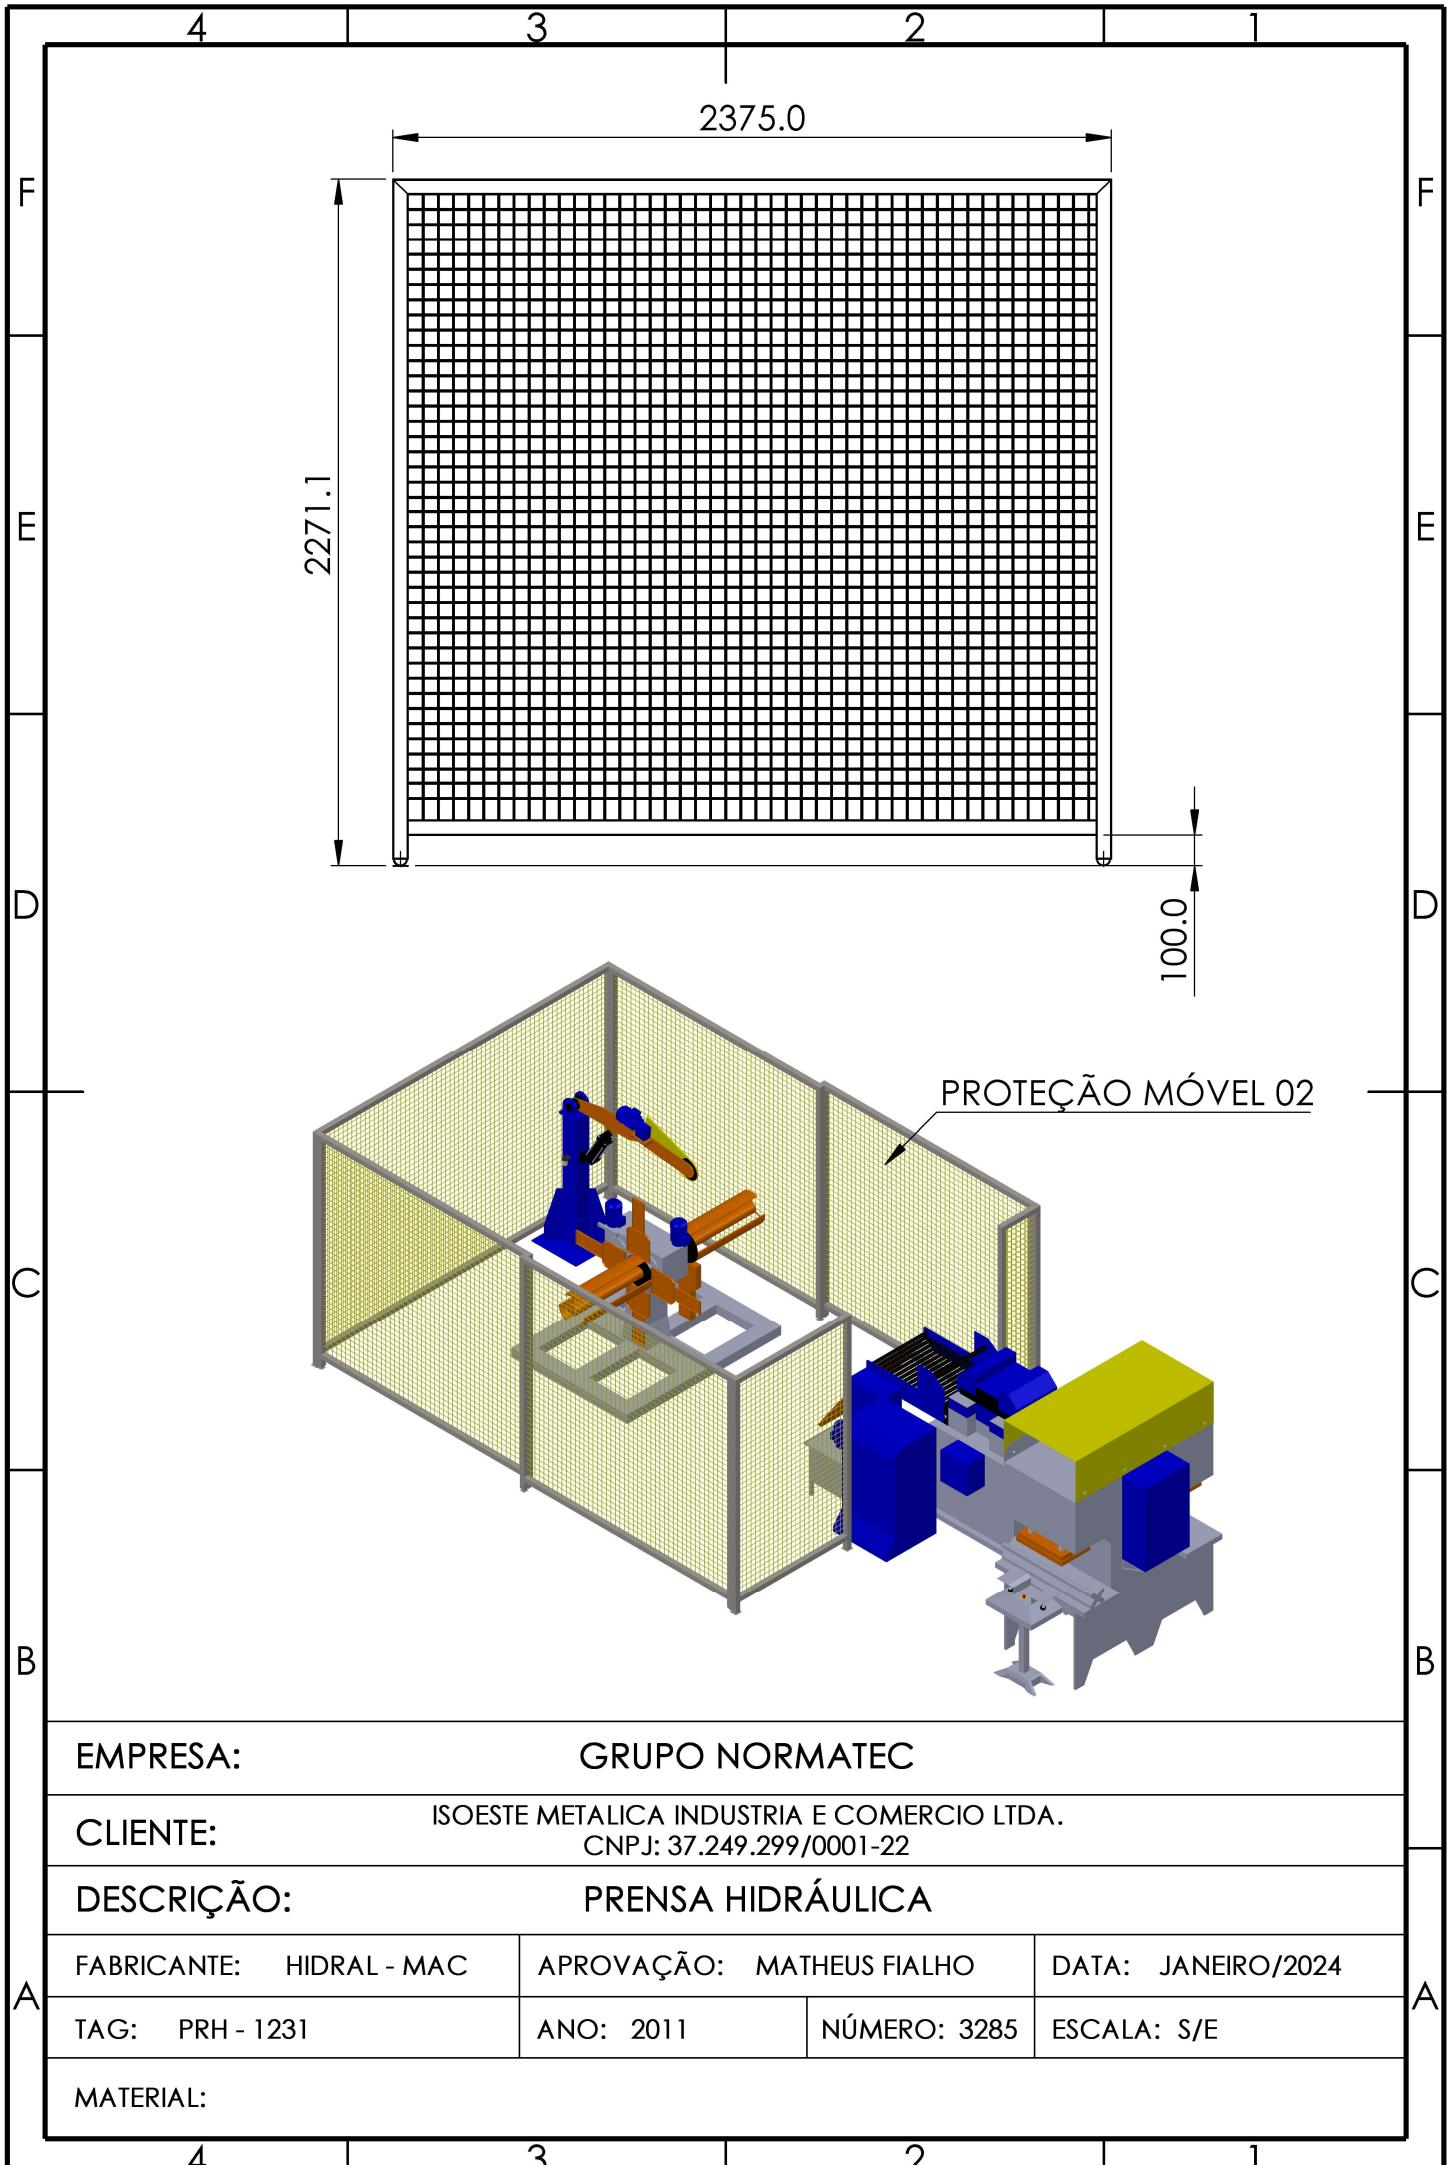

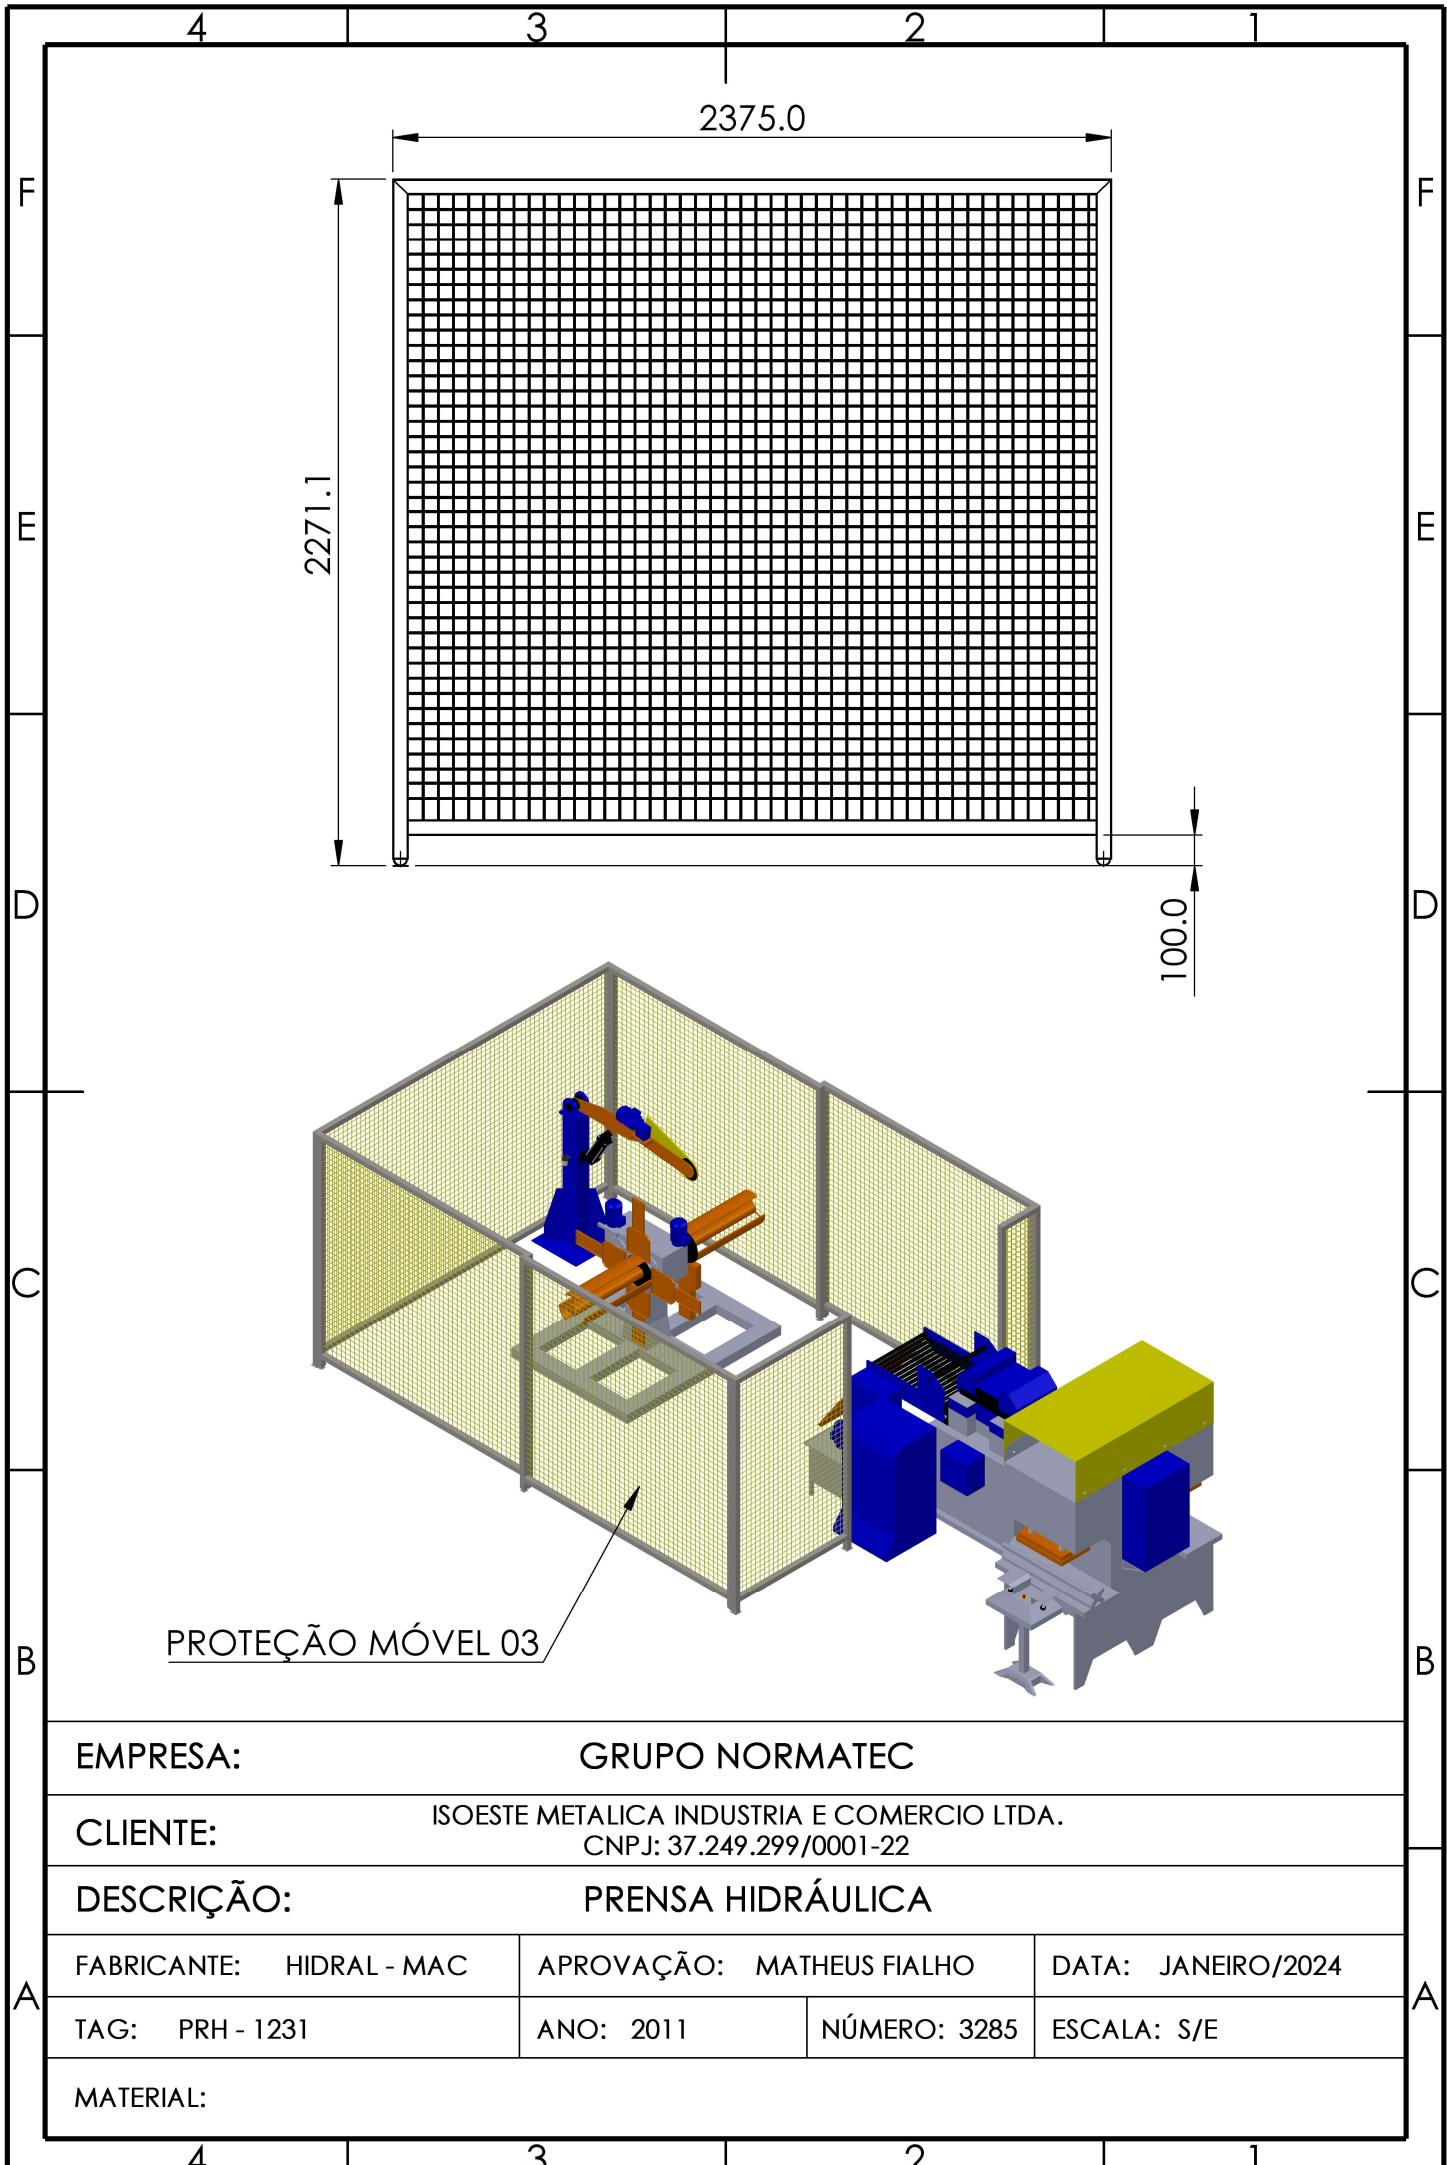

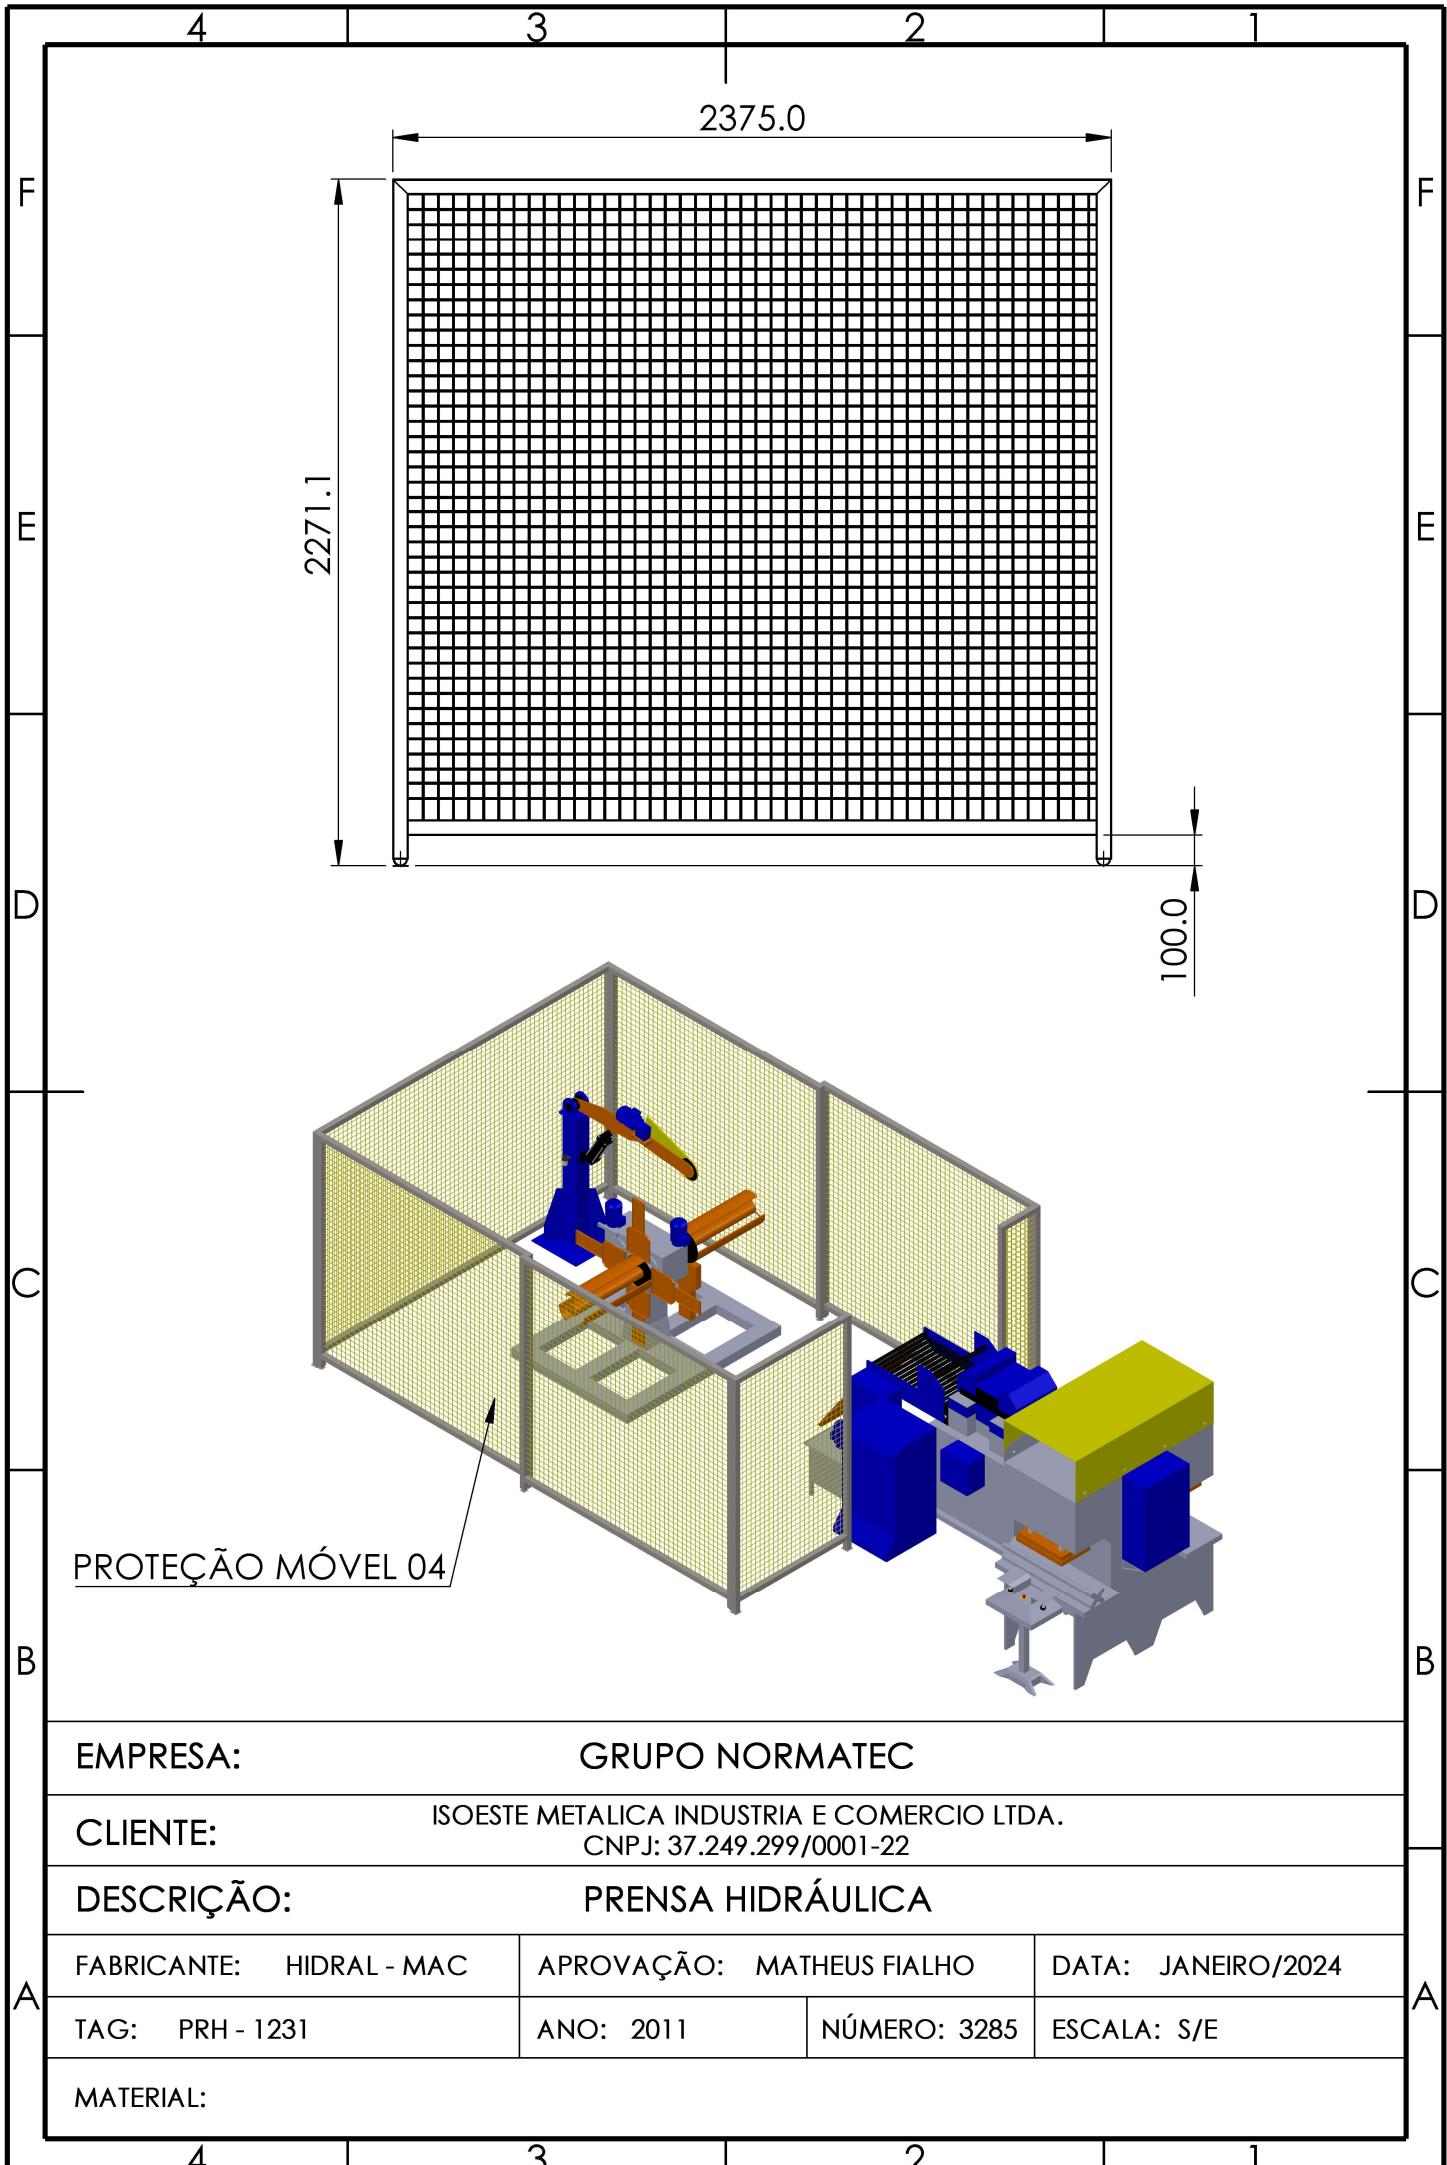

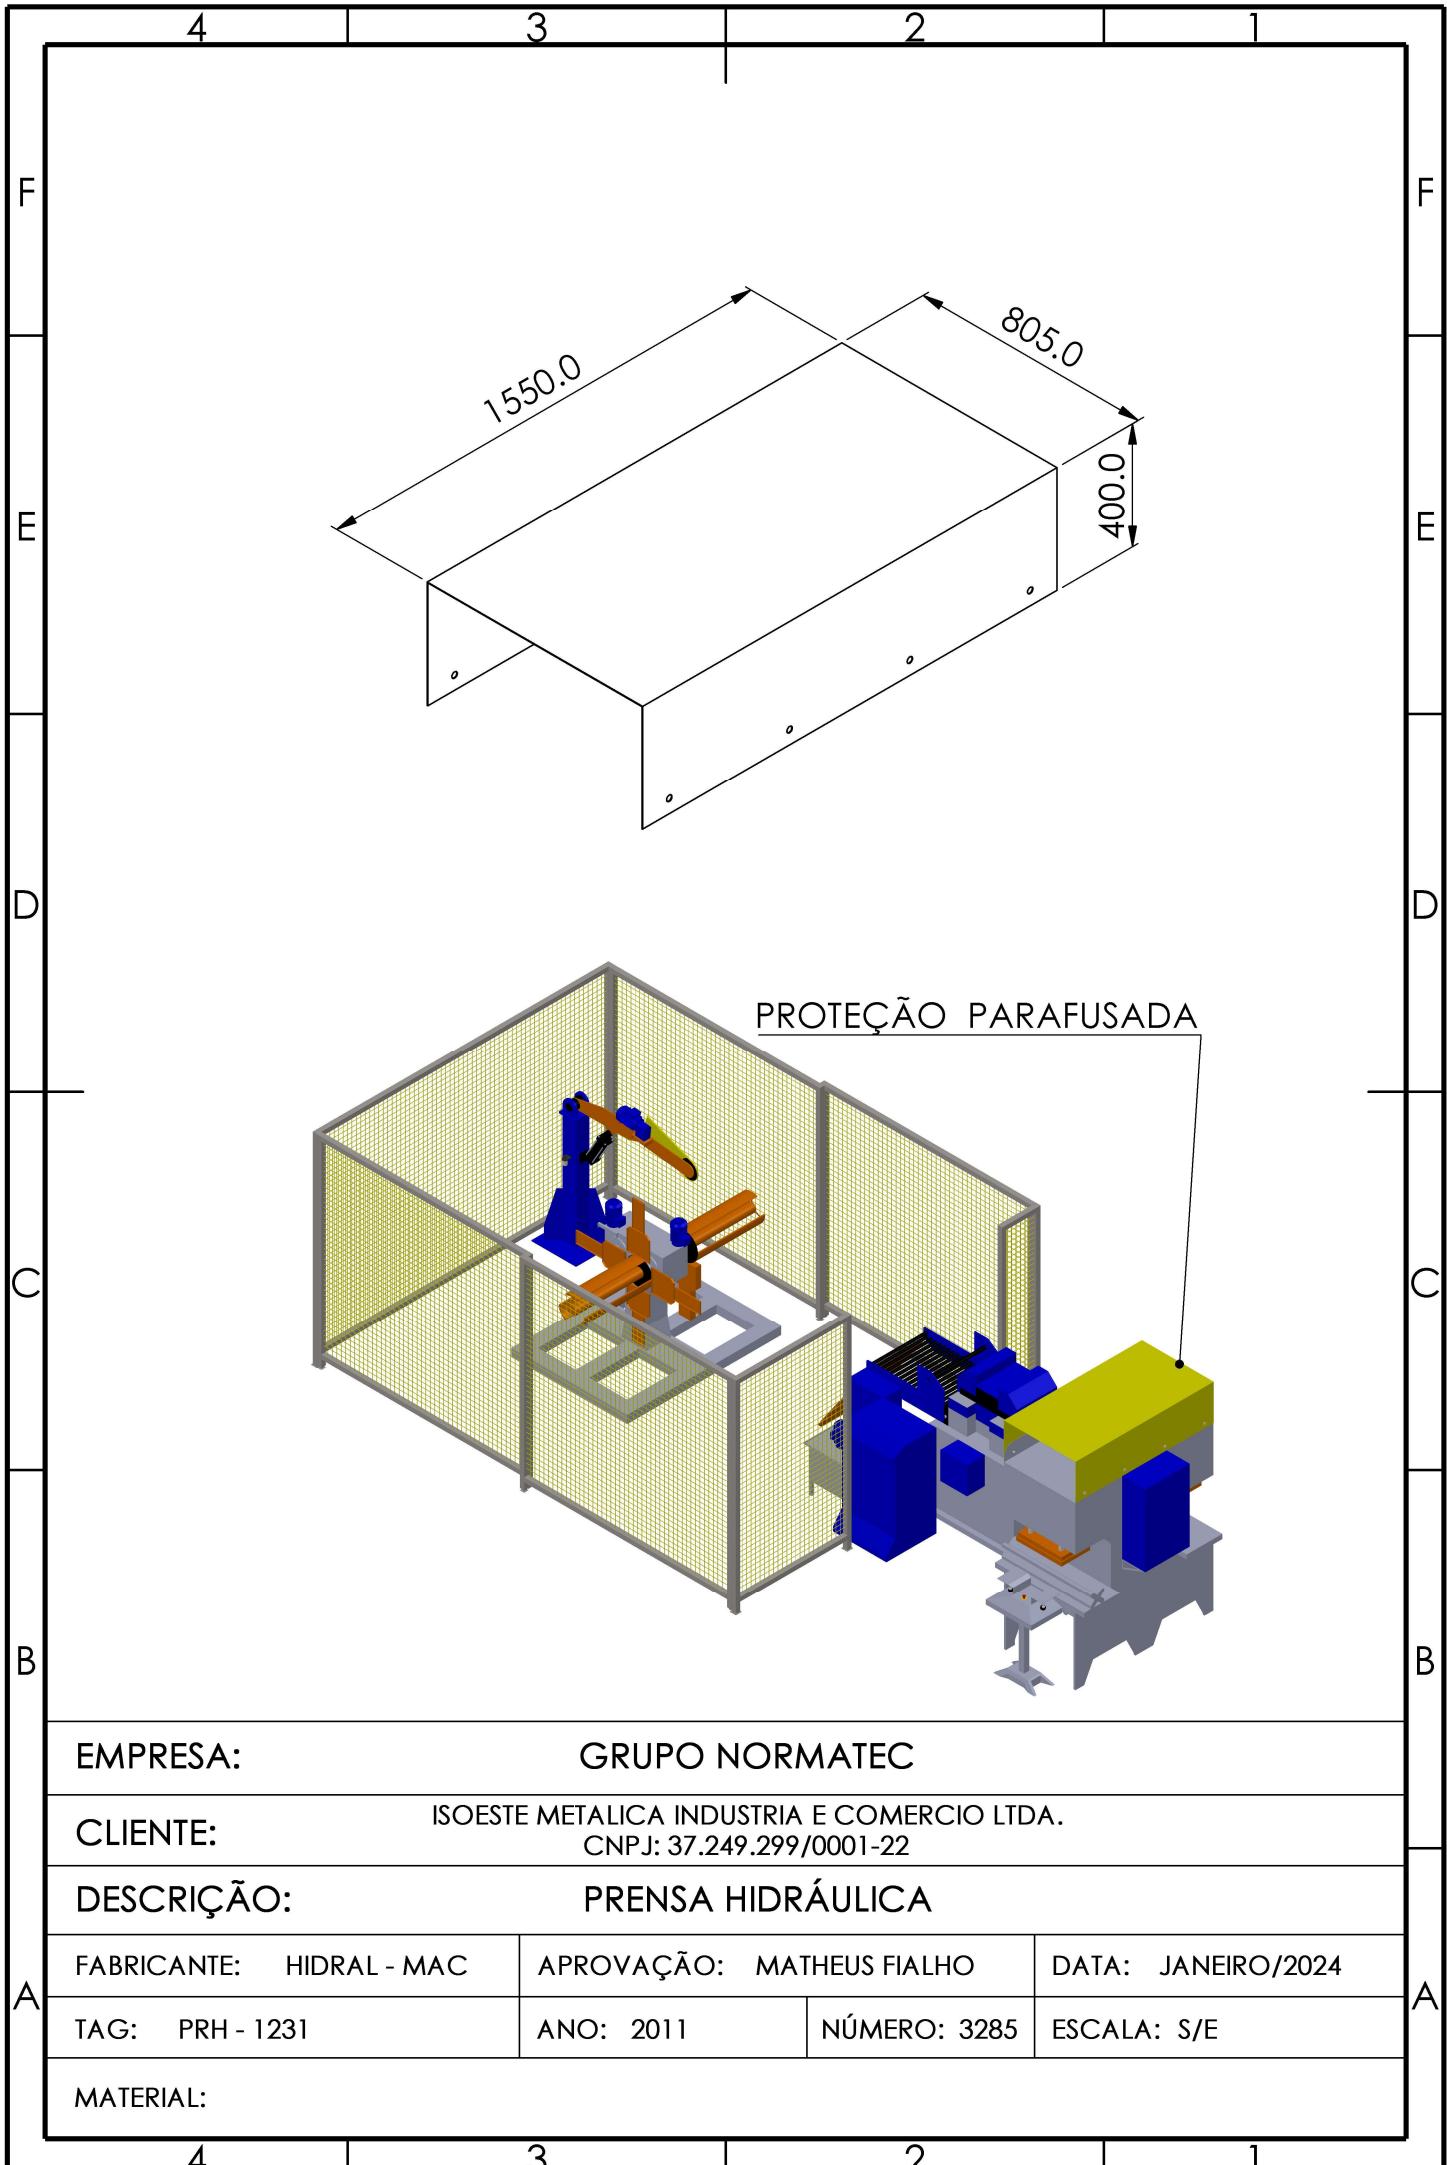

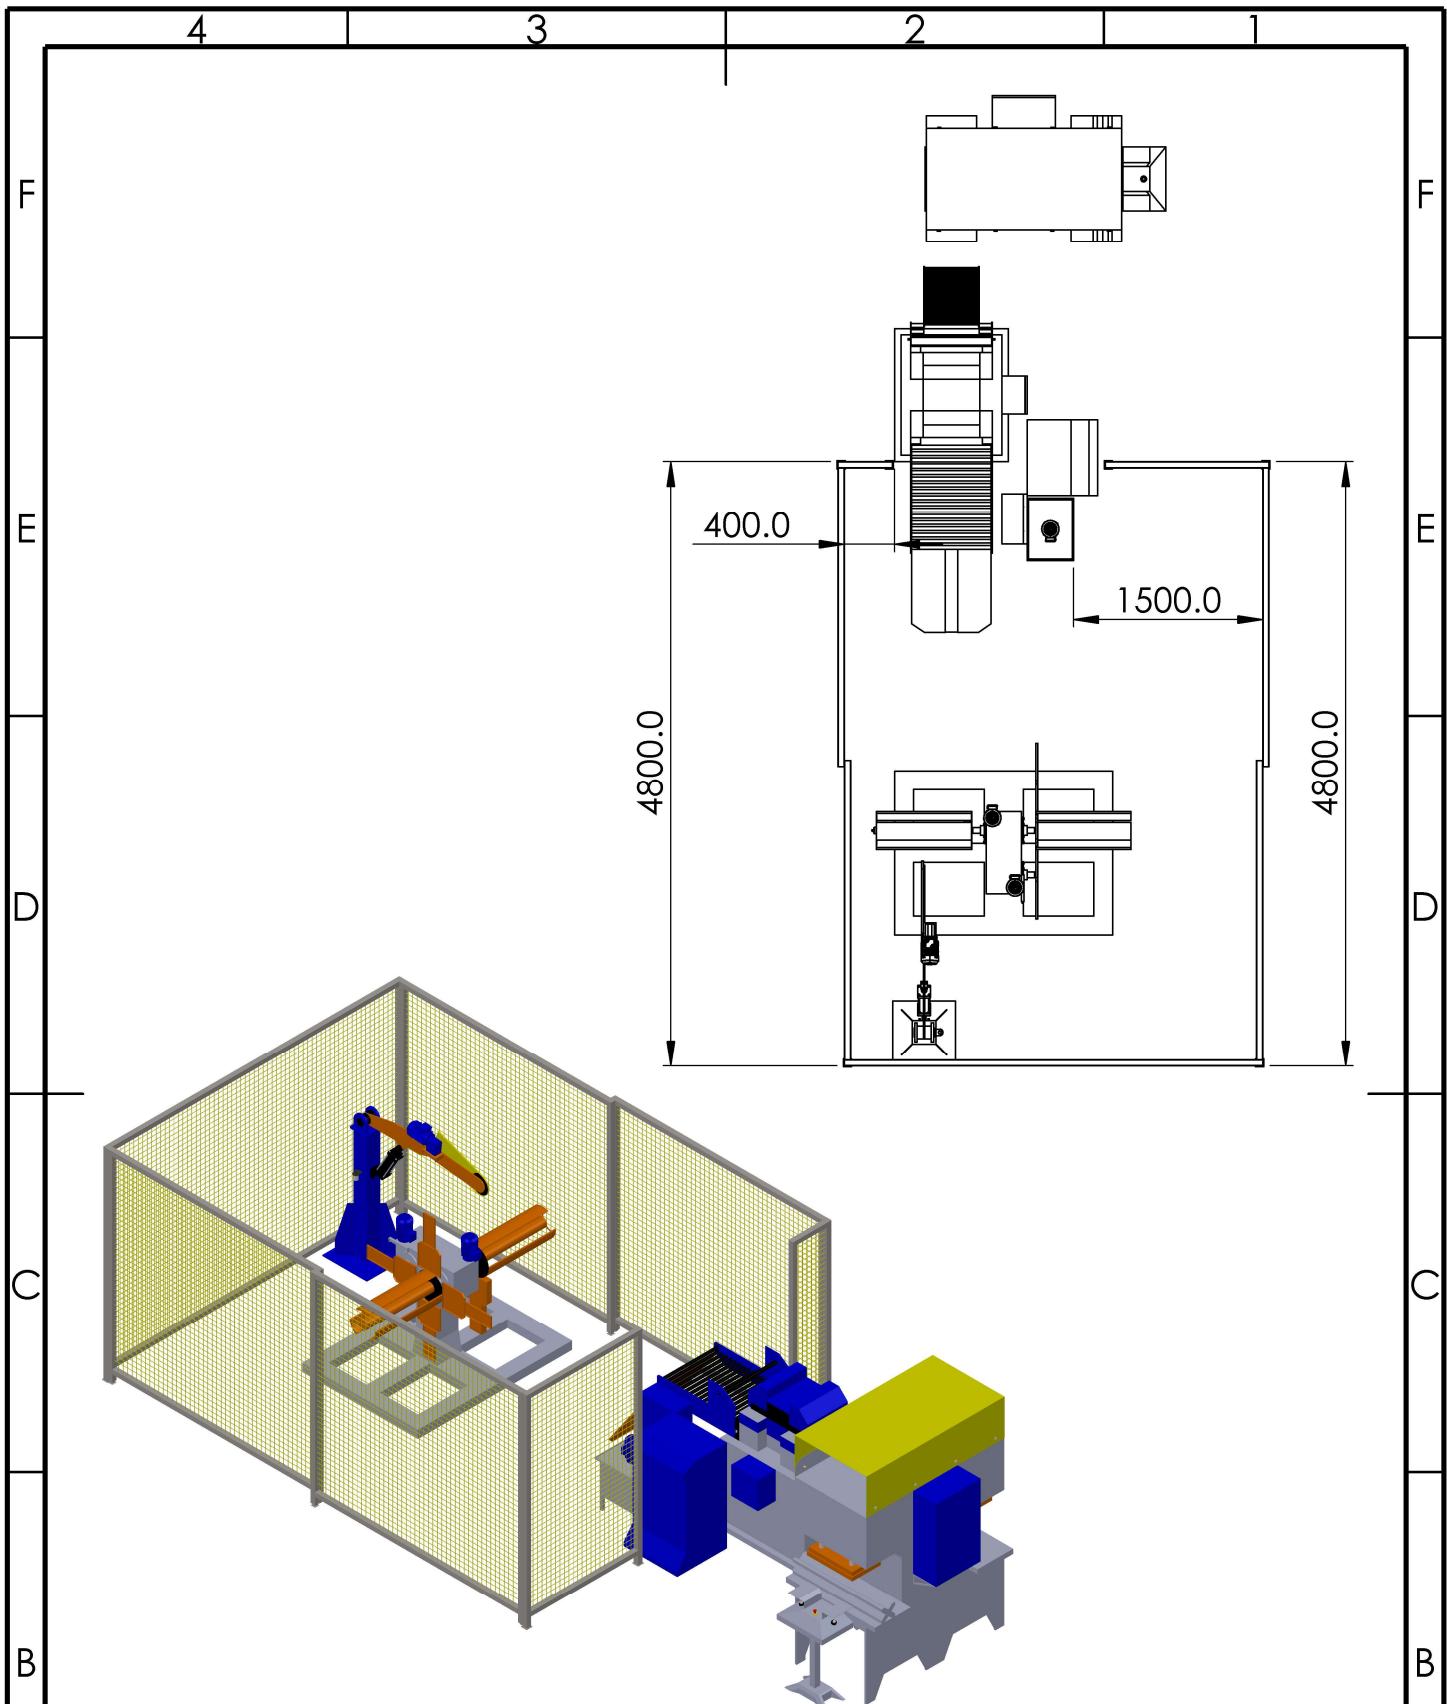

EMPRESA:

GRUPO NORMATEC

CLIENTE:

ISOESTE METALICA INDUSTRIA E COMERCIO LTDA.
CNPJ: 37.249.299/0001-22

DESCRIÇÃO:

PRENSA HIDRÁULICA

FABRICANTE: HIDRAL - MAC

APROVAÇÃO: MATHEUS FIALHO

DATA: JANEIRO/2024

TAG: PRH - 1231

ANO: 2011

NÚMERO: 3285

ESCALA: S/E

MATERIAL: