

ITENS	NOMES
01	PROTEÇÃO FIXA 01
02	PROTEÇÃO FIXA 02
03	PROTEÇÃO FIXA 03
04	PROTEÇÃO MÓVEL COM SENSOR DE MOVIMENTO 01
05	PROTEÇÃO MÓVEL COM SENSOR DE MOVIMENTO 02
06	PROTEÇÃO MÓVEL COM INTERTRAVAMENTO 01
07	PROTEÇÃO MÓVEL COM INTERTRAVAMENTO 02
08	PROTEÇÃO FIXA P/ SAÍDA DO MATERIAL
09	CONTROLE CABEADO FUNÇÃO JOG
10	PROTEÇÕES FIXAS FRONTAIS
11	BOBINADOR
12	PERFILADEIRA CANTONEIRA
13	ESTEIRA P/ SAÍDA DO MATERIAL

EMPRESA:

GRUPO NORMATEC

CLIENTE:

ISOESTE METALICA INDUSTRIA E COMERCIO LTDA.
CNPJ: 37.249.299/0001-22

DESCRÍÇÃO:

PERFILADEIRA CANTONEIRA

FABRICANTE: SHAOXING

APROVAÇÃO: MATHEUS FIALHO

DATA: JANEIRO/2024


TAG: 1204


ANO: N/C


NÚMERO: N


ESCALA: 1 : 60


MATERIAL:

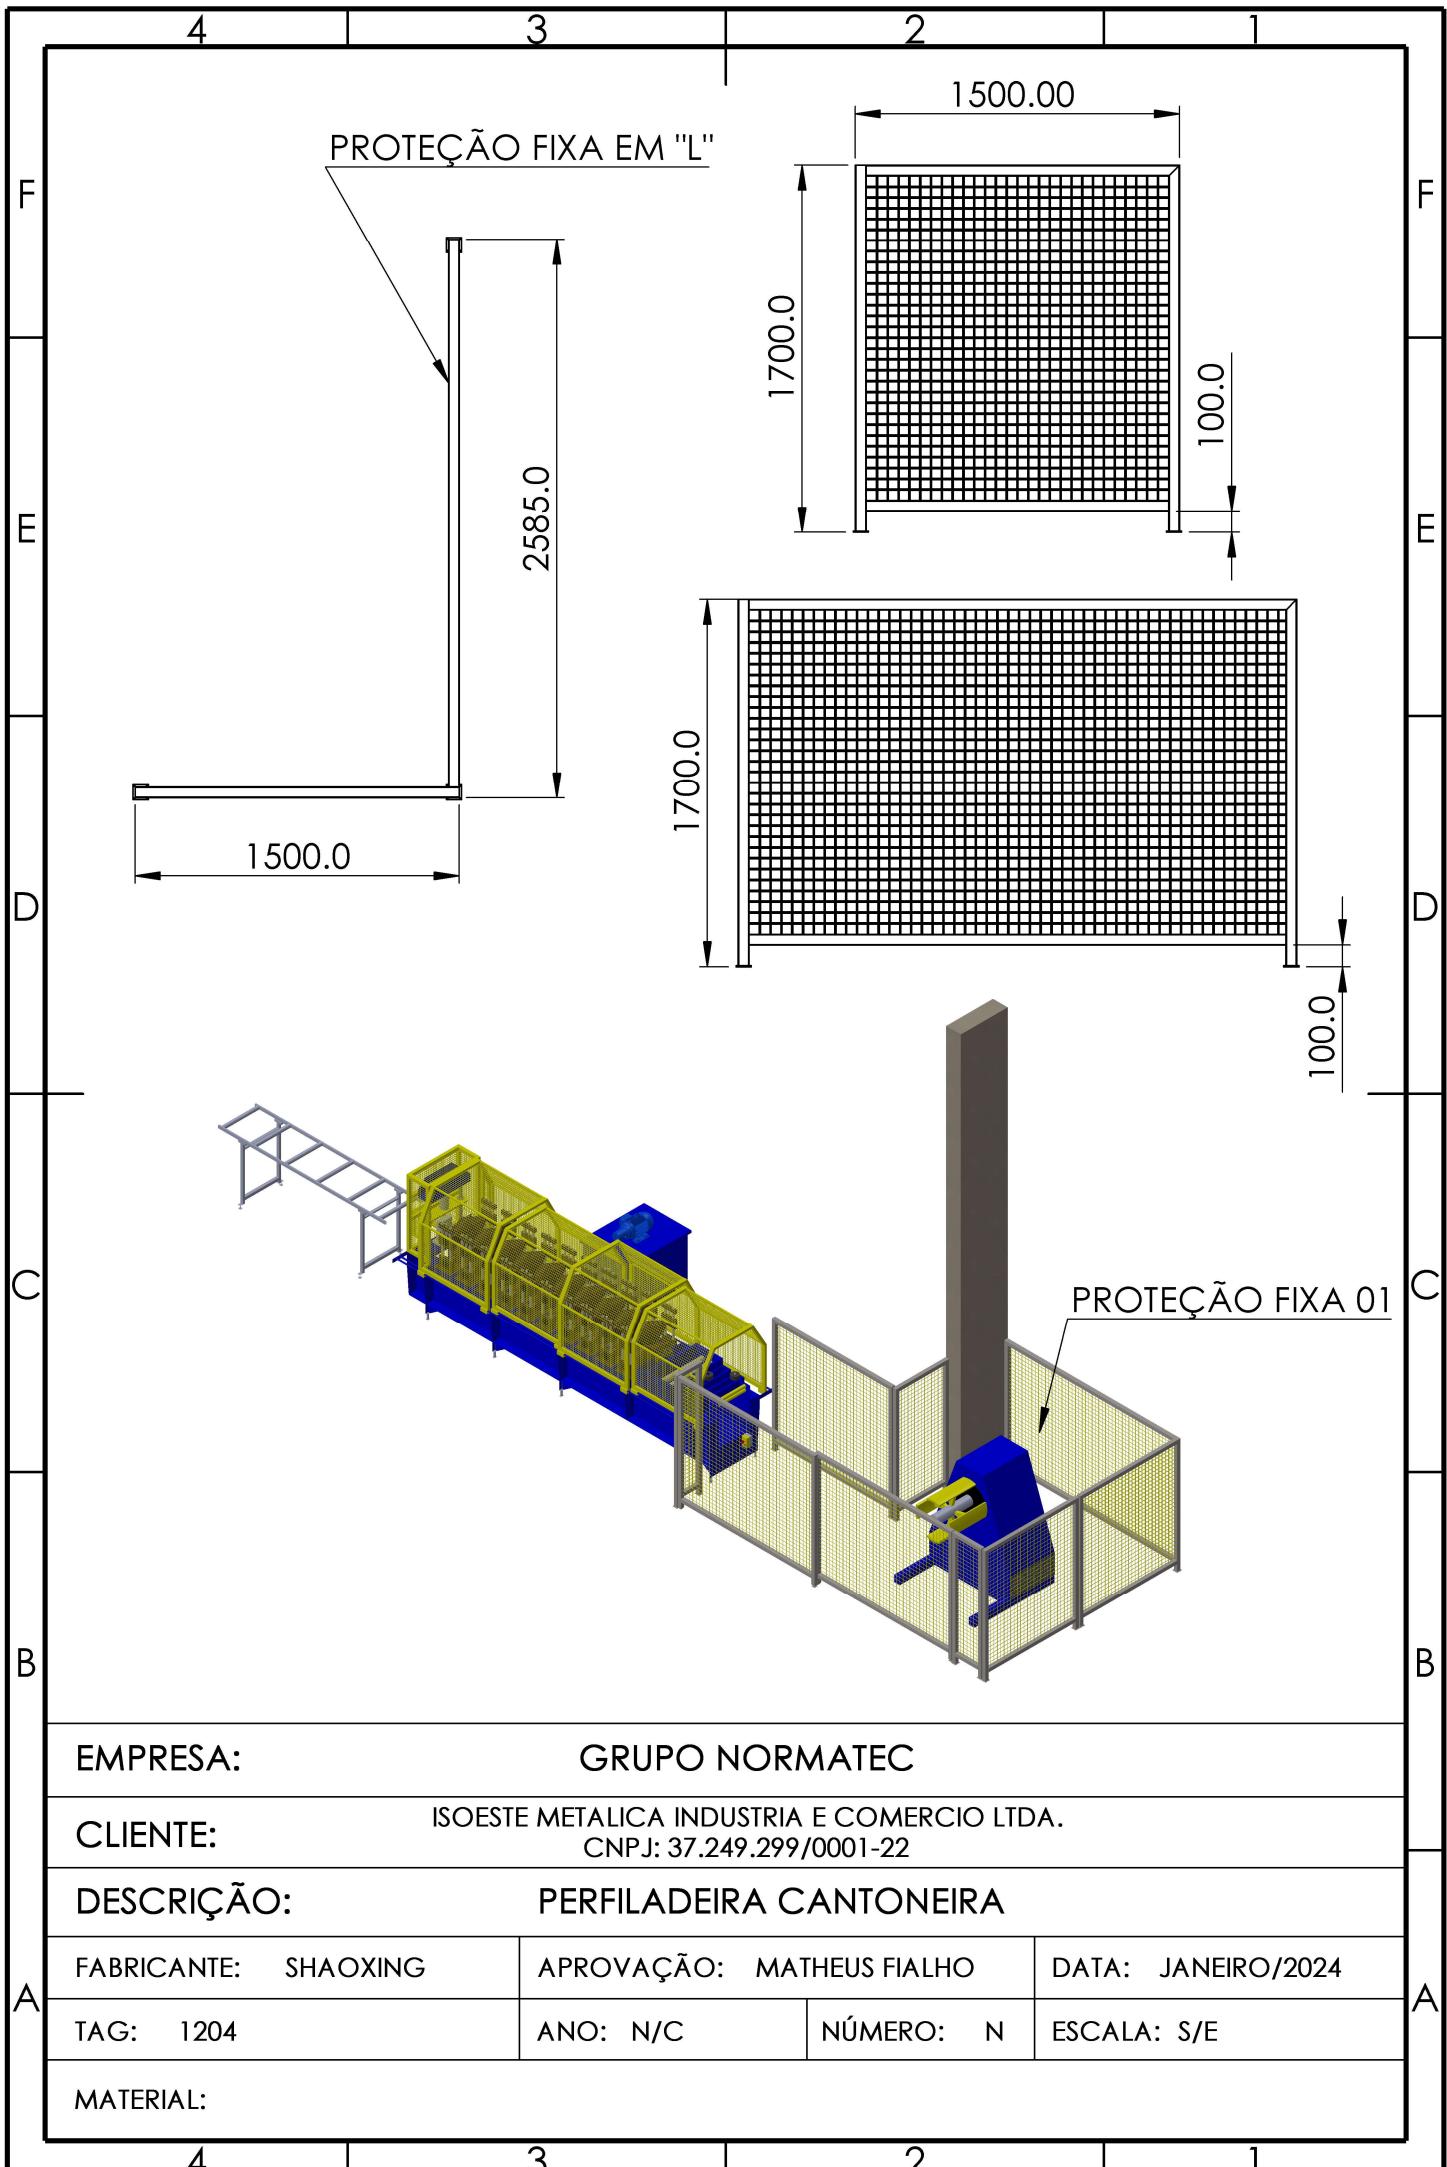


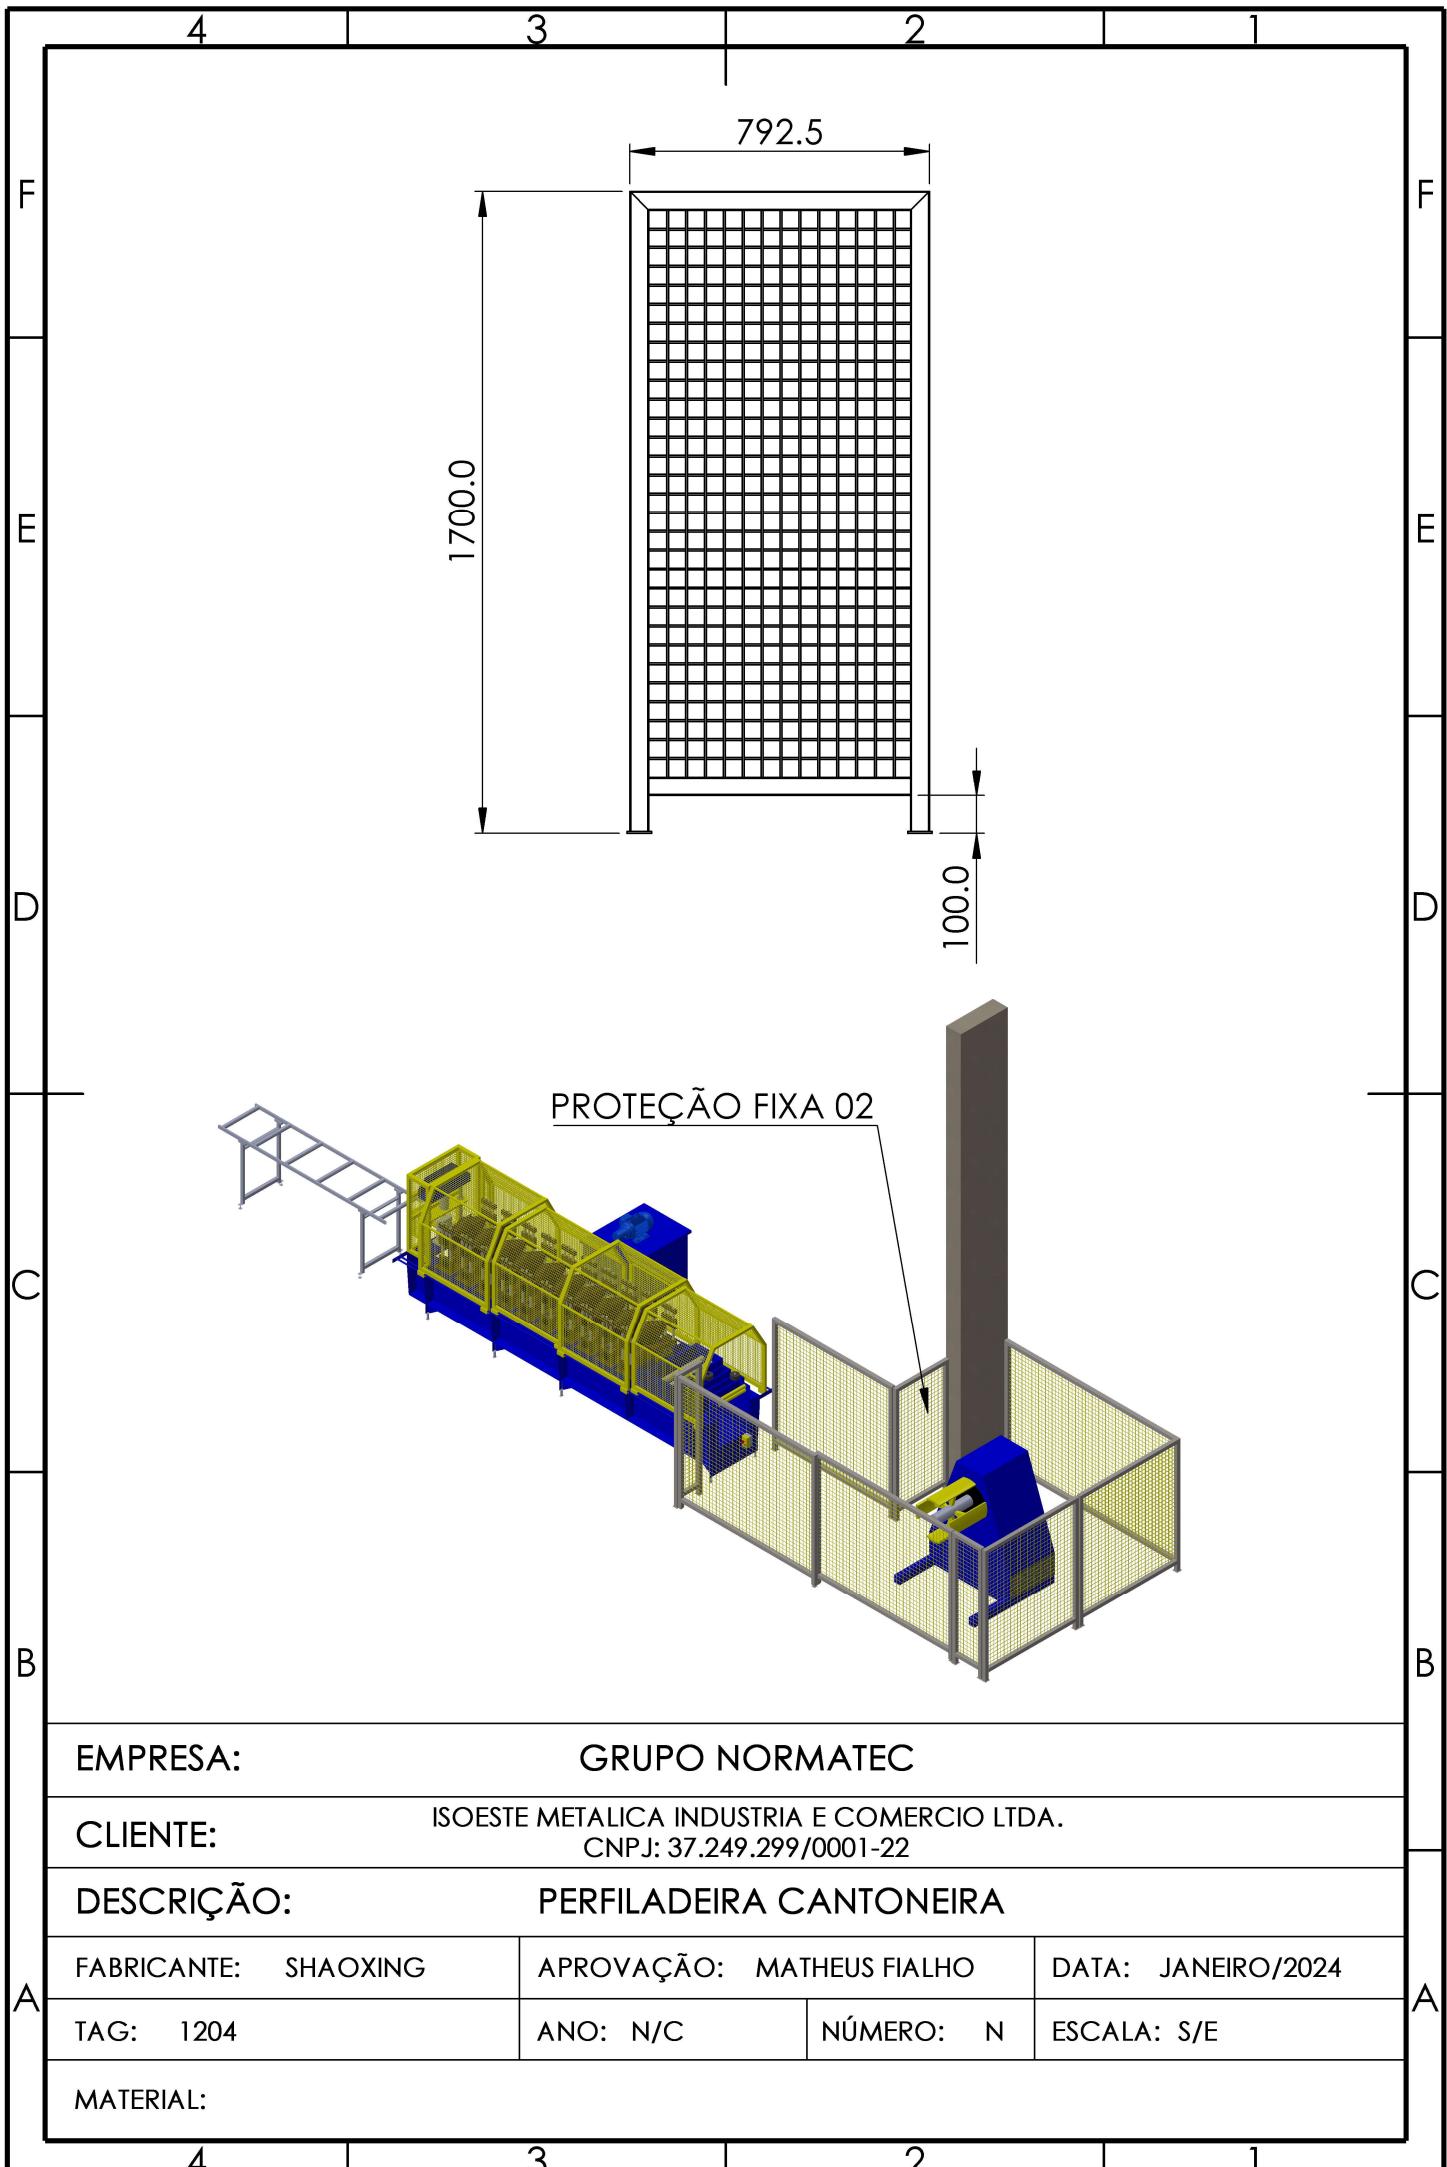


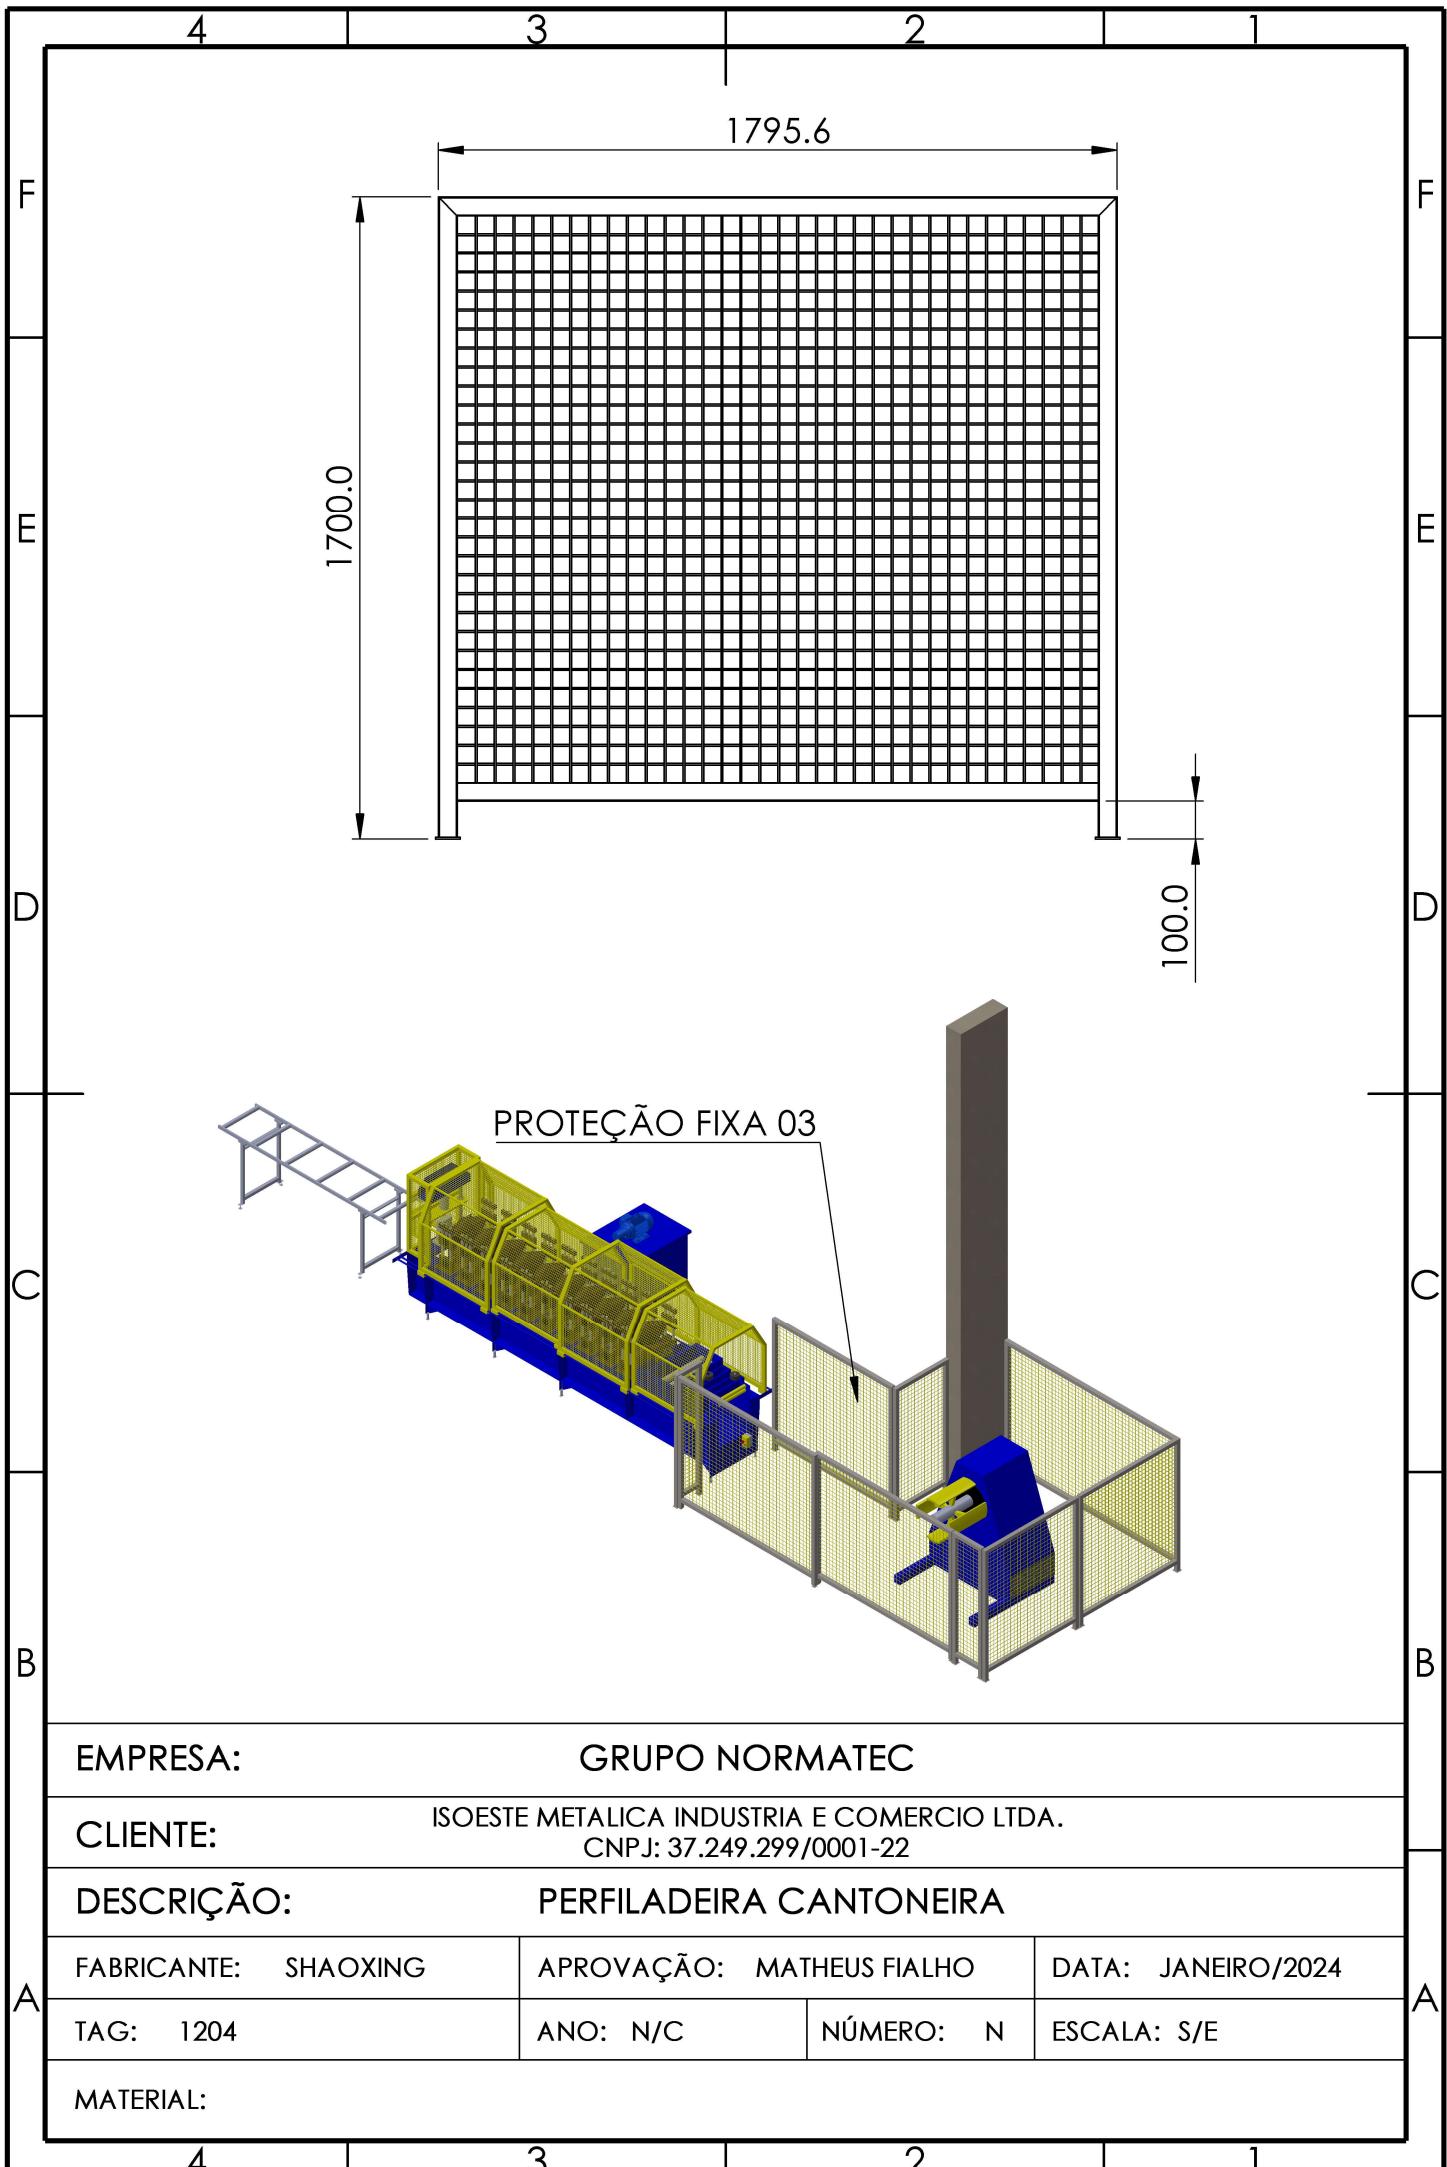


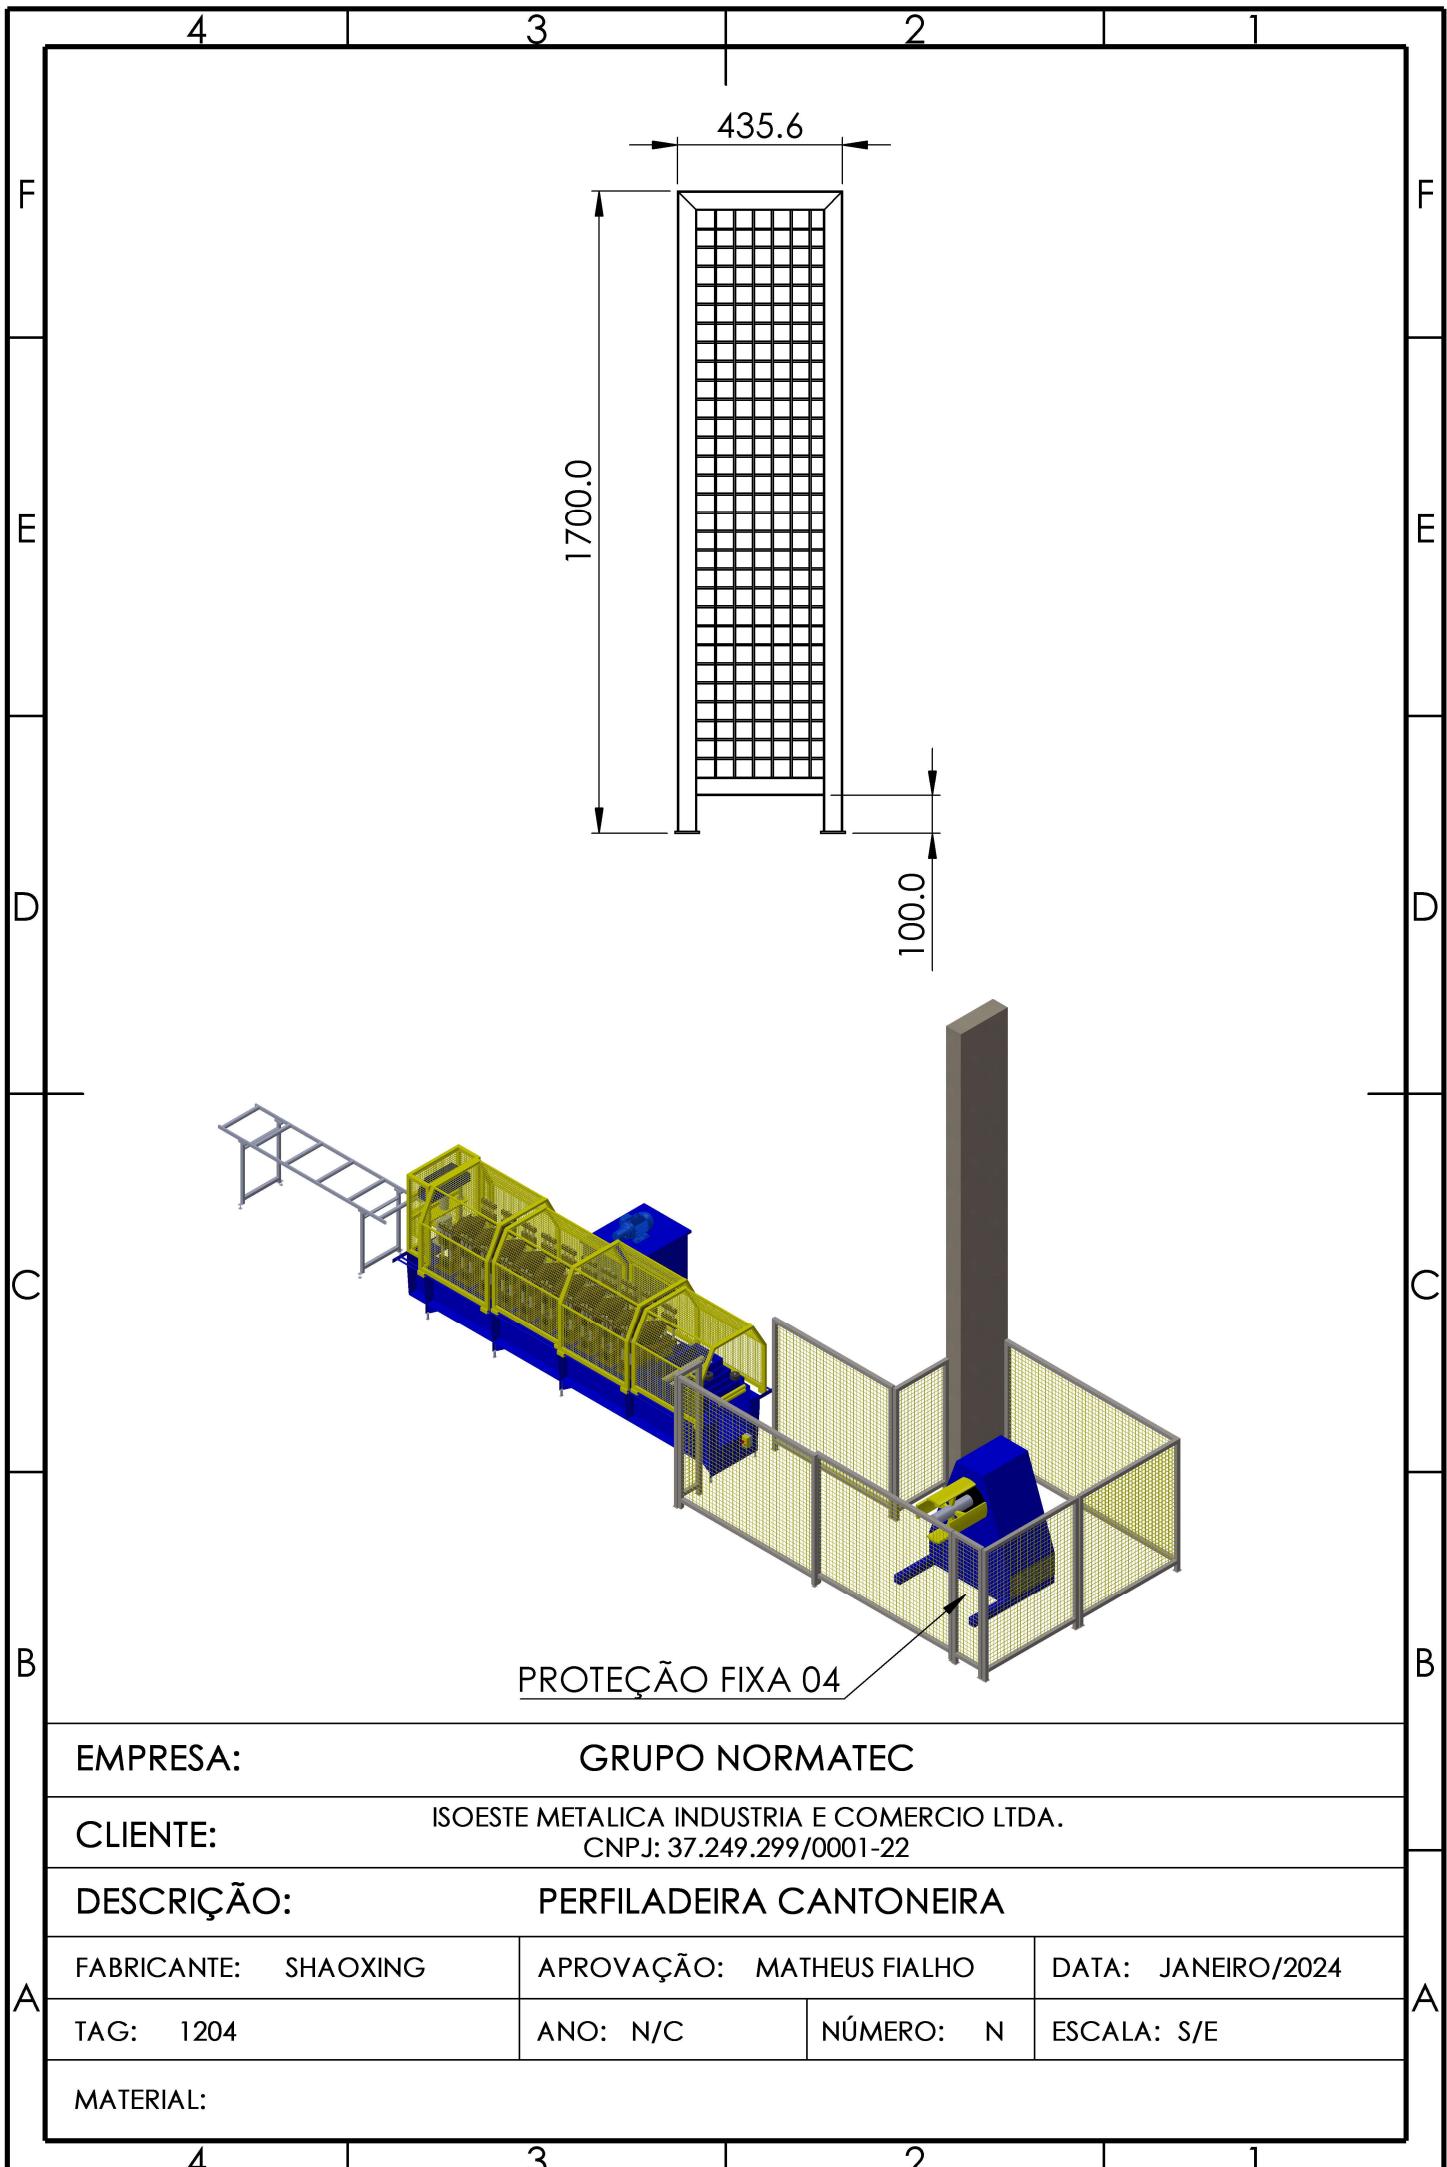


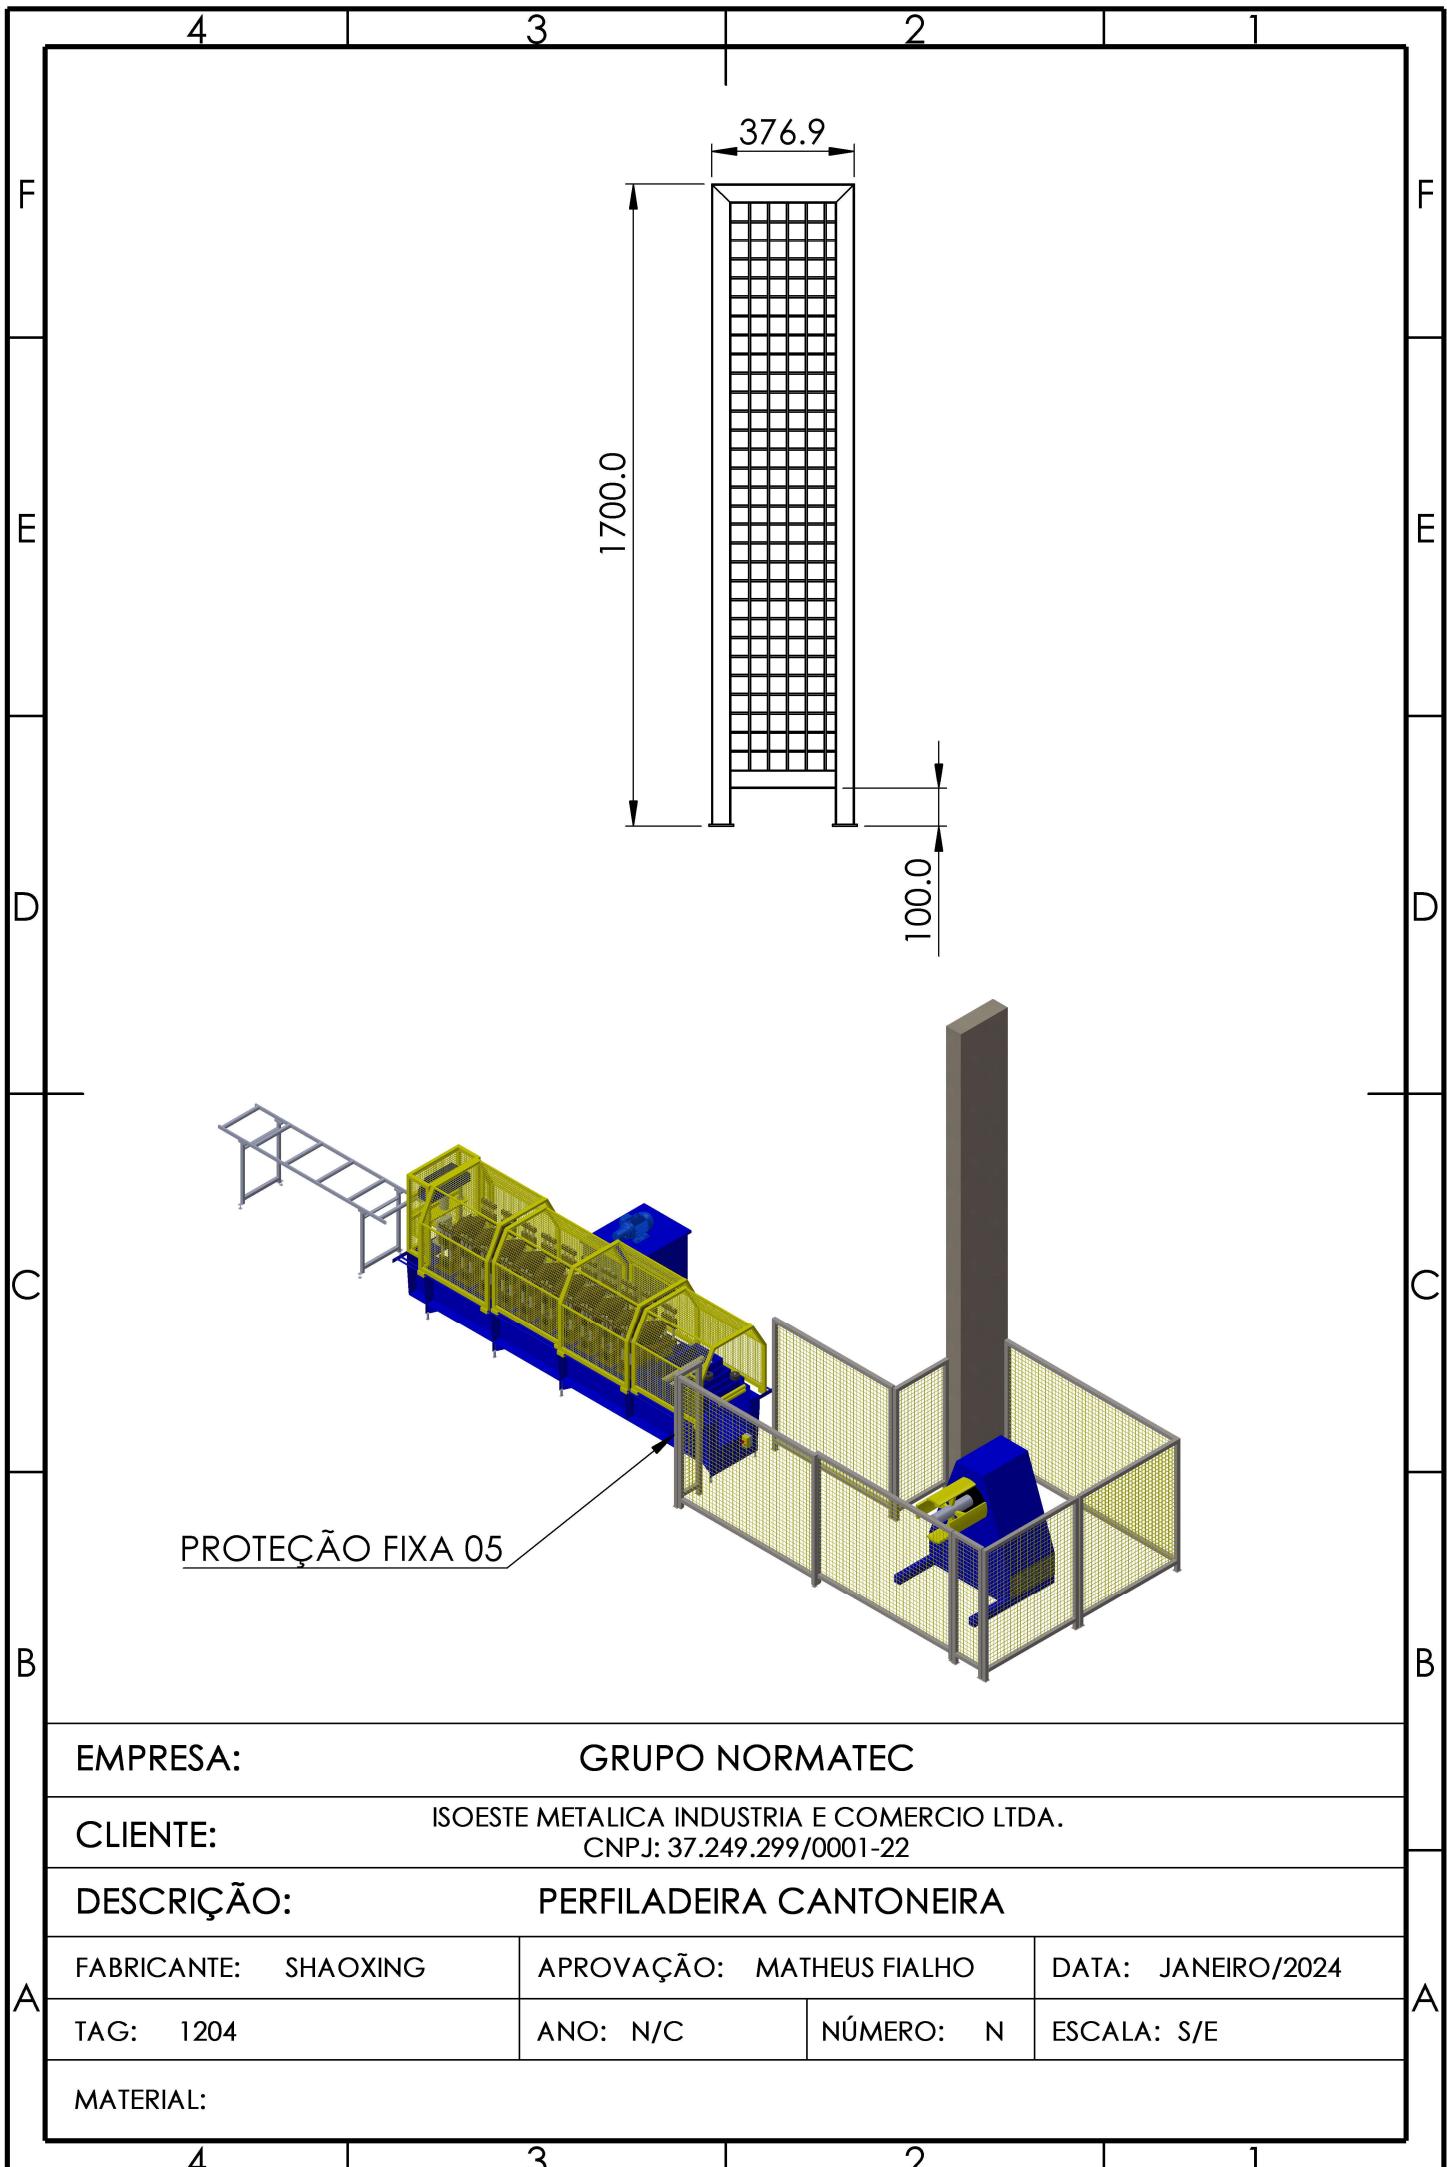


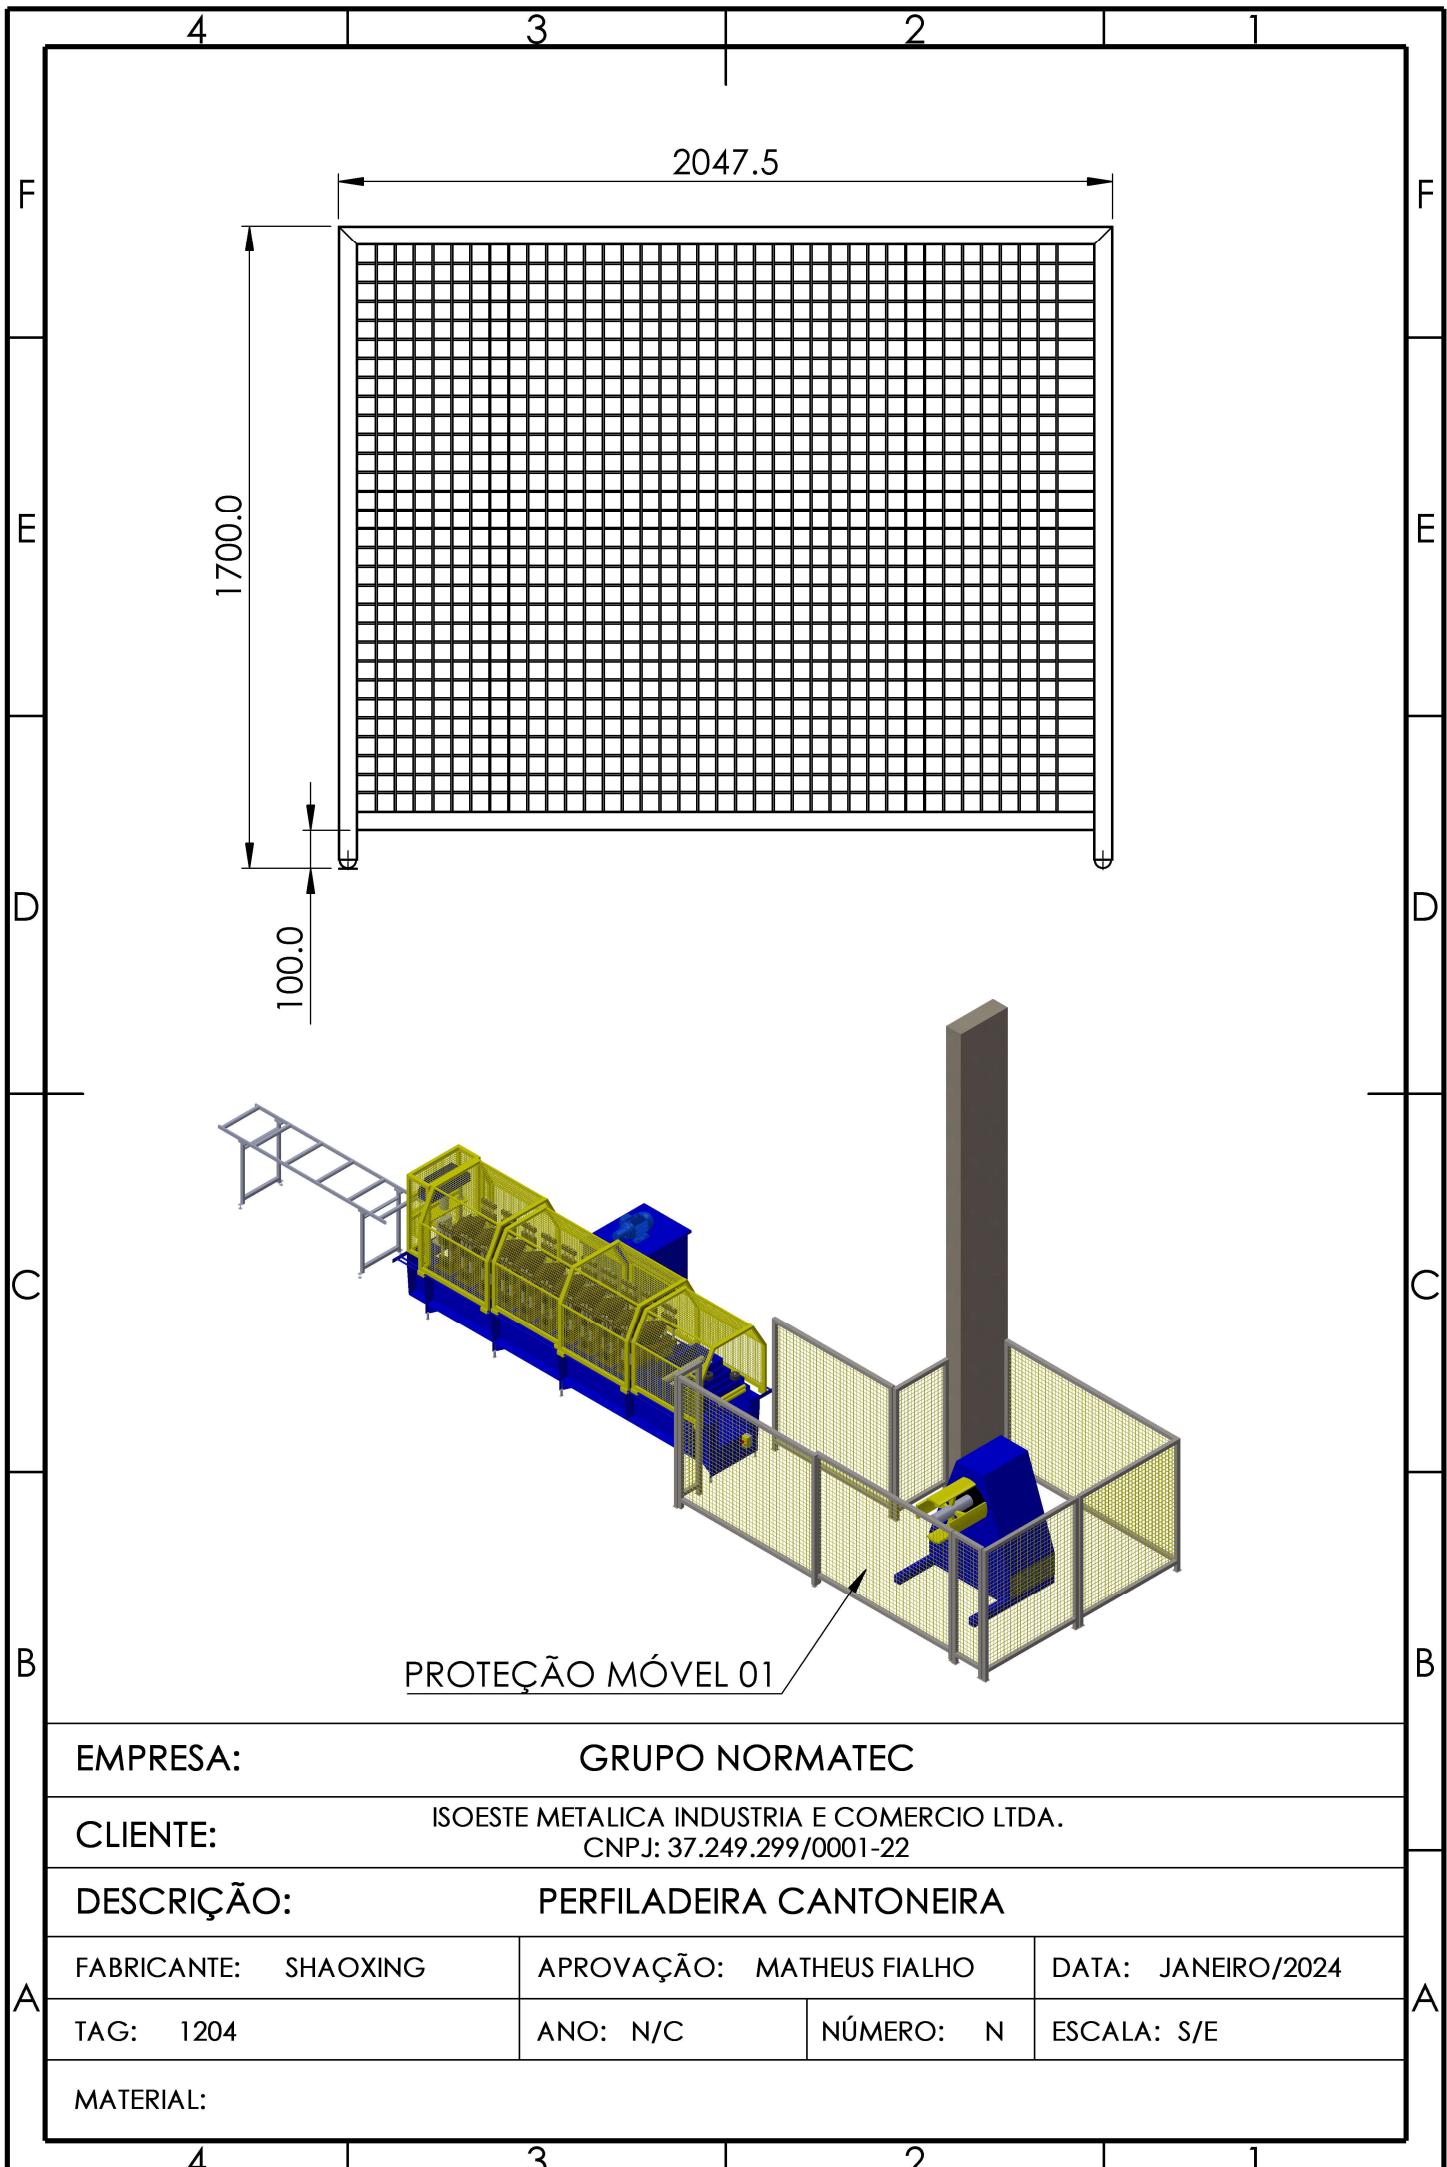


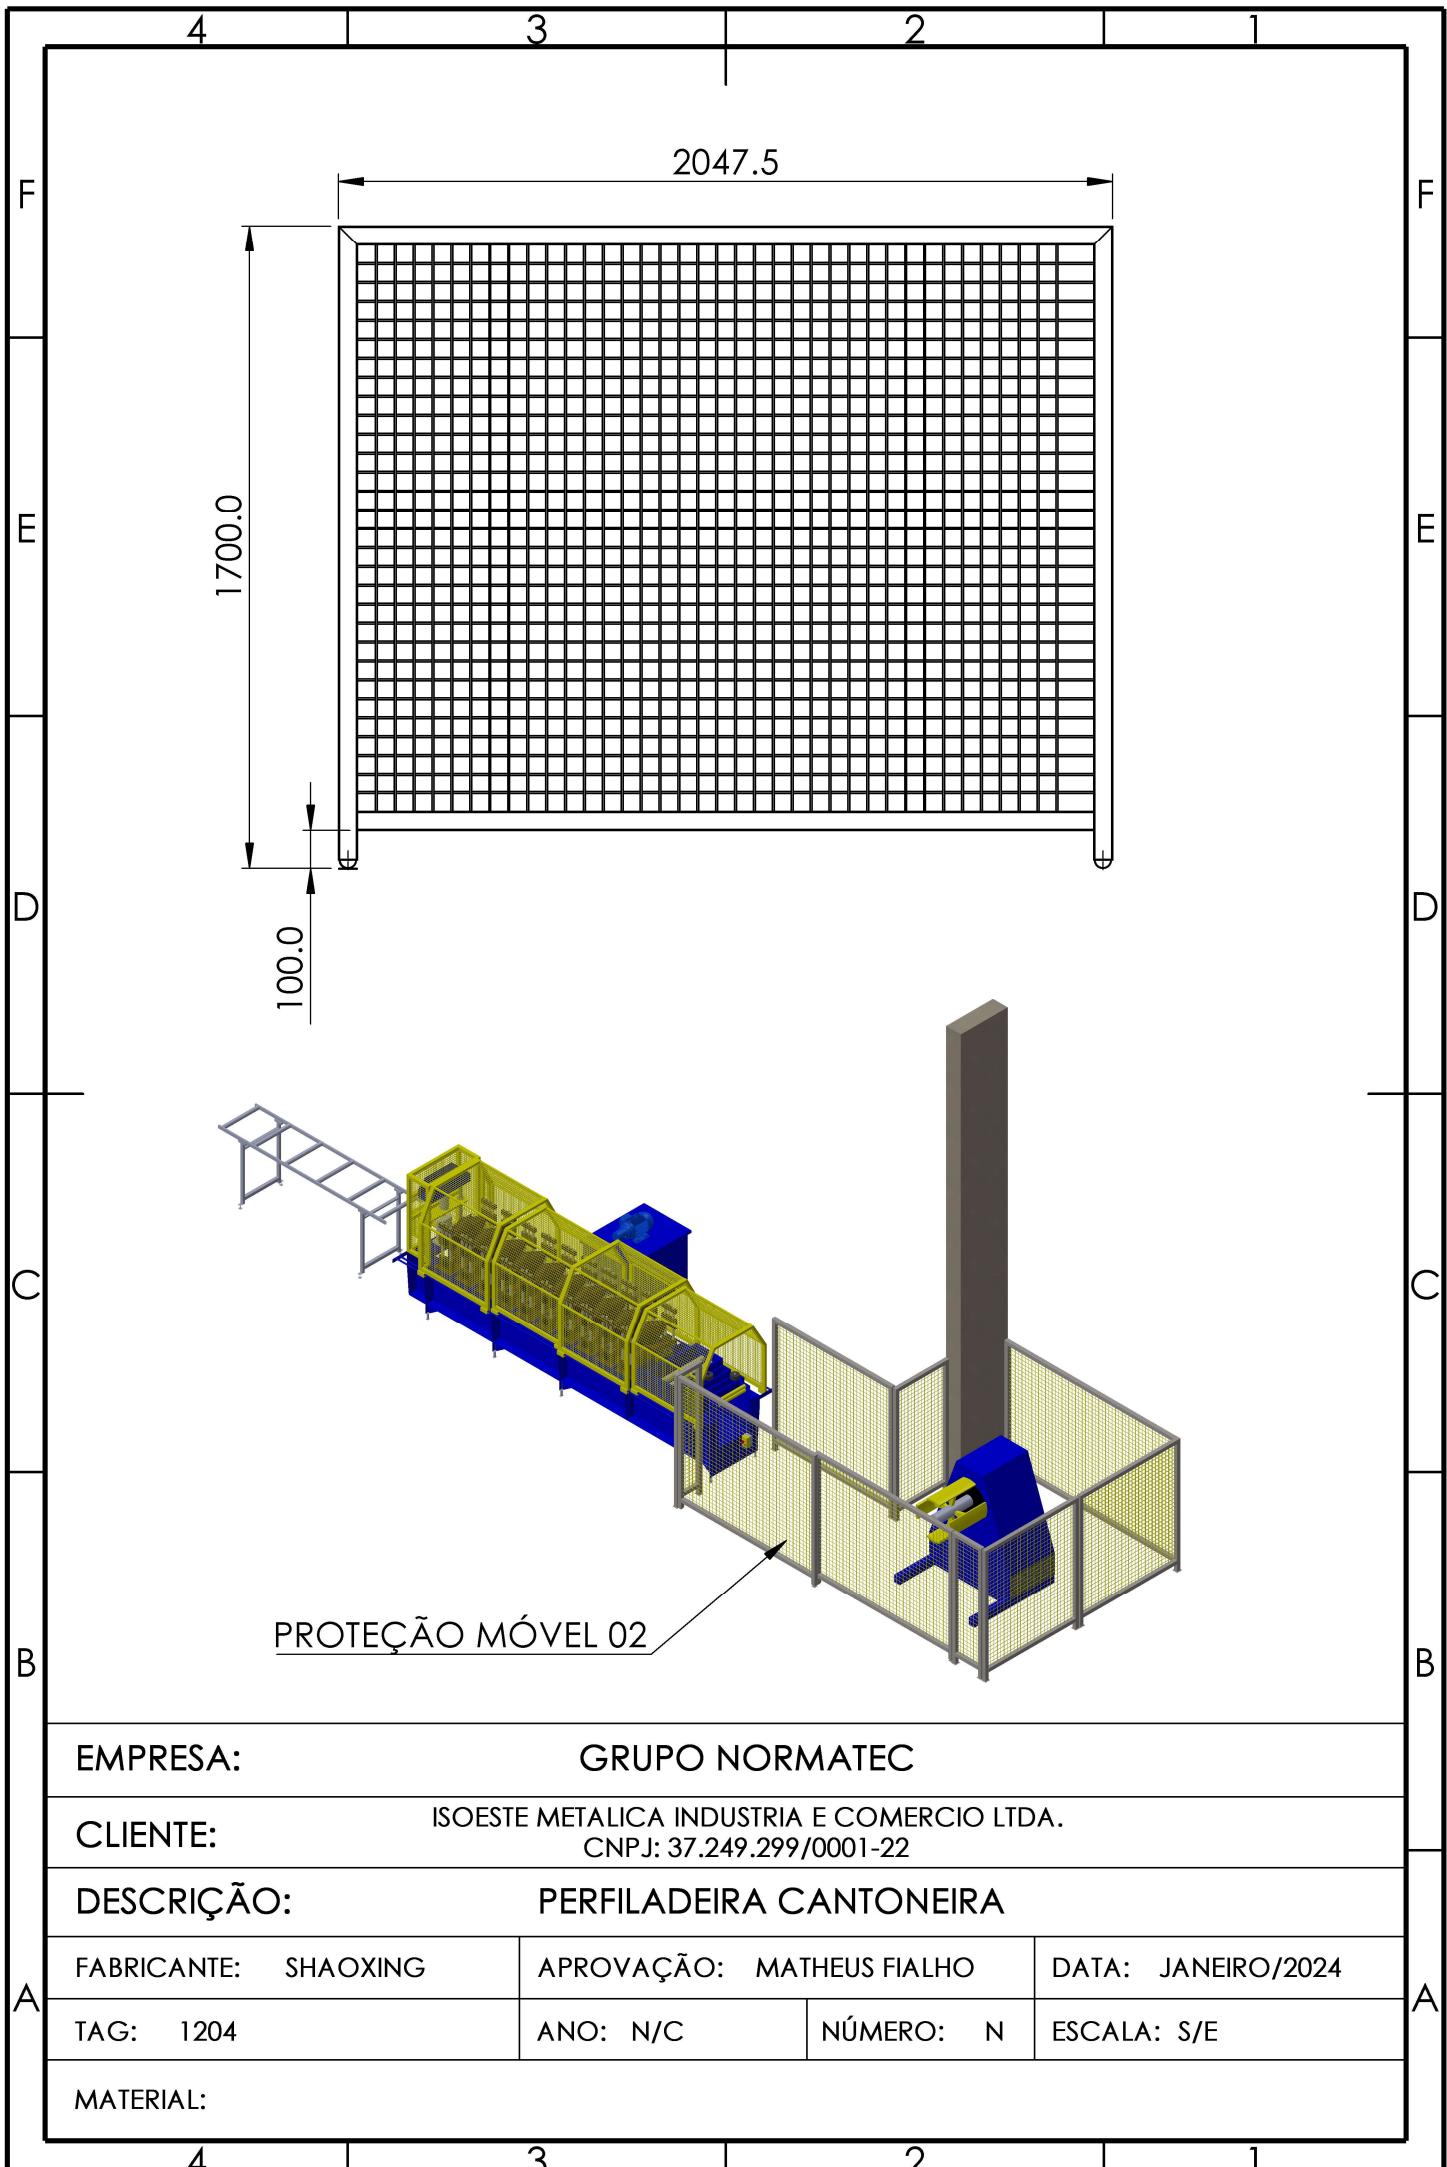

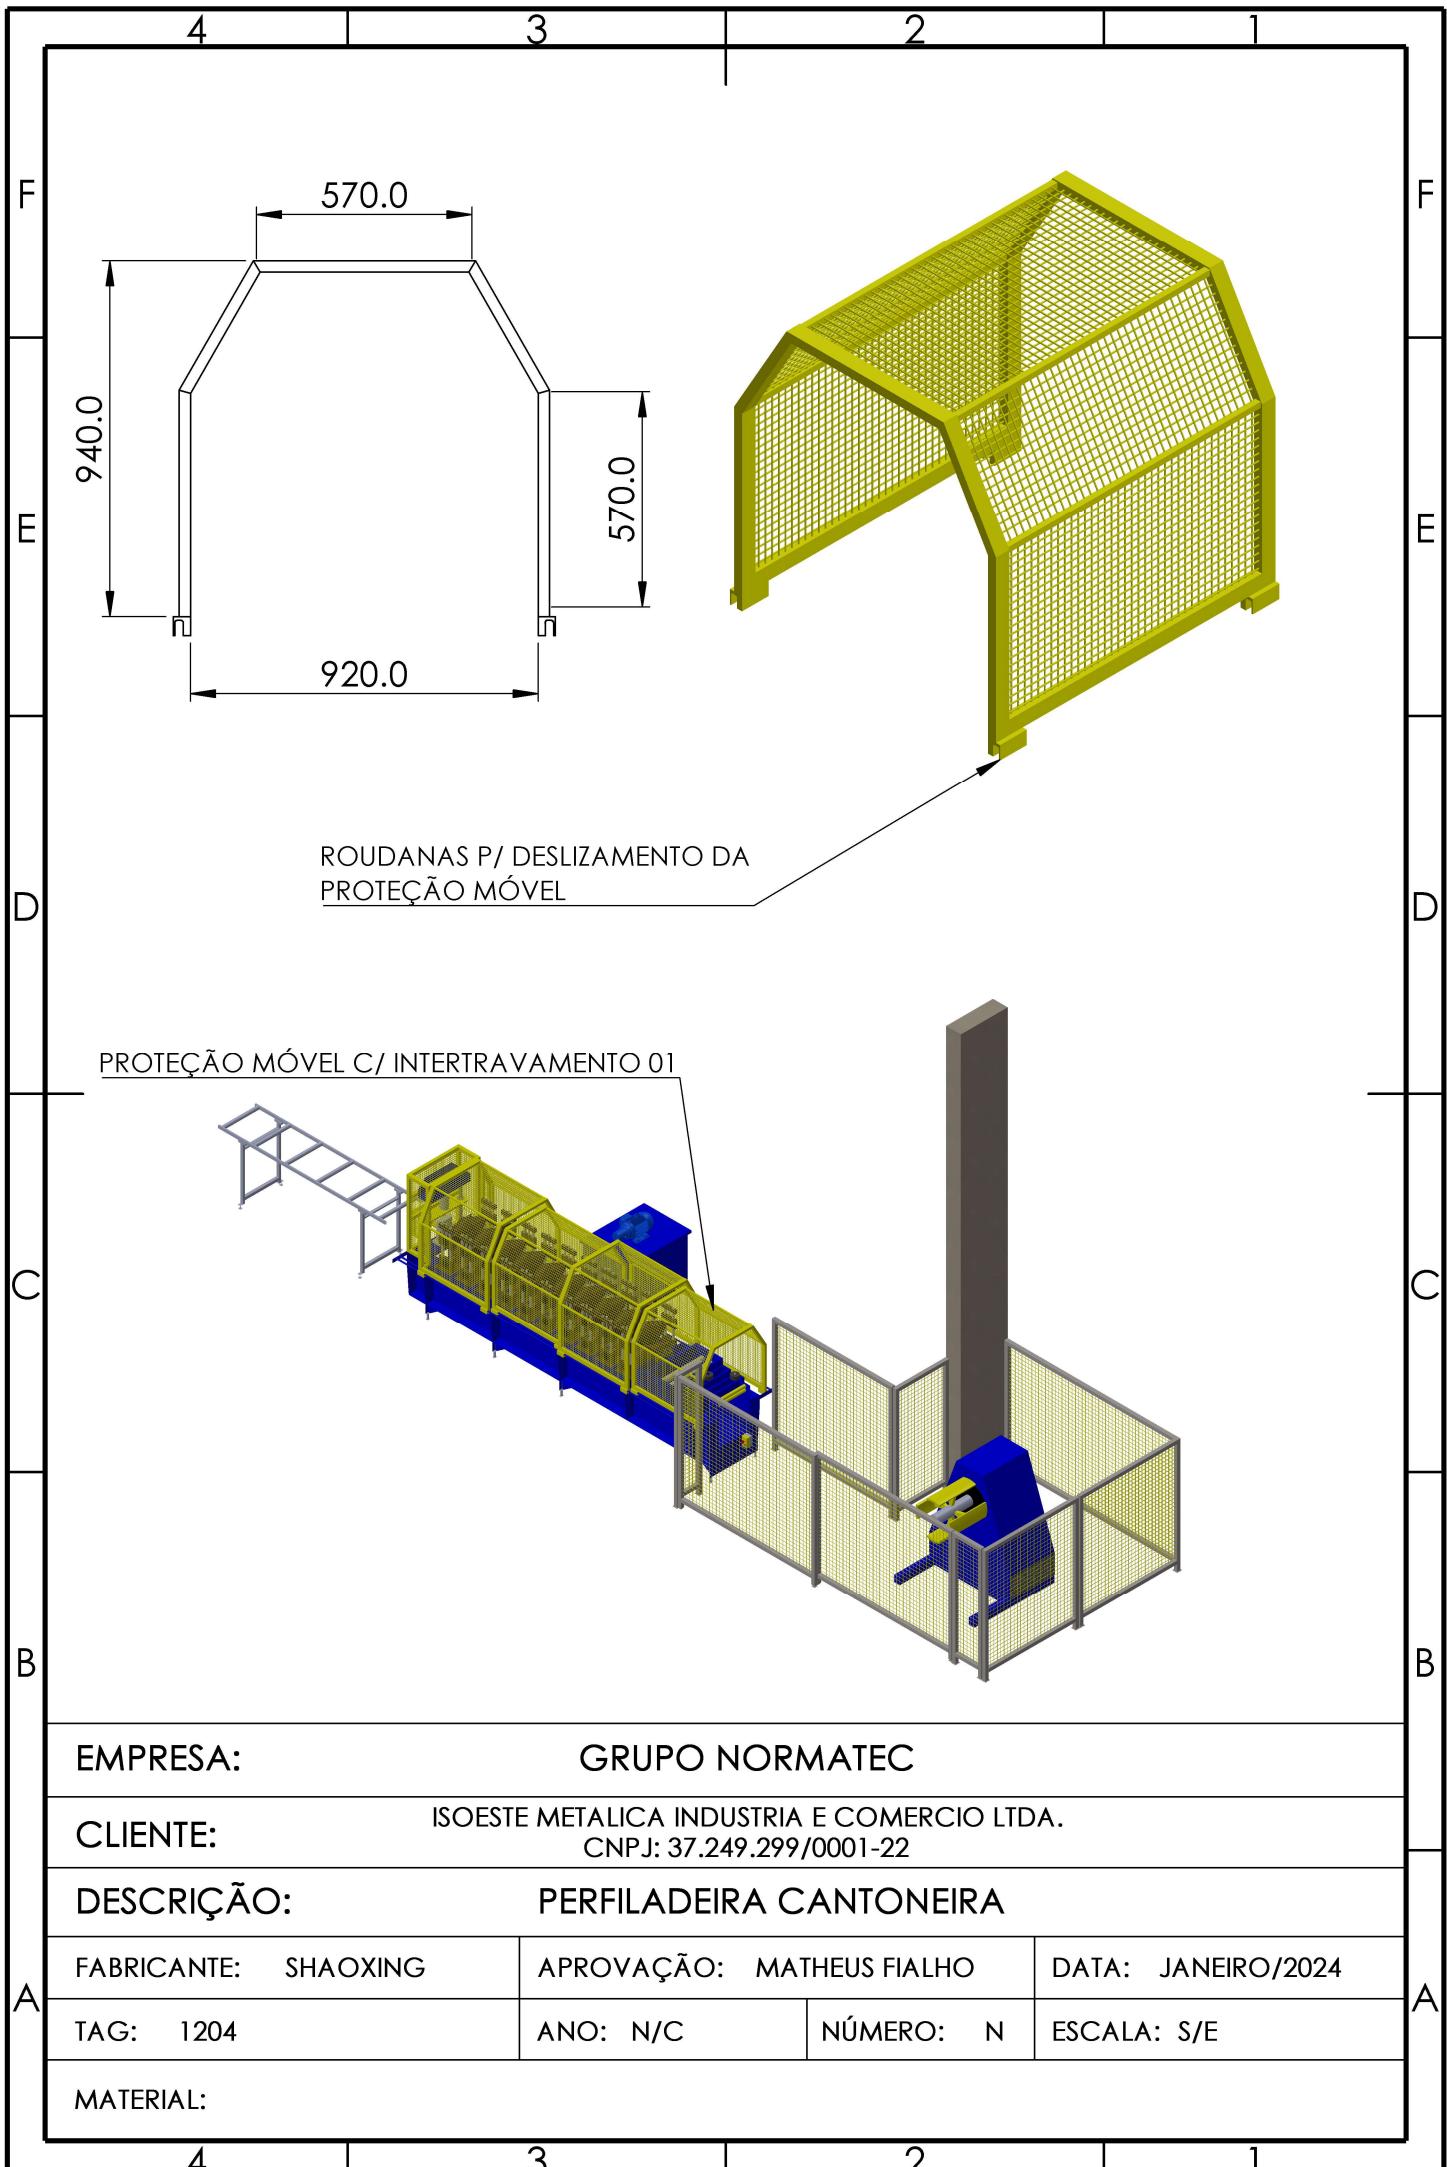

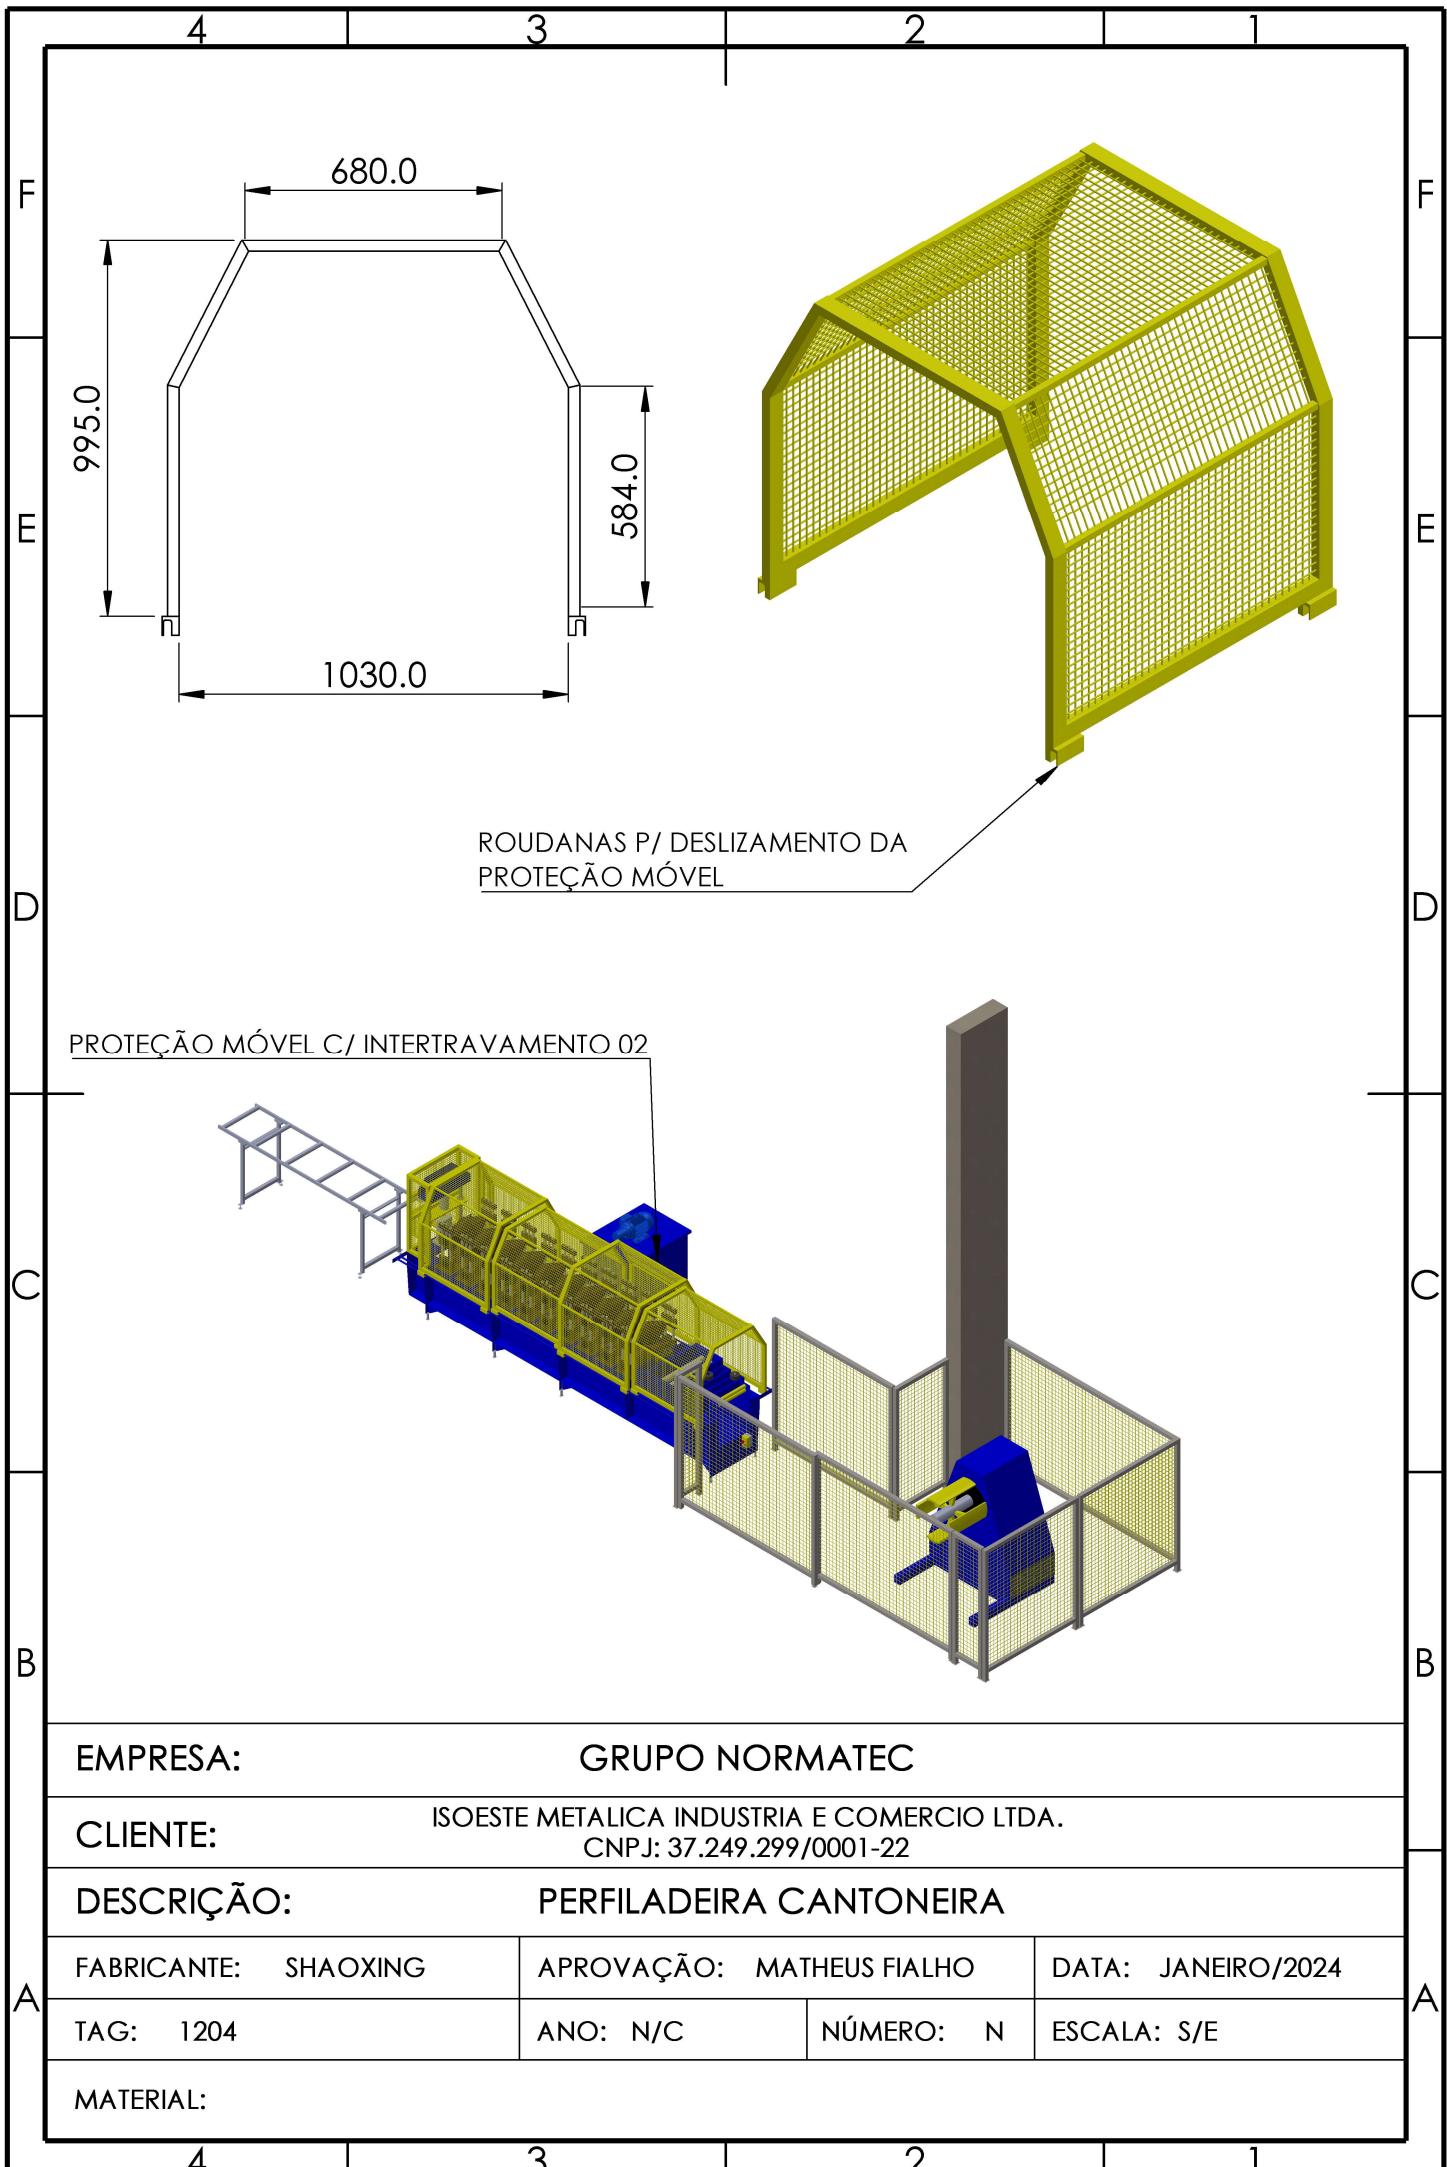

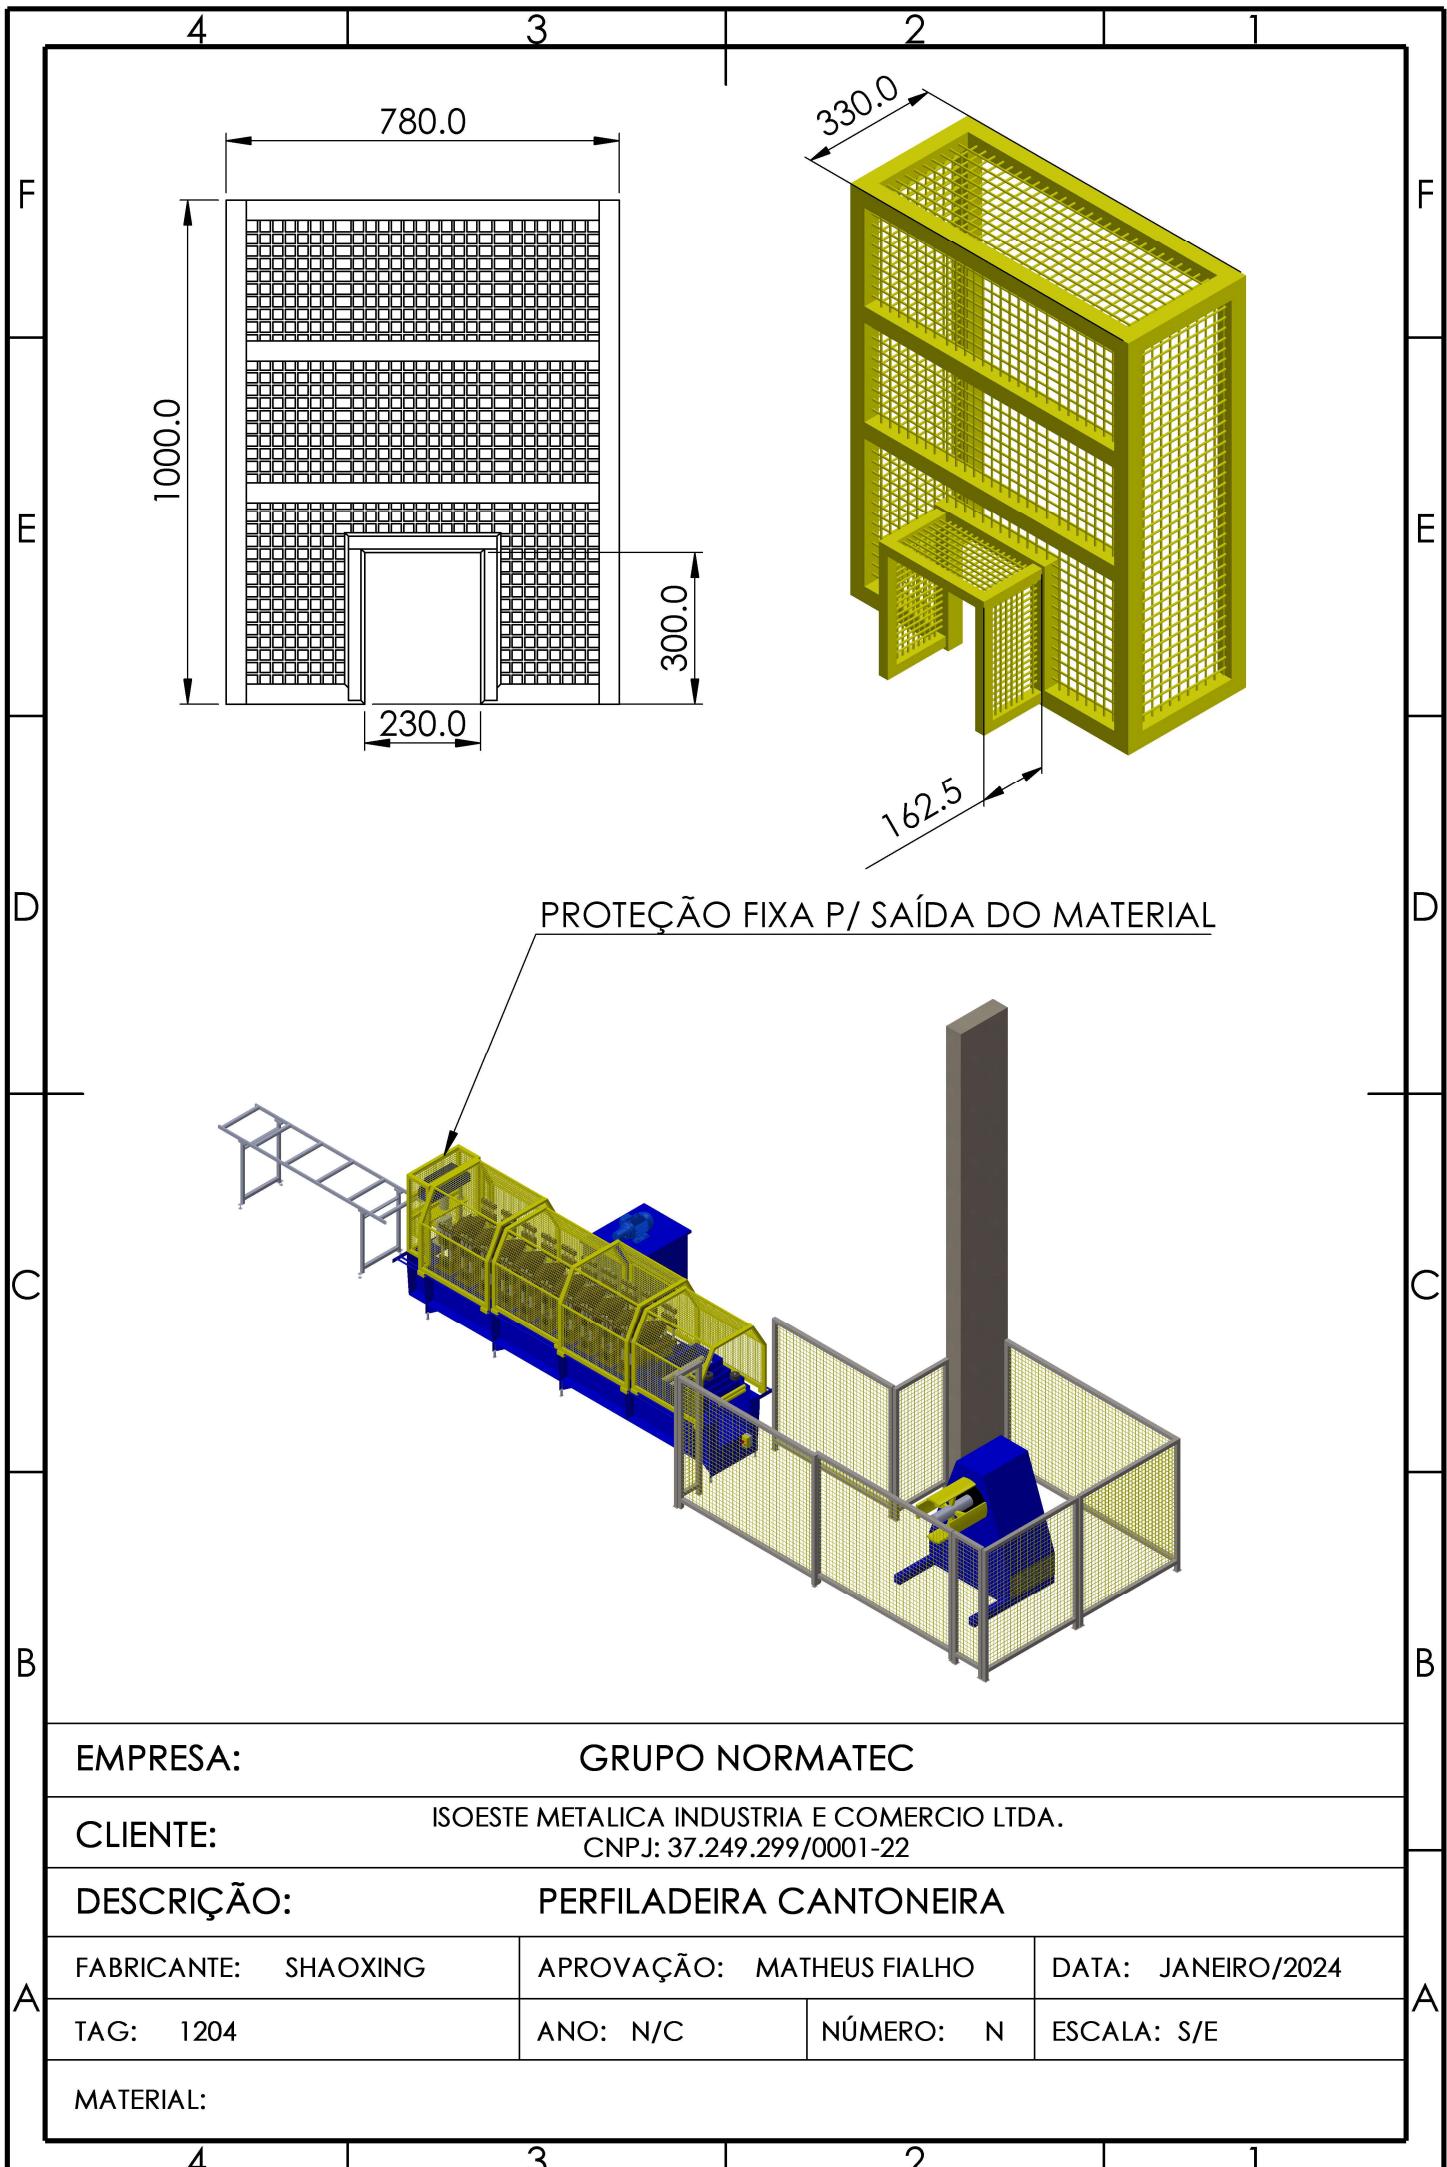

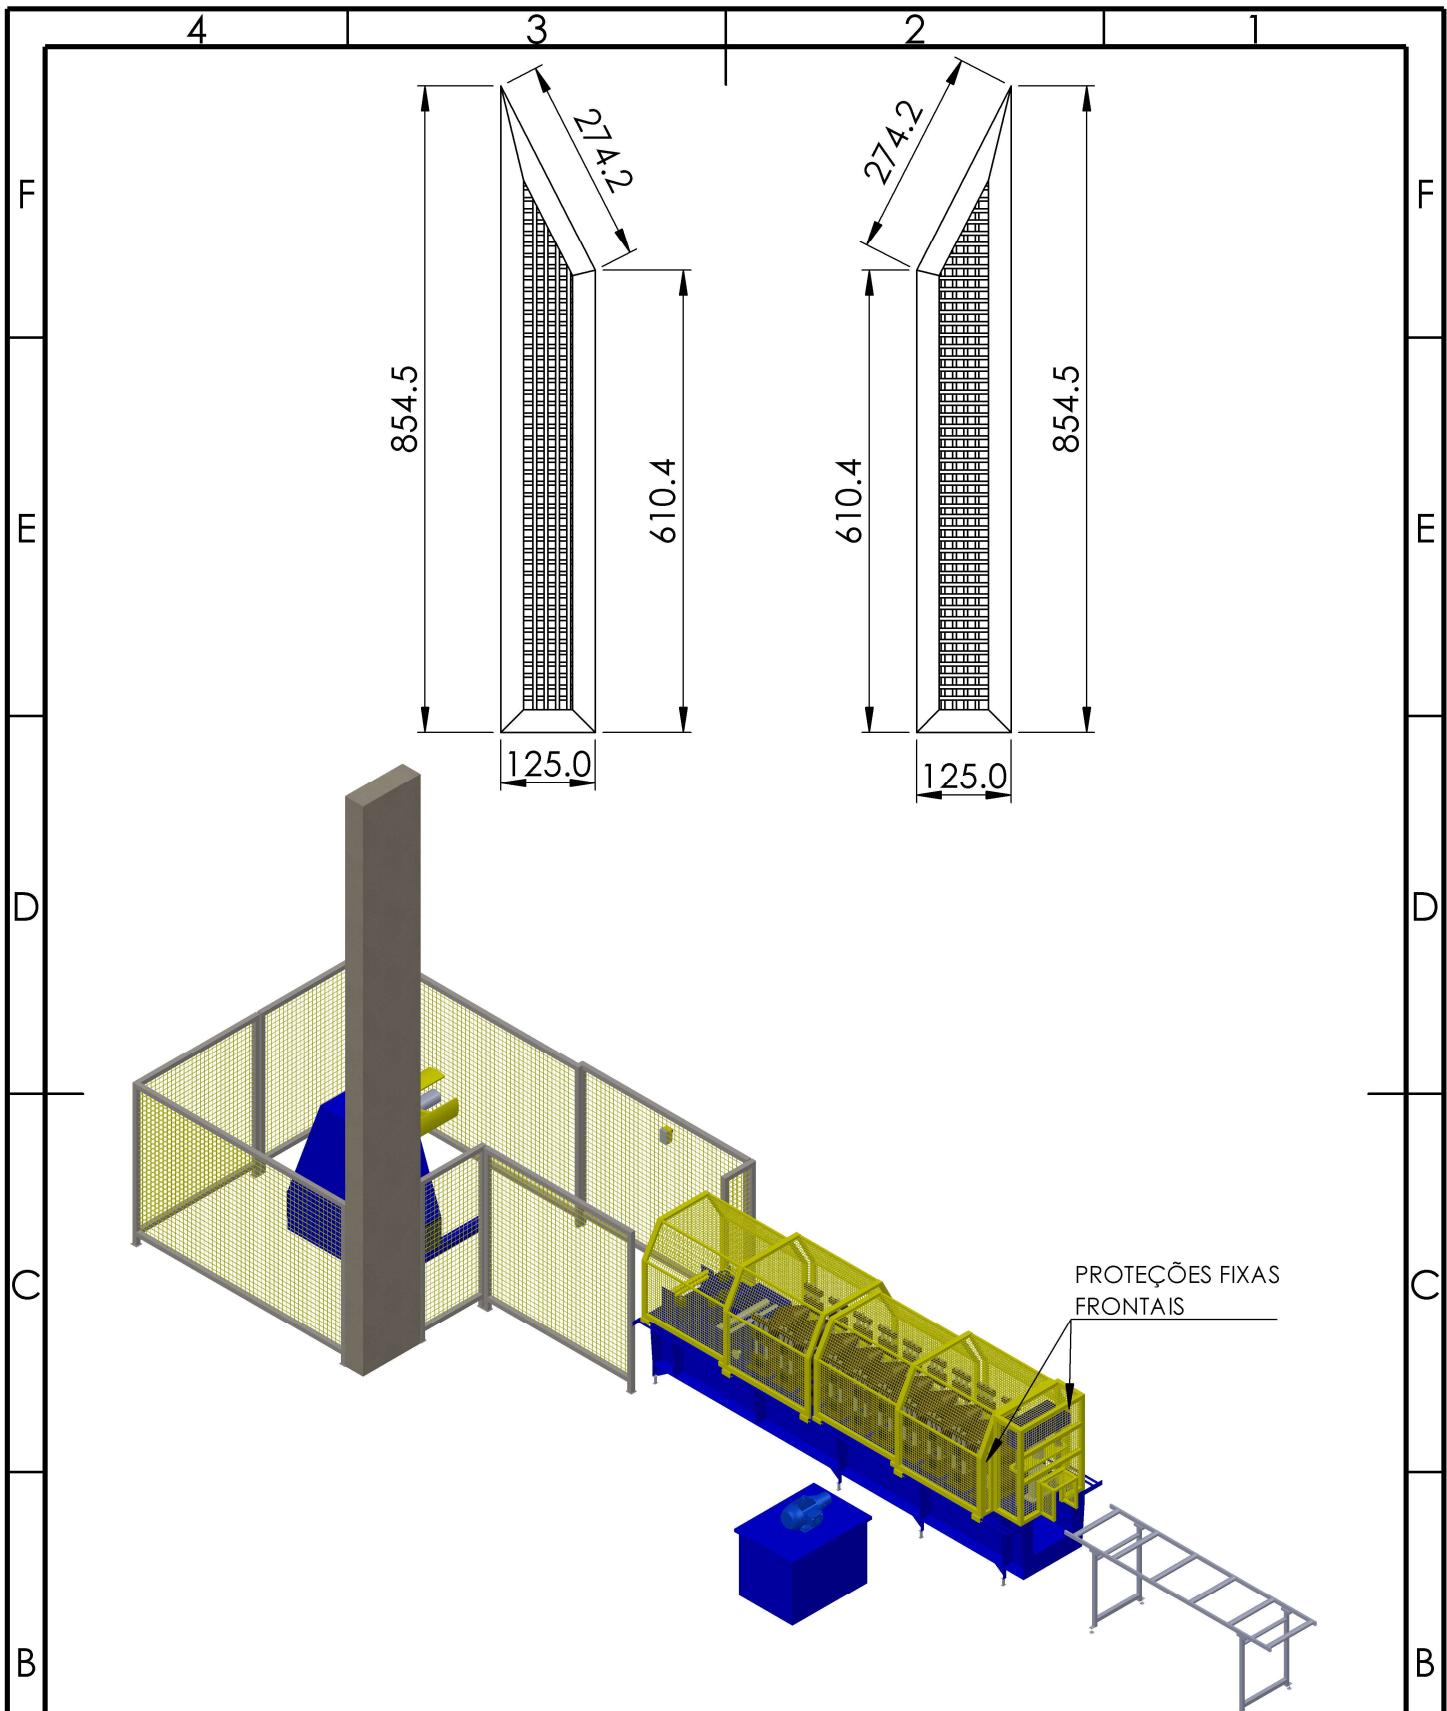

EMPRESA:

GRUPO NORMATEC

CLIENTE:

ISOESTE METALICA INDUSTRIA E COMERCIO LTDA.
CNPJ: 37.249.299/0001-22

DESCRIÇÃO:

PERFILADEIRA CANTONEIRA

FABRICANTE: SHAOXING

APROVAÇÃO: MATHEUS FIALHO

DATA: JANEIRO/2024

TAG: 1204

ANO: N/C

NÚMERO: N

ESCALA: S/E

MATERIAL: